松ヶ崎こども園　1敷地と自然環境

地に足をつけて育つ

比叡から降りる冷気と高野川の流れが出会う松ヶ崎の扇状地に、こどもたちが地に足をつけて育つ場所をつくる。

ゆるやかな弧を東の比叡にひらく木造平屋の本館に0歳から5歳のすべての部屋を並べ、縁側と深い庇で園庭とつなぐ。比叡に見立てた築山と、用水を借りて高野川に見立てた小川を置く。

オープンキッチンを玄関ホールに面する園の中心に据え、食べることを日々の求心力とする。野菜くずをこどもたちの手で土に還し、命の循環を知る。園庭にはチクチクする植物、季節ごとに香る木と実のなる木を植え、こどもたちは手と鼻と舌で季節を知る。

3 mスパンの木造架構によるスケルトン＆インフィルで用途の変化を受け止める。地域から様々なものを借り、無駄をせず巡らせて、こども園として地域に返す。

設計趣旨 約326字（課題は300字程度）。文字20 pt（5.1 mm）

4 災害時の持ちつ持たれつ

大洪水が予想される場合の緊急避難先として京都工芸繊維大学と協定（京都市ハザードマップによる浸水深1.5 m）。太陽光発電、蓄電池、地下水の利用によって、災害時に水を地域に提供。

3 お向かいさん

西の道の北半分は狭い道を挟んで向かいに住宅がある。圧迫感を与えないよう、この面の建物高さを1階程度に抑える。

⑥ 間伐材を使った林

京都北山の北山杉の間伐材141本を、ホールの林として立てる。

2 車と自転車の出入りを南にまとめる

西の道の中ほどでは、道に突き出た木が見通しをさえぎる。車と送り迎えの自転車の出入りはこの木より南にまとめ、出入口にはスピードバンプを置いて速度を落とす。

1 小竹薮公園を残す

地域の記憶である小竹薮公園をそのまま残し、園への入口の前庭にする。そこから北へ、西の道沿いに幅1 mの歩道を開き、歩く人を車から守る。

地域のなかの敷地　1/10000

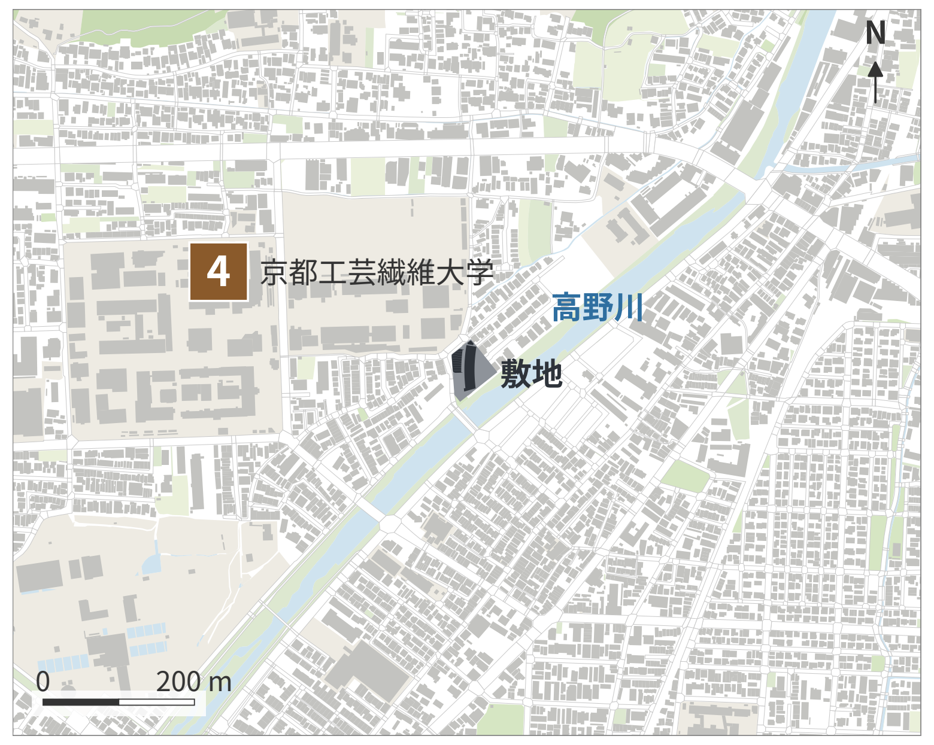
N
4
京都工芸繊維大学
高野川
敷地
0
200 m

出典：国土交通省 Project PLATEAU（京都市 2025）の建物・道路・土地利用から作図

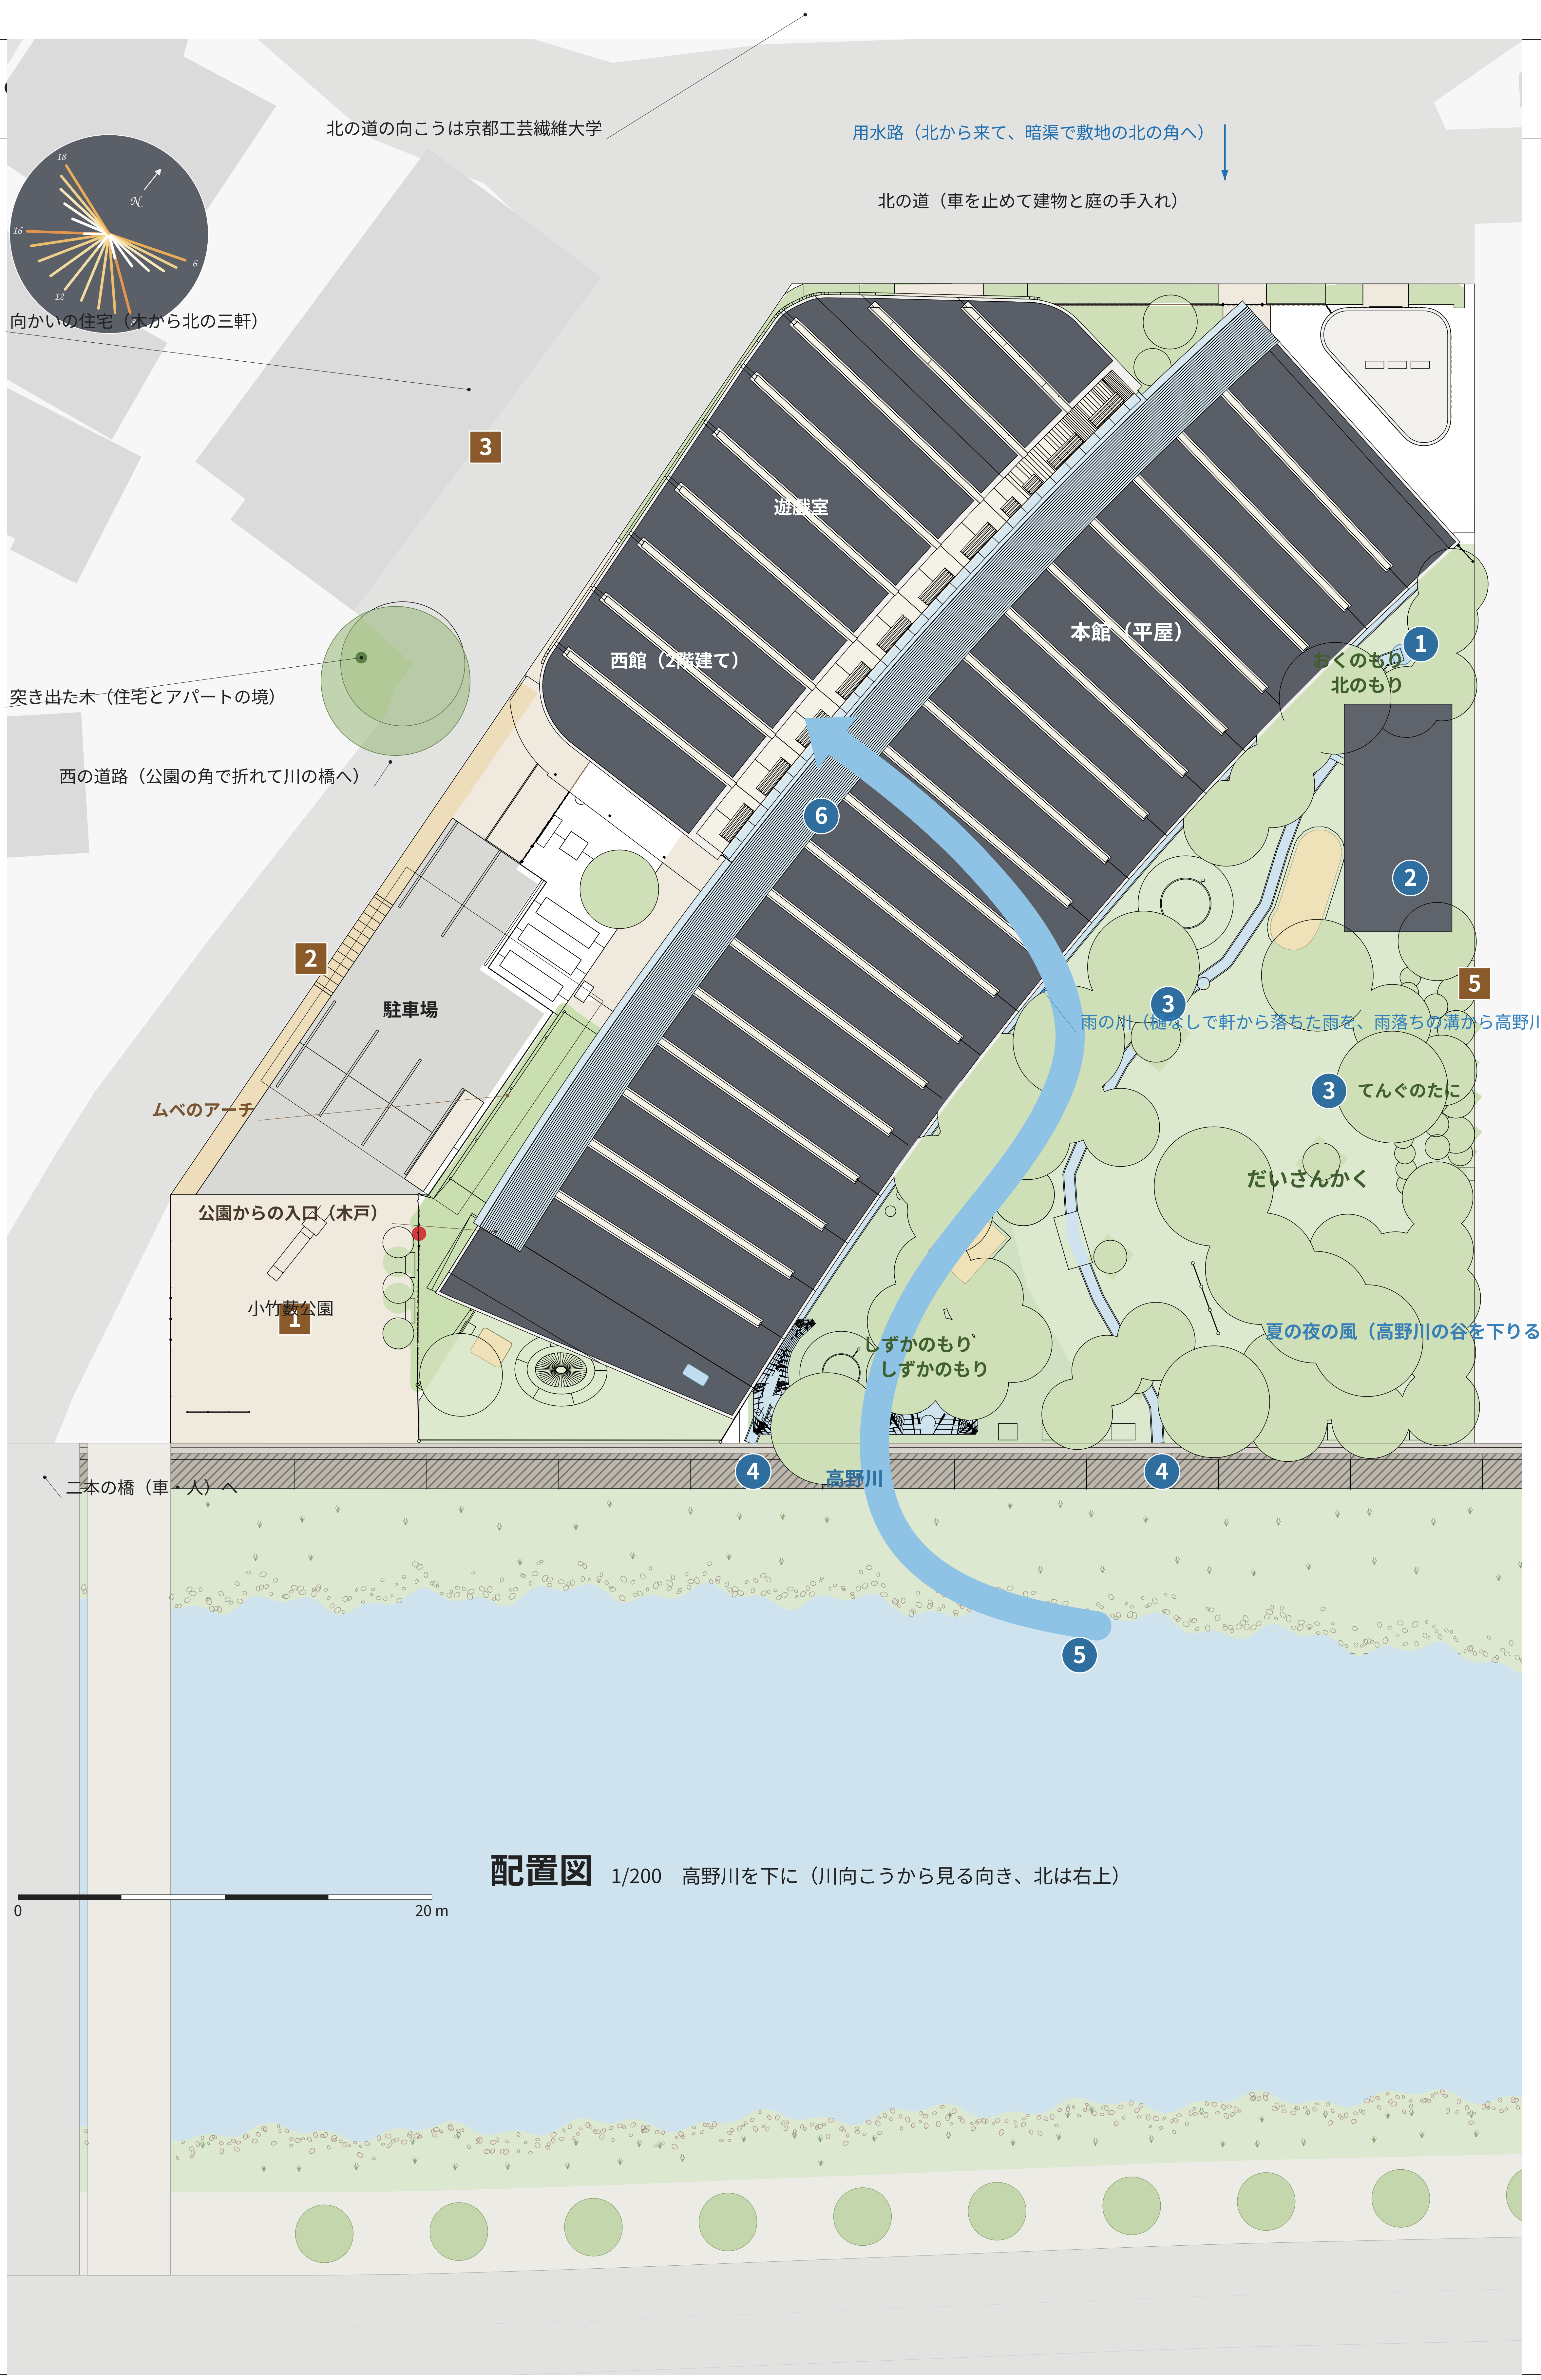
18
16
12
6
N
北の道の向こうは京都工芸繊維大学
用水路（北から来て、暗渠で敷地の北の角へ）
北の道（車を止めて建物と庭の手入れ）
向かいの住宅（木から北の三軒）
3
遊戯室
本館（平屋）
西館（2階建て）
おくのもり
北のもり
①
突き出た木（住宅とアパートの境）
西の道路（公園の角で折れて川の橋へ）
⑥
②
2
駐車場
③
5
雨の川（樋なしで軒から落ちた雨を、雨落ちの溝から高野川へ）
③ てんぐのたに
ムベのアーチ
だいさんかく
公園からの入口（木戸）
小竹薮公園
1
夏の夜の風（高野川の谷を下りる風）
しずかのもり
しずかのもり
④
高野川
④
二本の橋（車・人）へ
⑤
0
20 m

配置図　1/200　高野川を下に（川向こうから見る向き、北は右上）

松ヶ崎の用水ネットワーク

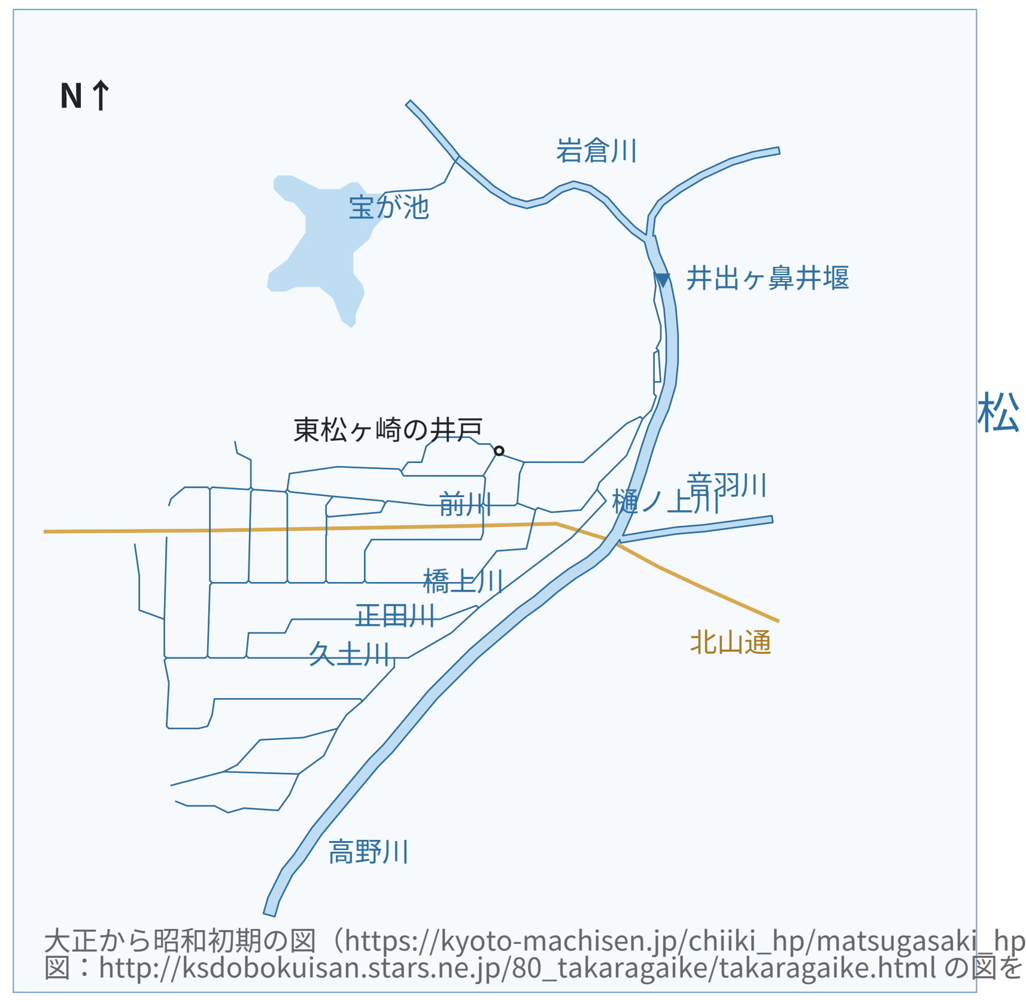
N
岩倉川
宝が池
井出ヶ鼻井堰
東松ヶ崎の井戸
前川
樋ノ上川
音羽川
橋上川
正田川
久土川
北山通
高野川

大正から昭和初期の図（https://kyoto-machisen.jp/chiiki_hp/matsugasaki_hp/history/history.htm）
図：http://ksdobokuisan.stars.ne.jp/80_takaragaike/takaragaike.html の図をなぞって描き直し

松ヶ崎の用水ネットワーク

敷地

① 用水を借りる

井出ヶ鼻井堰に端を発する松ヶ崎の用水ネットワークから、水を借り、園庭の小川にする。

大正から昭和初期の図（https://kyoto-machisen.jp/chiiki_hp/matsugasaki_hp/history/history.h

② 野菜くずコンポスト

野菜くずや落ち葉をこどもたちの手で土に還す。発酵する暖かい土とミミズに驚く。野菜を育てる。命の循環を知る。

5 東の隣家への配慮

東の隣家との境は1 m下げ（セットバック）、園庭の小屋と植樹で視線と音をやわらげる。

⑤ 風の道

夏の夜、高野川の谷を下りてくる涼しい風を、縁側の床下から越屋根へ抜く。床下に冷えをためて、昼の冷房を抑える。

③ 高野川と比叡にみたてる

日本文化が育ててきた「みたて」。園内の小川と築山を高野川と比叡にみたてる。それを超えて視線を遠くにすると、高野川を超えて比叡の山。

④ 水の行方を見る

小川は暗渠に隠さず高野川に注ぐ。屋根に降った雨は、雨落ちに落ち、雨水浸透側溝と雨庭を経て、溢れは高野川に。

建築設計実習 II — I　2026.11.05　木田

［割付の注記］フォーカス：周囲の自然環境との関係と地域環境への配慮。配置図の上に夏の夜の風・比叡への視線　／　目に入る順：タイトルと趣旨 → 真ん中の配置図 → 左右の箱（青＝自然環境、茶＝地域）→ 用水のネットワーク・地域のなかの敷地

松ヶ崎こども園　2ゾーニングと動線・環境

ゾーニング　1/200　使う人ごとの色、セキュリティの内と外、園庭と一体（配置図と同じ向き、高野川を下に）

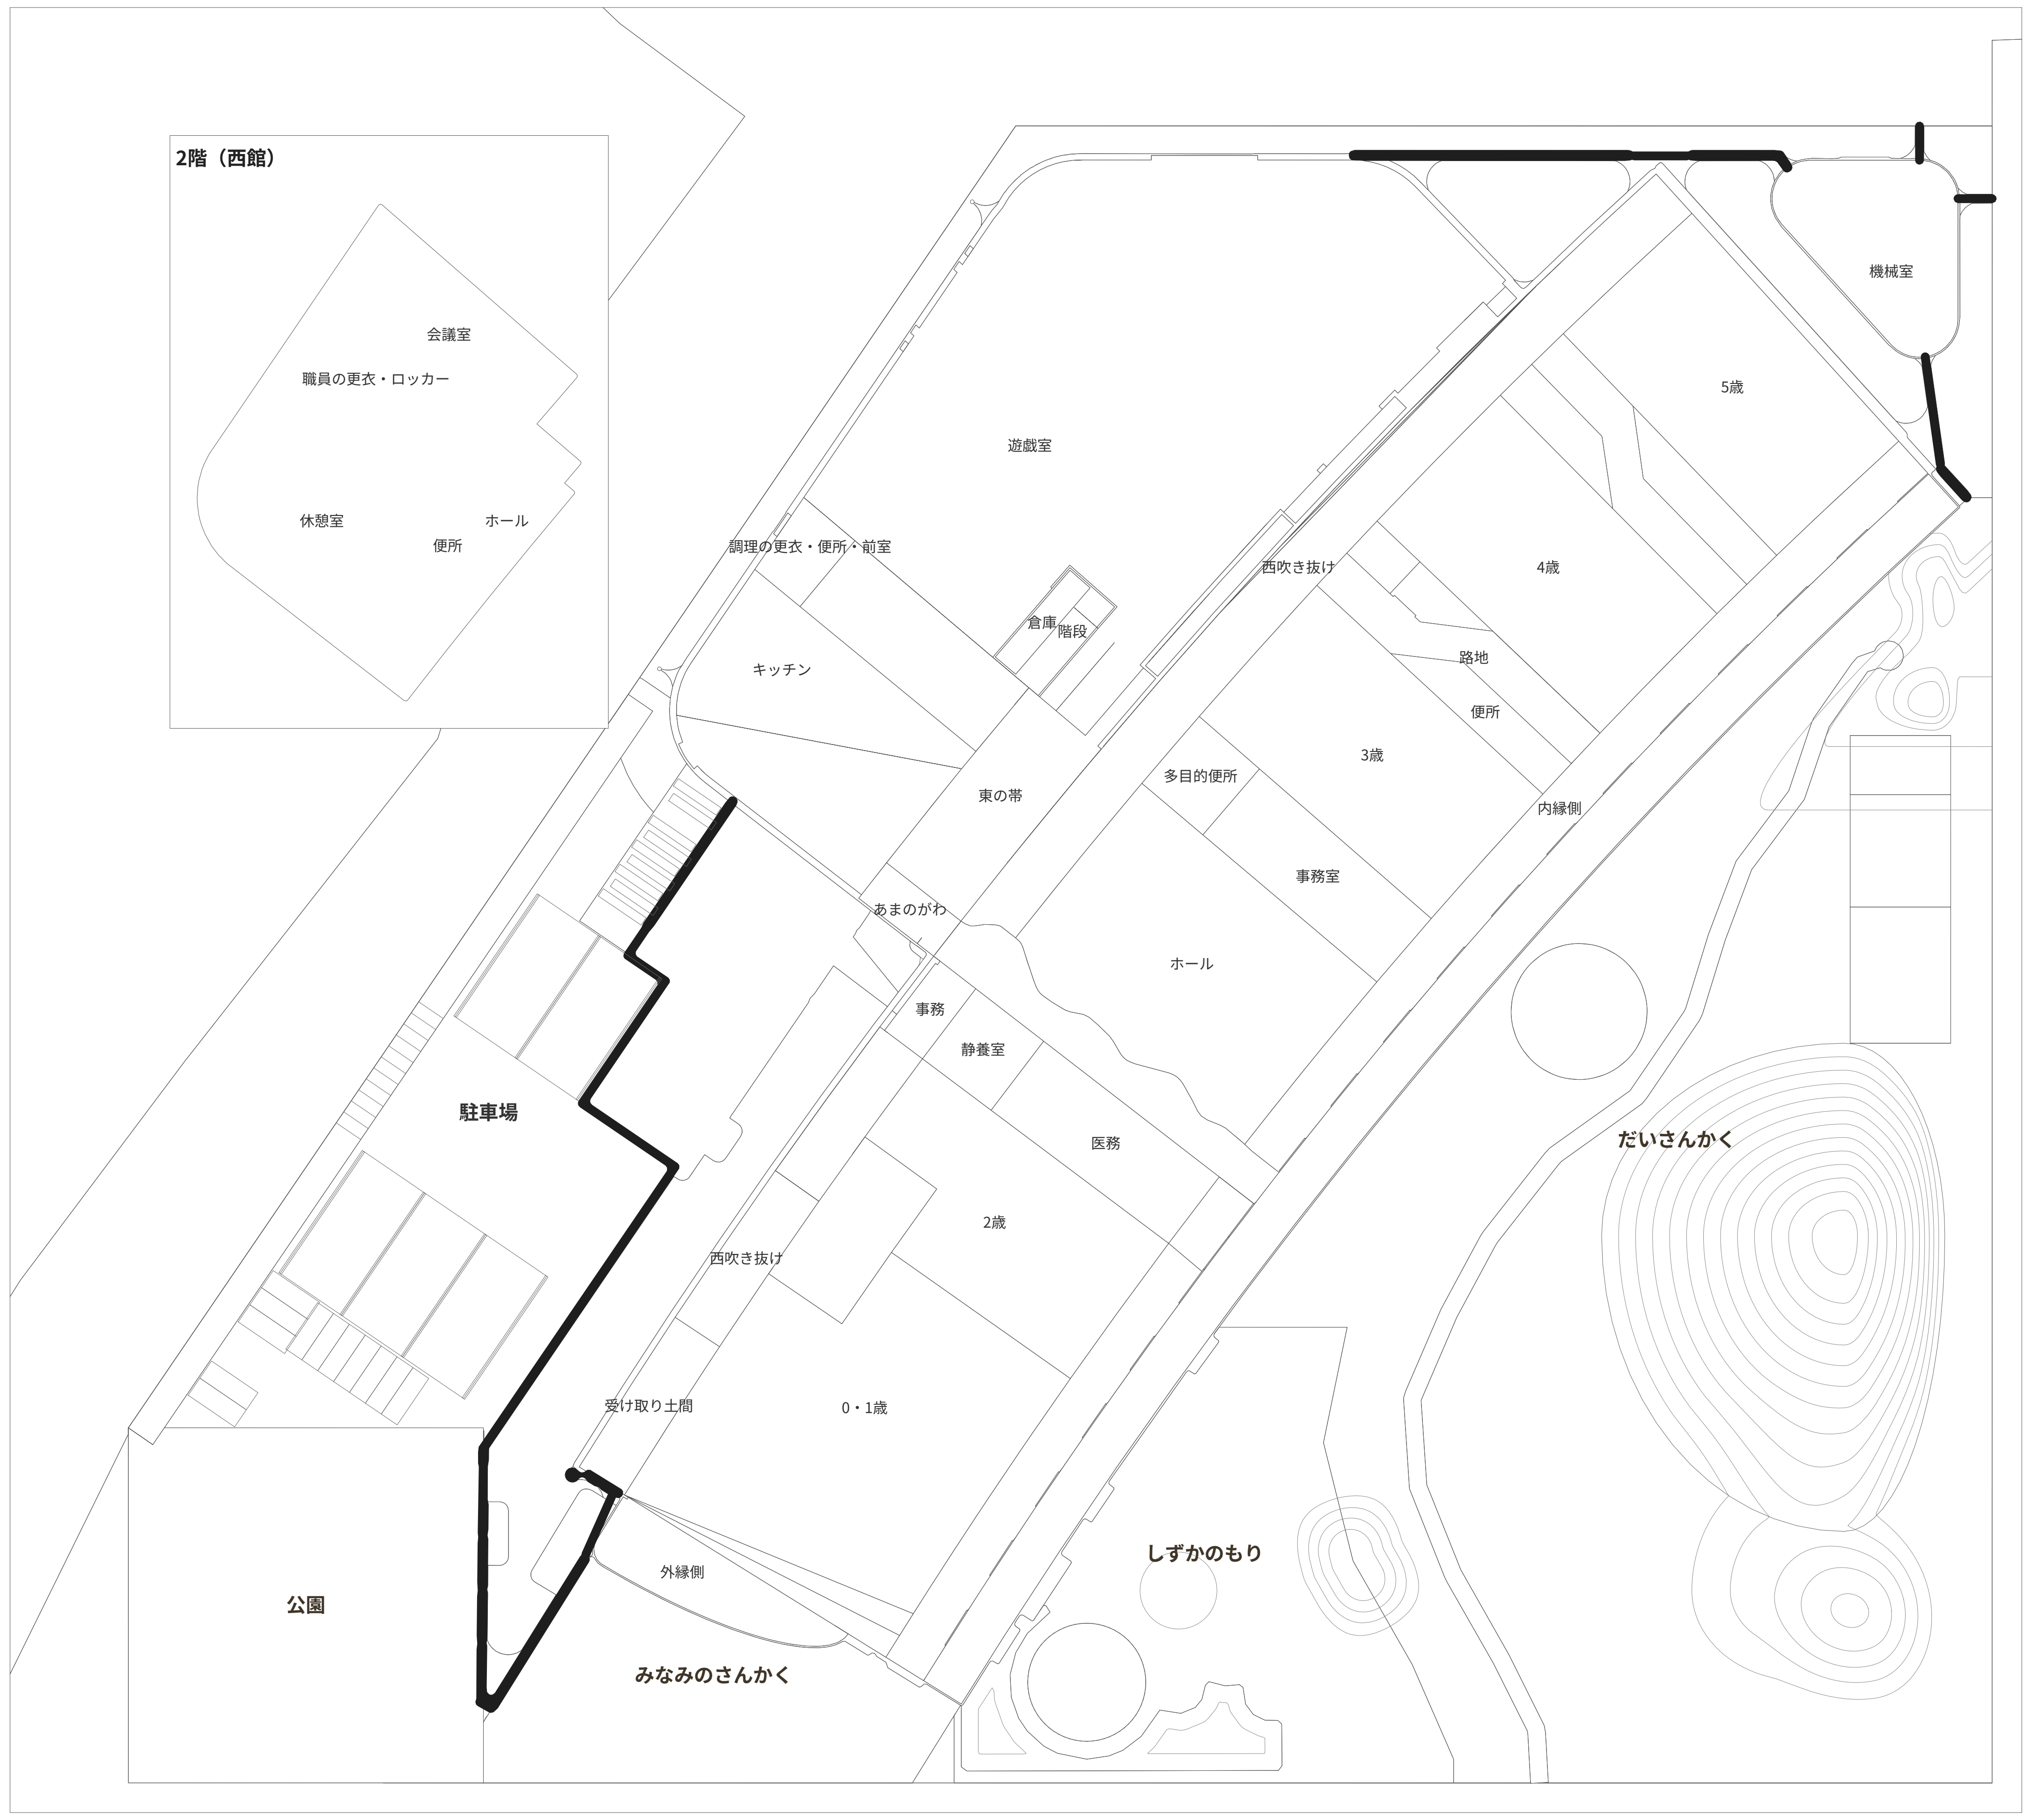
2階（西館）
会議室
職員の更衣・ロッカー
休憩室
ホール
便所
遊戯室
調理の更衣・便所・前室
倉庫
階段
キッチン
東の帯
あまのがわ
機械室
5歳
西吹き抜け
4歳
路地
便所
3歳
多目的便所
内縁側
事務室
ホール
事務
静養室
医務
駐車場
2歳
西吹き抜け
受け取り土間
0・1歳
外縁側
公園
みなみのさんかく
しずかのもり
だいさんかく

☐ 0〜2歳　☐ 3〜5歳　☐ みんなの場所　☐ 大人　☐ 調理　☐ トイレ　☐ 倉庫

☐ セキュリティ外（歩道・ひろば・搬入路）　☐ セキュリティ内の外構（北の坪庭・読書の庭）　☐ 土足（木戸の内の小径・ムベの下、受け取り土間・あまのがわ・外縁側）

☐ 乳児の園庭（みなみのさんかく）　☐ しずかのもり（両方）　☐ だいさんかく（3〜5歳）　☐ 駐車場・駐輪場　☐ 水遊び場・雨庭　☐ 公園

―― 塀・柵・木戸・生垣（セキュリティの線）　― 等高線 0.2 m（園庭の地形・築山）

樹木　1/400　園児が目にする木。塗りは常緑・落葉、印は香り・花・紅葉・実・ちくちく

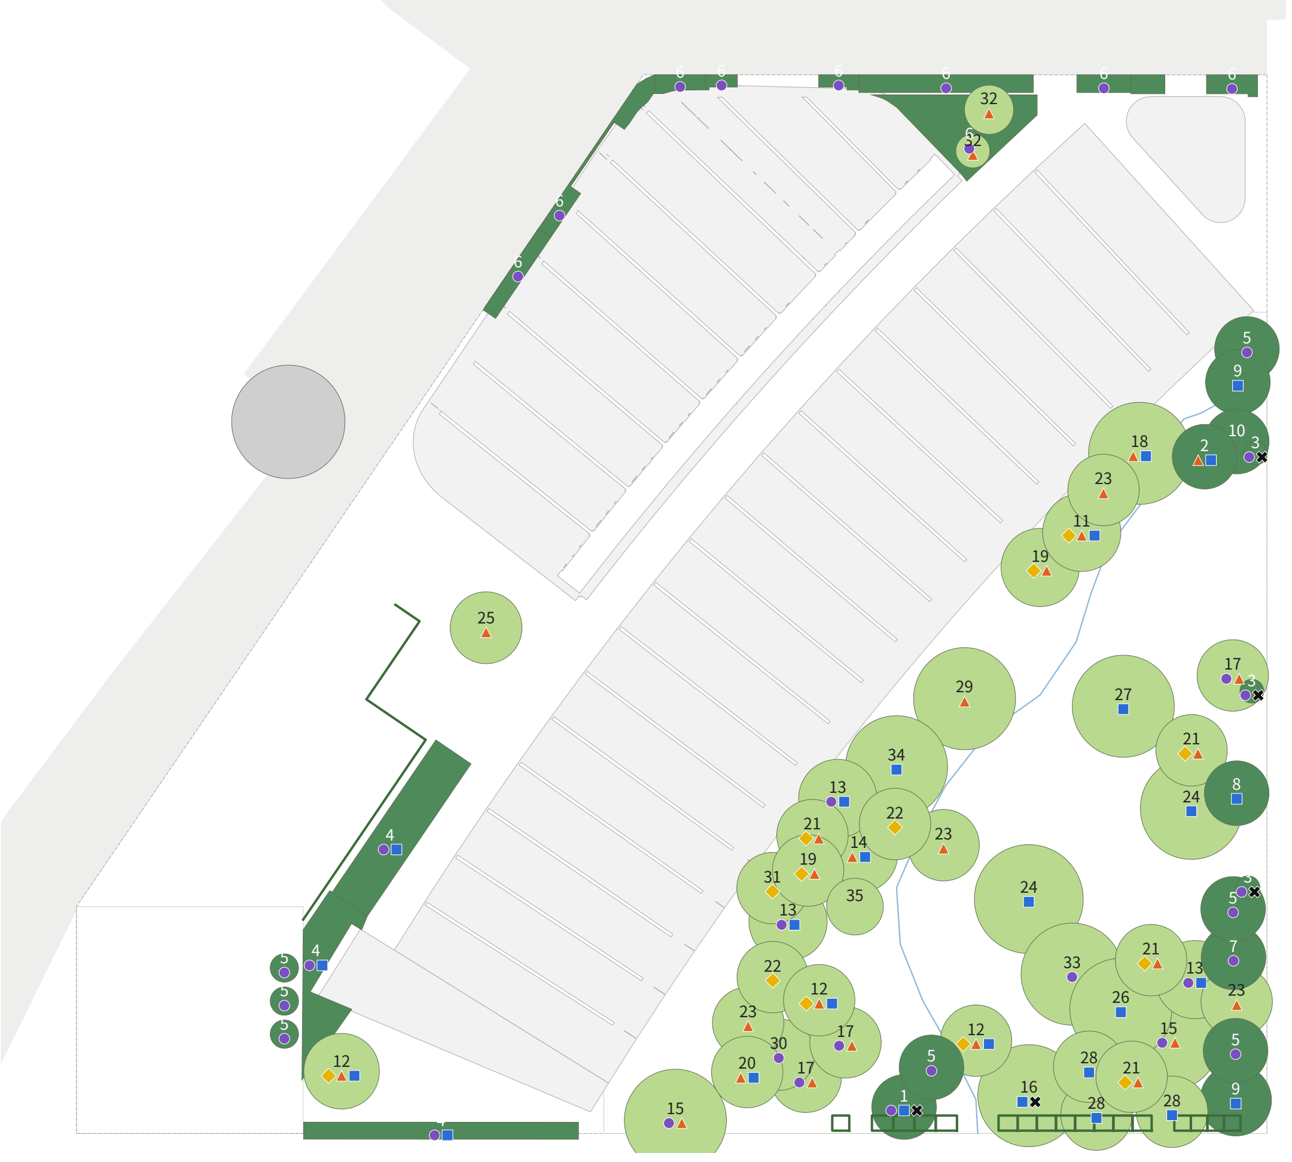

🟩 常緑
▨ 落葉
― 生垣（線）
● 香り
◆ 花
▲ 紅葉・黄葉
■ 実
✖ ちくちく（とげ・痛い葉）

🟩 1　ユズ ●■✖
🟩 2　ナンテン ▲■
🟩 3　ヒイラギ（3） ●✖
🟩 4　ムベ（3） ●■
🟩 5　キンモクセイ（7） ●
🟩 6　ギンモクセイ（9） ●
🟩 7　クスノキ ●
🟩 8　シラカシ ■
🟩 9　ソヨゴ（2） ■
🟩 10　ホウライチク
▨ 11　ジューンベリー ◆▲■
▨ 12　ヤマボウシ（3） ◆▲■
▨ 13　ウメ（3） ●■
▨ 14　カキ ▲■
▨ 15　カツラ（2） ●▲
▨ 16　クリ ■✖
▨ 17　クロモジ（3） ●▲
▨ 18　コナラ ▲■
▨ 19　サルスベリ（2） ◆▲
▨ 20　ナツハゼ ▲■
▨ 21　ヤマザクラ（4） ◆▲
▨ 22　アオダモ（2） ◆
▨ 23　イロハモミジ（4） ▲
▨ 24　エノキ（2） ■
▨ 25　オオモミジ ▲
▨ 26　カシワ ■
▨ 27　クヌギ ■
▨ 28　クワ（3） ■
▨ 29　ケヤキ ▲
▨ 30　コブシ ●
▨ 31　ハナモモ ◆
▨ 32　ベニシダレ（2） ▲
▨ 33　ホオノキ ●
▨ 34　ムクノキ ■
▨ 35　ヤナギ（柳の家）

一日の帯：1/700の小さな配置（西の道路から高野川まで）。その時間に使う所だけゾーニングの色、ほかは灰。動線は .ai で

朝（と帰り）

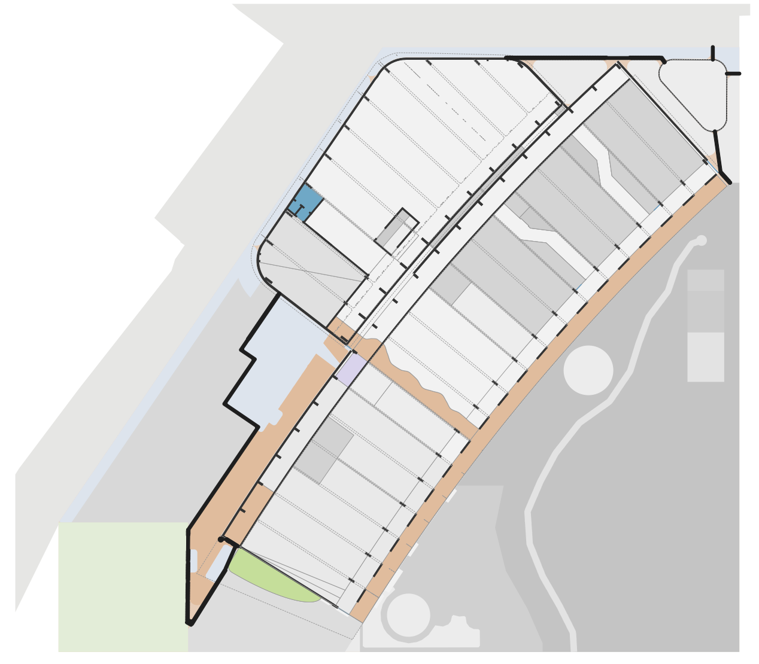

公園の木戸からムベのアーチの下へ。0・1歳は受け取り土間で手渡し、ひろばで見送り、おはようの窓口で挨拶。食材は勝手口で検収。帰りはこの逆

日中

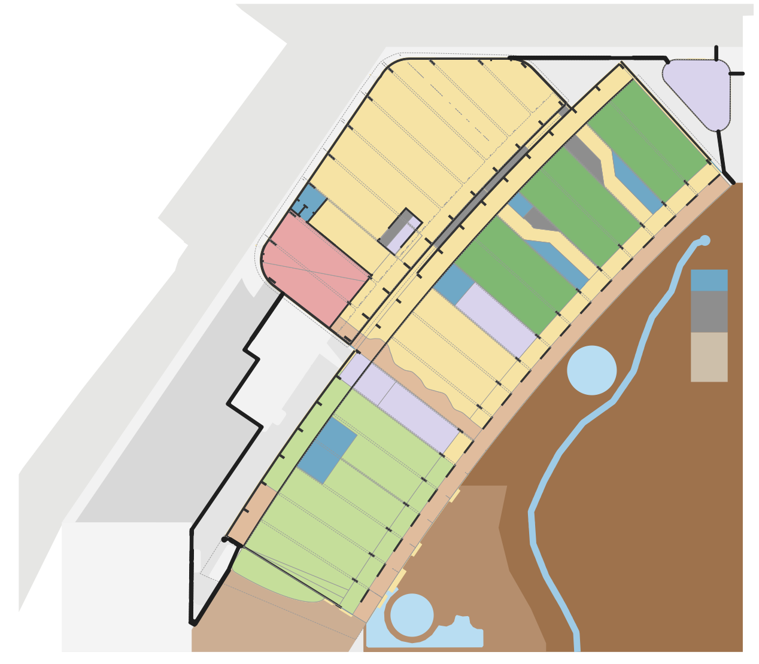

建物の中のすべてと、だいさんかく・しずかのもり・みなみのさんかくで過ごす

食事

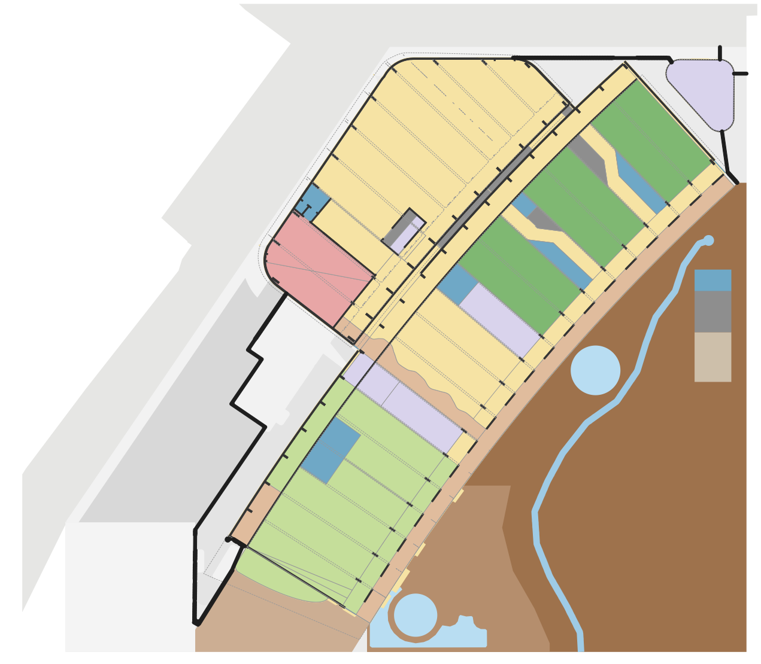

保育室の食卓でクラスごとに食べる。キッチンから配膳口を通って運ぶ

延長保育

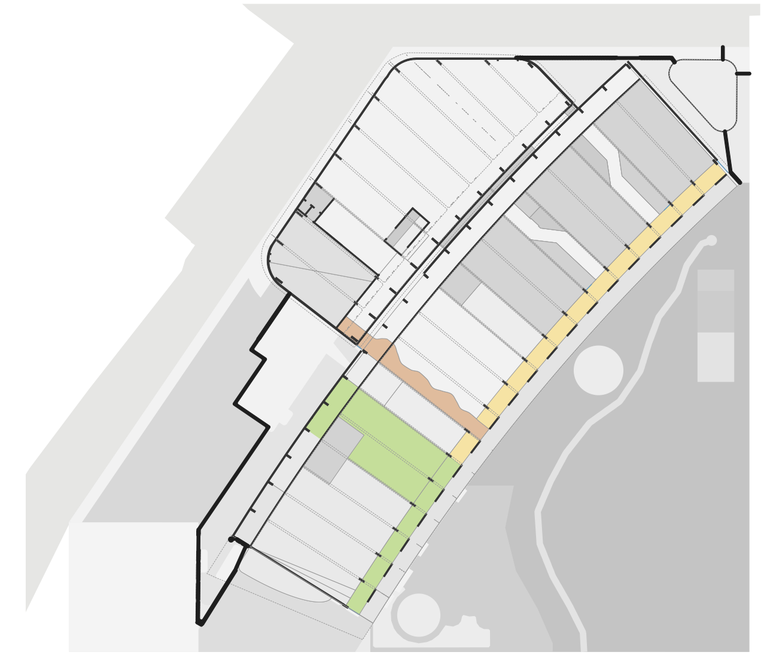

2歳の部屋で迎えを待つ。内縁側・あまのがわ・西の吹き抜けの南だけを使い、ほかは閉じる

教室　3〜5歳　軸測図（レンダリングを待つあいだ）

4歳の保育室

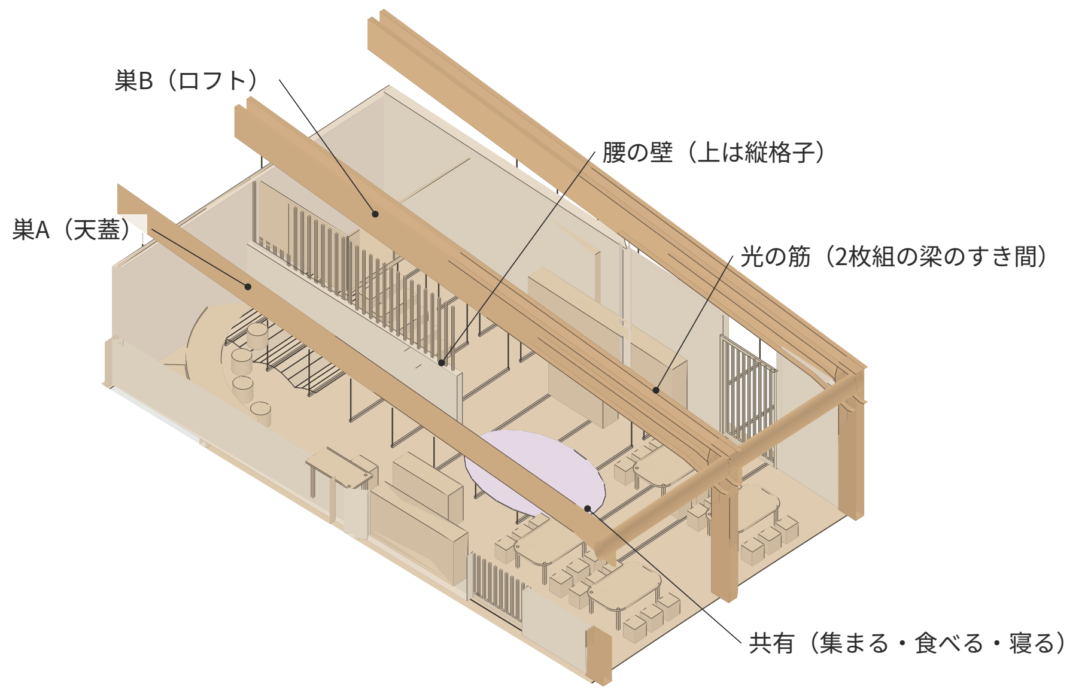
巣B（ロフト）
腰の壁（上は縦格子）
巣A（天蓋）
光の筋（2枚組の梁のすき間）
共有（集まる・食べる・寝る）

教室　0・1歳　軸測図（レンダリングを待つあいだ）

0・1歳の保育室

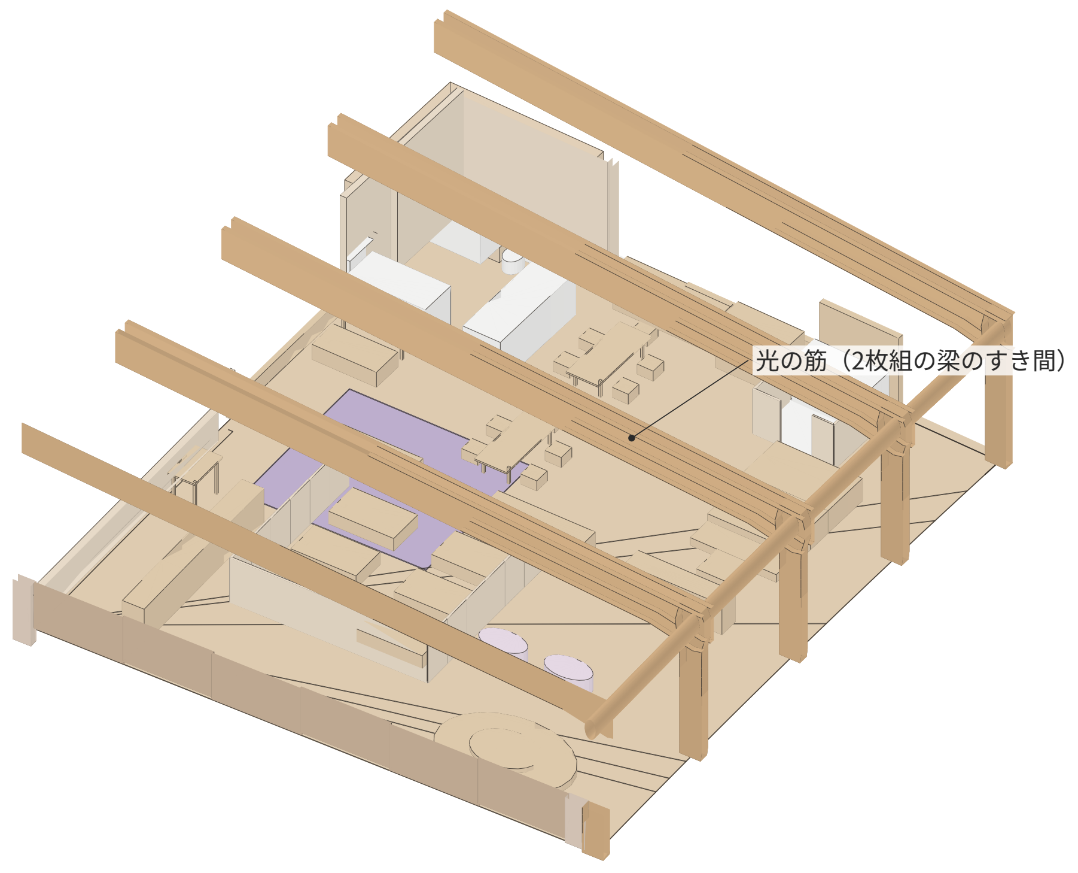
光の筋（2枚組の梁のすき間）

教室　2歳　軸測図（レンダリングを待つあいだ）

2歳の保育室

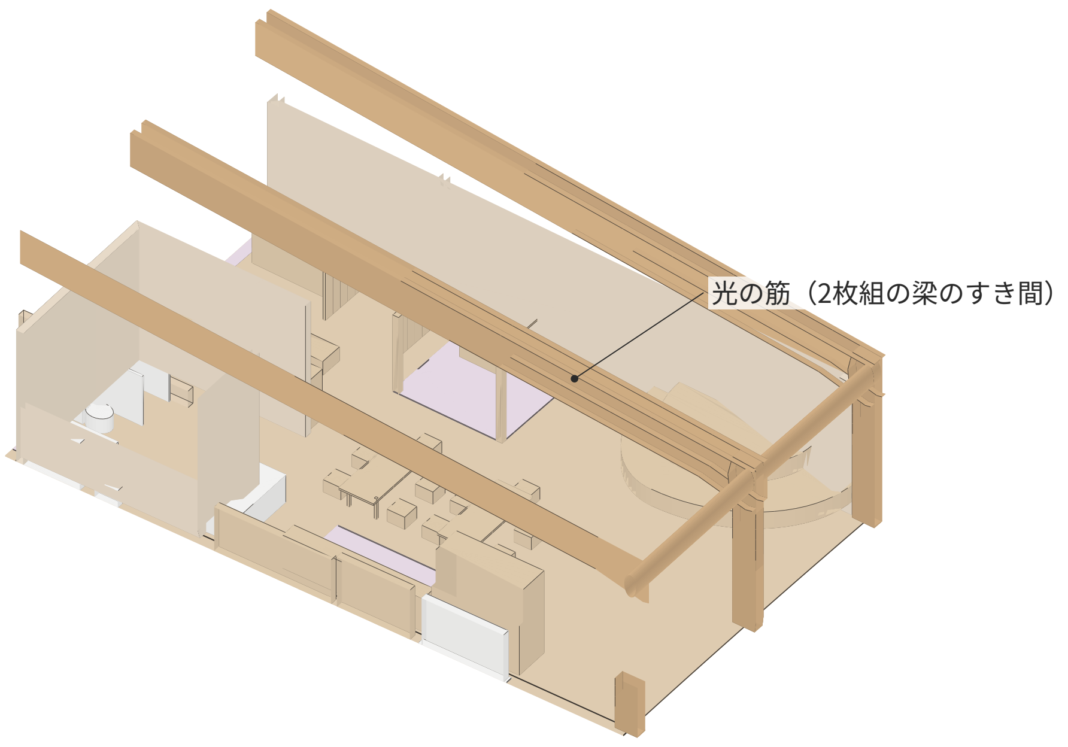
光の筋（2枚組の梁のすき間）

居場所　読書　軸測図（レンダリングを待つあいだ）

絵本の通りと本の奥

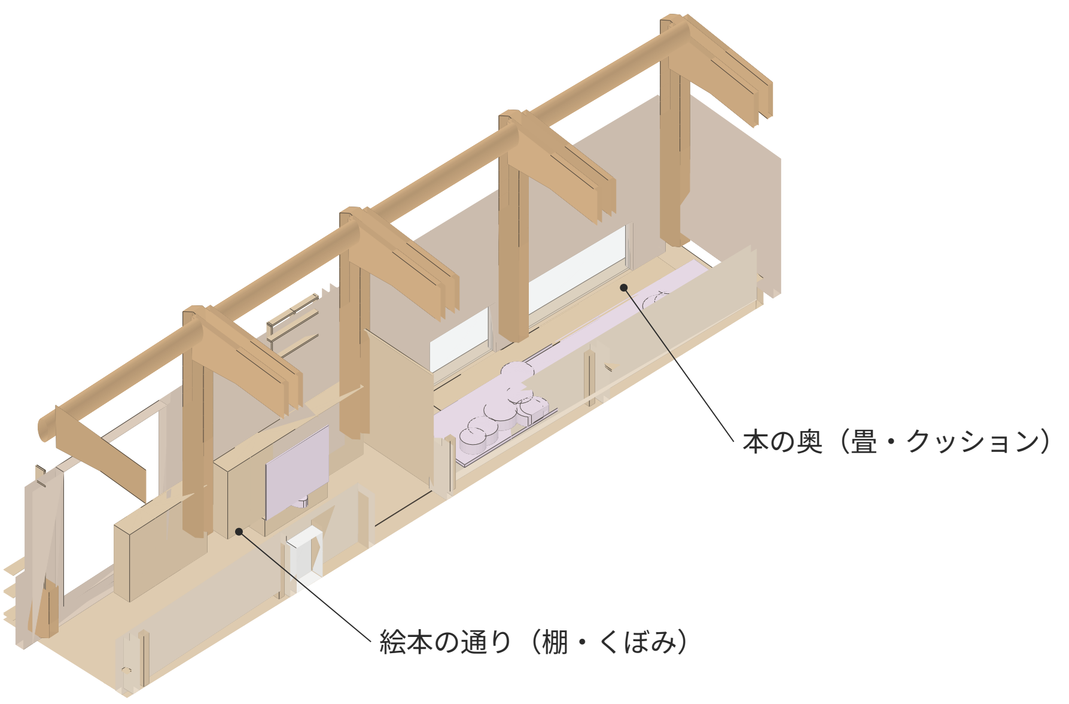
本の奥（畳・クッション）
絵本の通り（棚・くぼみ）

居場所　遊戯室の箱　軸測図（レンダリングを待つあいだ）

遊戯室の箱（西の壁のひだ）

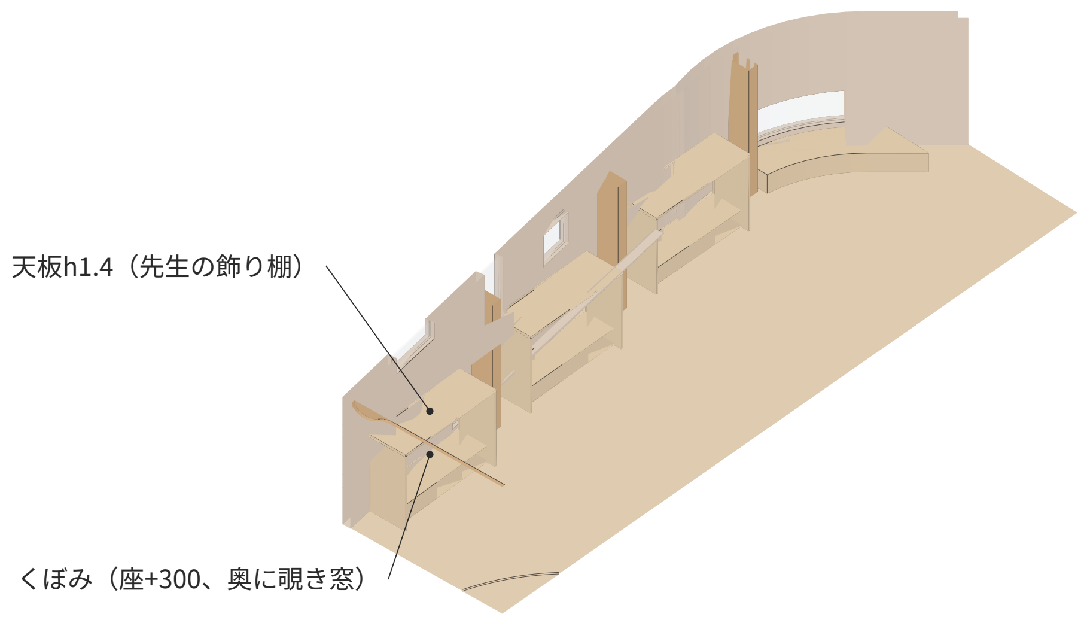
天板h1.4（先生の飾り棚）
くぼみ（座+300、奥に覗き窓）

遊戯室　平面

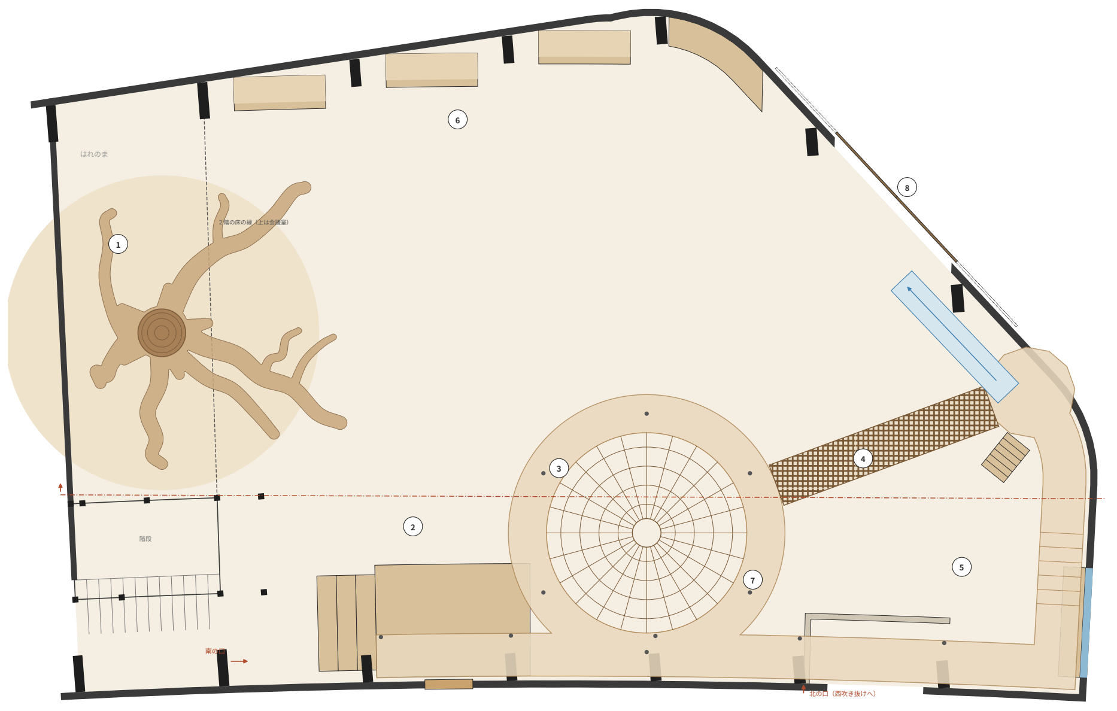
はれのま
2階の床の縁（上は会議室）
1
2
3
4
5
6
7
8
階段
南の口
北の口（西吹き抜けへ）

建築設計実習 II — I　2026.11.05　木田

［割付の注記］フォーカス：左にゾーニング（園庭と一体、使う人・土足・トイレ）と樹木。右の上に一日の帯（朝と帰り・日中・食事・延長保育）、下に教室・居場所・遊戯室　／　目に入る順：ゾーニング→一日の帯→教室・居場所・遊戯室→樹木

平面図　1階　FL+1500 で切断　1/100

松ヶ崎こども園 3平面図　1階

高野川を下に（配置図と同じ向き）、一点鎖線は敷地の境、二点鎖線は切断より上にある物（屋根の外形、越屋根、2階の床の縁など）、周りの道・建物は細い線

C
D
A
B
N
30,194　西館の南北の全長（東の線で）　架構 8〜18・10 スパン
1,000　西の道路境界まで（西の外壁は後退の1mの線の上）
14,235　西館の東西の幅（架構 15 の線で、外壁の外面から外面）
R205,000（W通り）
1,156　北東の隣地境界まで（機械室）
遊戯室
266.1 m²
調理の更衣・便所・前室
6.3 m²
倉庫
3.8 m²
階段
4.4 m²
上
キッチン
59.4 m²
1,600　2階の床の東の縁（東の線から）
東の帯
26.0 m²
倉庫
4.6 m²
倉庫
4.8 m²
背骨（W通り）の弦は約56.8 m・矢高は約2.0 m（二点鎖線）
路地
15.1 m²
倉庫
6.5 m²
5歳
60.6 m²
便所
8.6 m²
R193,000（E通り）
2,081　北東の隣地境界まで（本館）
4歳
60.3 m²
便所
3.0 m²
倉庫
3.5 m²
路地
15.2 m²
便所
8.6 m²
3歳
60.3 m²
多目的便所
8.0 m²
事務室
22.2 m²
西吹き抜け＝越屋根の幅
1,600
西吹き抜け
63.3 m²
ホール
75.2 m²
部屋の帯（保育室・ホールなど）
10,400
15,000　計（W通り〜東の軒先、どの架構でも同じ）
内縁側
1,500
外縁側
1,500
〜53,663　E通り（R193,000）の上の長さ、架構1〜20
〜57,000　W通り（R205,000、背骨）の上の長さ、架構1〜20（19× 3,000、スパンもW通りの上）
〜3,000
事務
4.9 m²
静養室
8.6 m²
医務
21.6 m²
あまのがわ（W通りの上、架構8から）
2,200
西吹き抜け
11.4 m²
2歳
60.0 m²
受け取り土間
11.2 m²
0・1歳
120.5 m²
4,200
南の軒の出（架構1から、東の軒先→西の角）
4,329　高野川の側の境界まで（避難の帯）
1,800　軒の出
R190,000（東の軒先）
2,824（E通りの上）
0.838°
W
E
1
2
3
4
5
6
7
8
9
10
11
12
13
14
15
16
17
18
19
20
0
5 m

部屋の色

- 🟩 0・1歳〜5歳
- 🟨 こどものみんなの場所（遊戯室・はれのま）
- ▨ 通り・つなぐ場所（はだし）
- ▨ 土足の床
- 🟪 大人の場所
- 🟪 キッチン・調理の更衣
- ▨ 水まわり

建築設計実習Ⅱ－Ⅰ　2026.11.05　木田

［割付の注記］フォーカス：敷地全体の1階の平面図1/100、配置図と同じ向き。2階（西館）は4枚目　／　目に入る順：平面図→色の凡例・面積

平面図　2階（西館）　2FL+1000 で切断　1/100

松ヶ崎こども園　4平面図　2階

高野川を下に（配置図と同じ向き）。1階の平面図と同じ位置・同じ縮尺（重ねると上下が合う）。西館の外（東館の屋根・園庭・周り）は上から見た見えがかり。二点鎖線は切断より上にある物（西館の屋根の外形など）

吹抜（遊戯室）
会議室
29.8 m²
職員の更衣・
ロッカー
12.9 m²
休憩室
60.4 m²
ホール
18.8 m²
便所
2.9 m²
下
12,194　2階の南北（南の妻の外面〜2階の床の北の縁、東の縁で）
11,366　2階の東西（西の外面〜2階の床の東の縁）
N
W
E
1
2
3
4
5
6
7
8
9
10
11
12
13
14
15
16
17
18
19
20
0
5 m

部屋の色

🟩	0・1歳〜5歳
🟨	こどものみんなの場所（遊戯室・はれのま）
▨	通り・つなぐ場所（はだし）
🟫	土足の床
🟪	大人の場所
🟪	キッチン・調理の更衣
🟦	水まわり

建築設計実習 II ー I　2026.11.05　木田

こどもたちの育ち舎　3dm（sodachiya.3dm）から自動で作図　2026-10-31 06:42（atelier ebc45d の次の版の3dm）

［割付の注記］フォーカス：2階（西館）の平面図1/100。1階（3枚目）と紙の上で同じ位置・同じ大きさ（重ねると上下が合う）　／　目に入る順：平面図

松ヶ崎こども園　5立面・景観

園庭の側の立面図

1/100　円弧の中心の方向から弧の真ん中に正対

園庭にひらく　縁側と深い軒が57 m続き、3 mごとの柱とガラス戸の半分が開く。屋根の光の筋が架構を照らし、こどもは縁側から庭へ下りる。

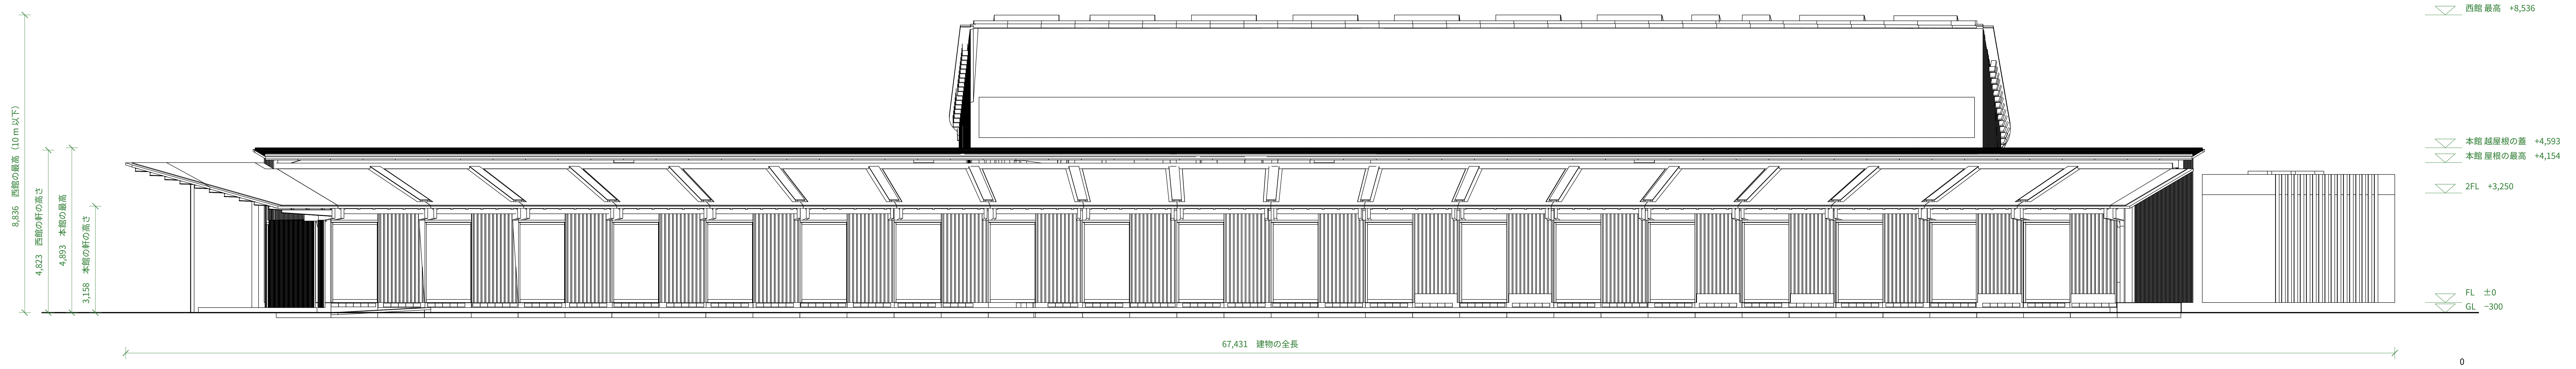
8,836　西館の最高（10 m 以下）
4,823　西館の軒の高さ
4,893　本館の最高
3,158　本館の軒の高さ
西館 最高　+8,536
本館 越屋根の蓋　+4,593
本館 屋根の最高　+4,154
2FL　+3,250
FL　±0
GL　−300
67,431　建物の全長
0

道路の側の立面図

1/100　西の道路から

まちに溶け込み、やさしく守る　杉の大和張りの静かな板の壁。西館は向かいの住宅に向けて1階の高さまで下げ、窓は小さく面ごとのリズムで。道からは中が見えすぎず、園を包む。

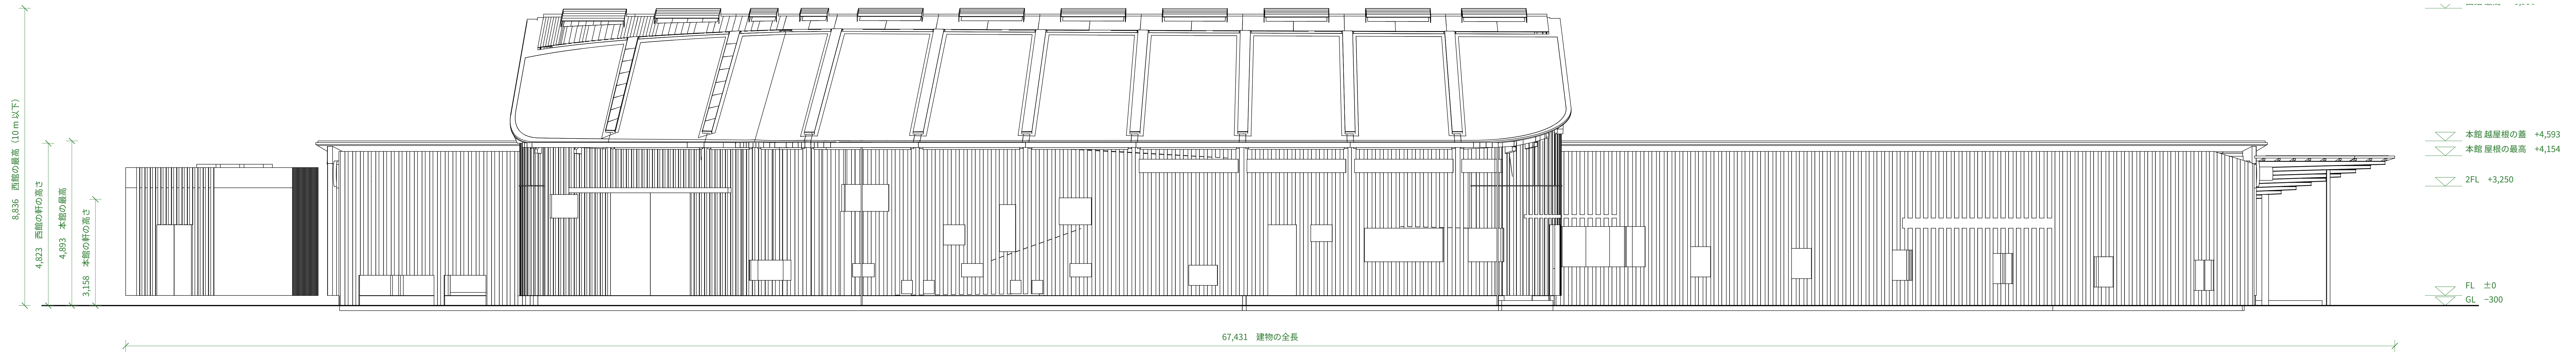
8,836　西館の最高（10 m 以下）
4,823　西館の軒の高さ
4,893　本館の最高
3,158　本館の軒の高さ
本館 越屋根の蓋　+4,593
本館 屋根の最高　+4,154
2FL　+3,250
FL　±0
GL　−300
67,431　建物の全長

透視図（A4）　公園の角から西の道を見る

目の高さ1.5 m、左に向かいの住宅、右に西館の低い軒

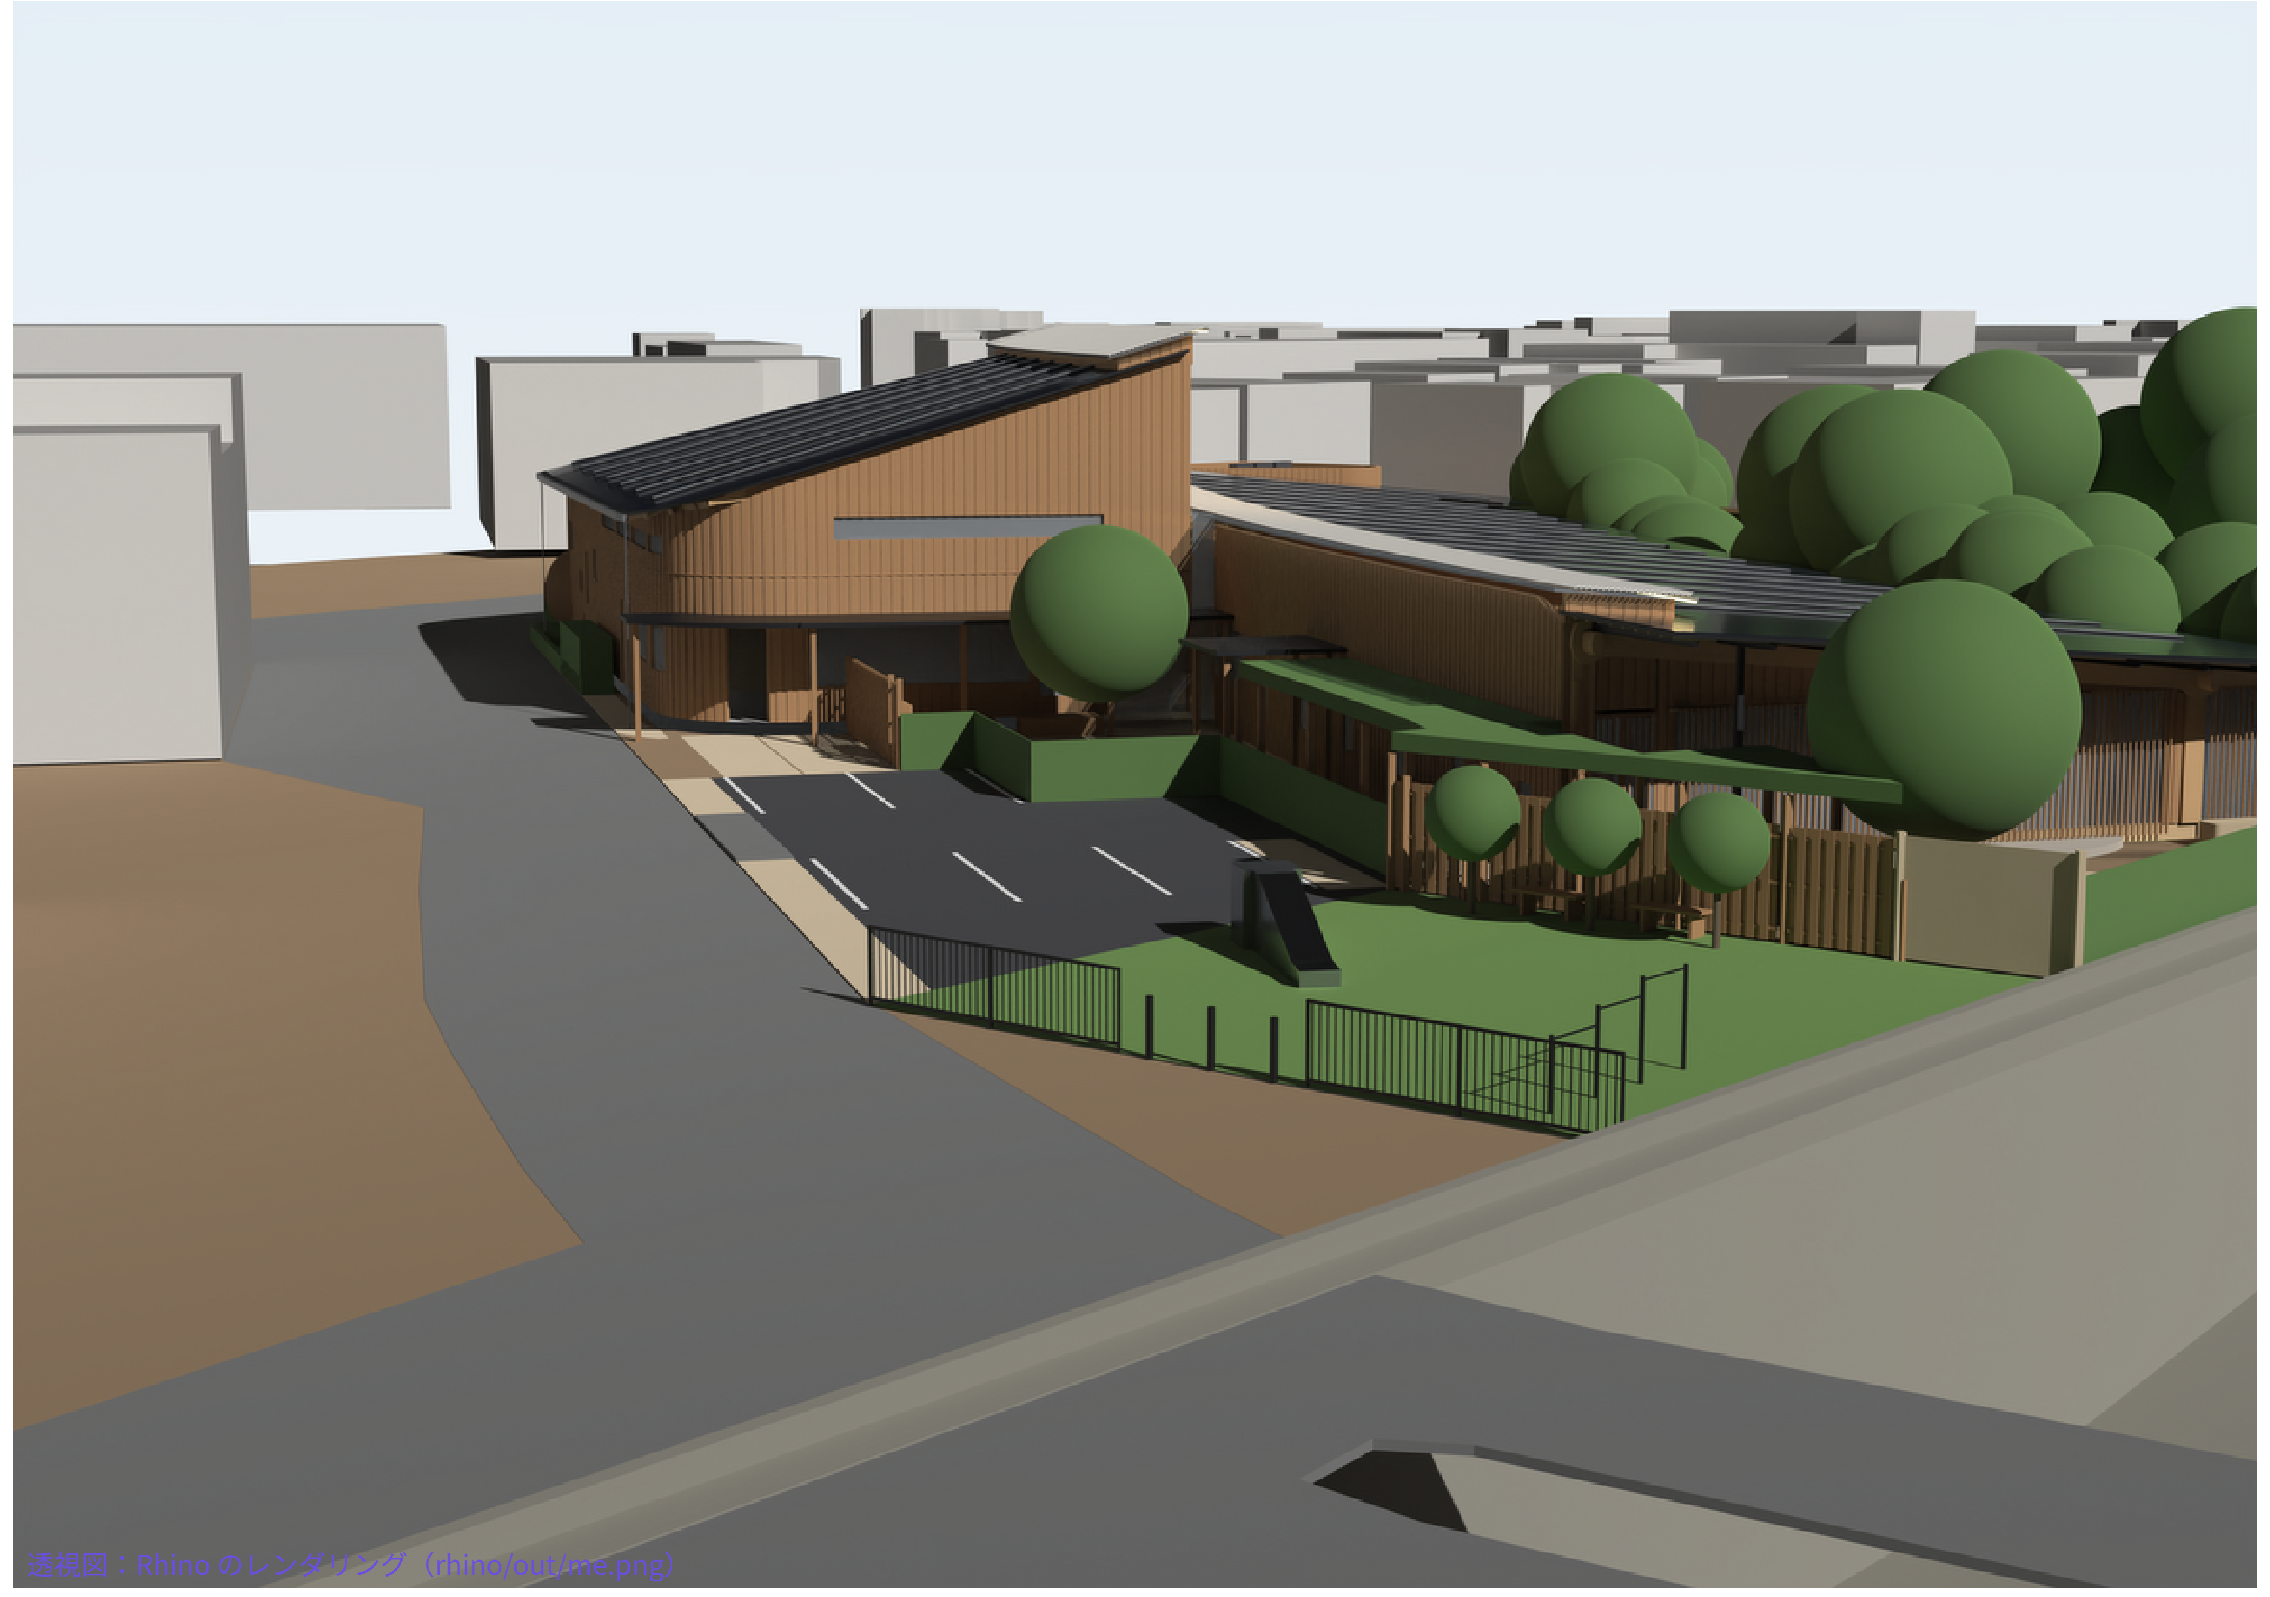
透視図：Rhino のレンダリング（rhino/out/me.png）

沿川の景観　昼

高野川の向こう岸の歩道から、目の高さ1.5 m

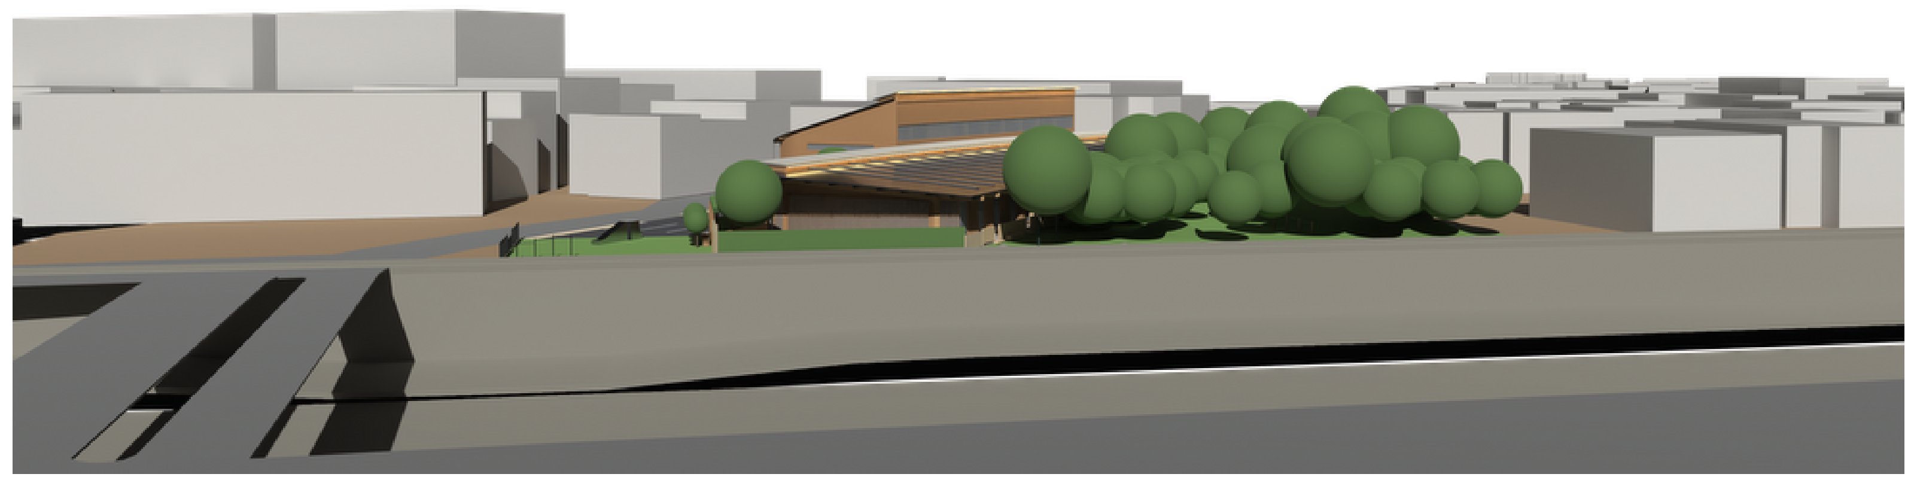

沿川の景観　夜

高野川の向こう岸の歩道から、目の高さ1.5 m　本館と西館の越屋根の光

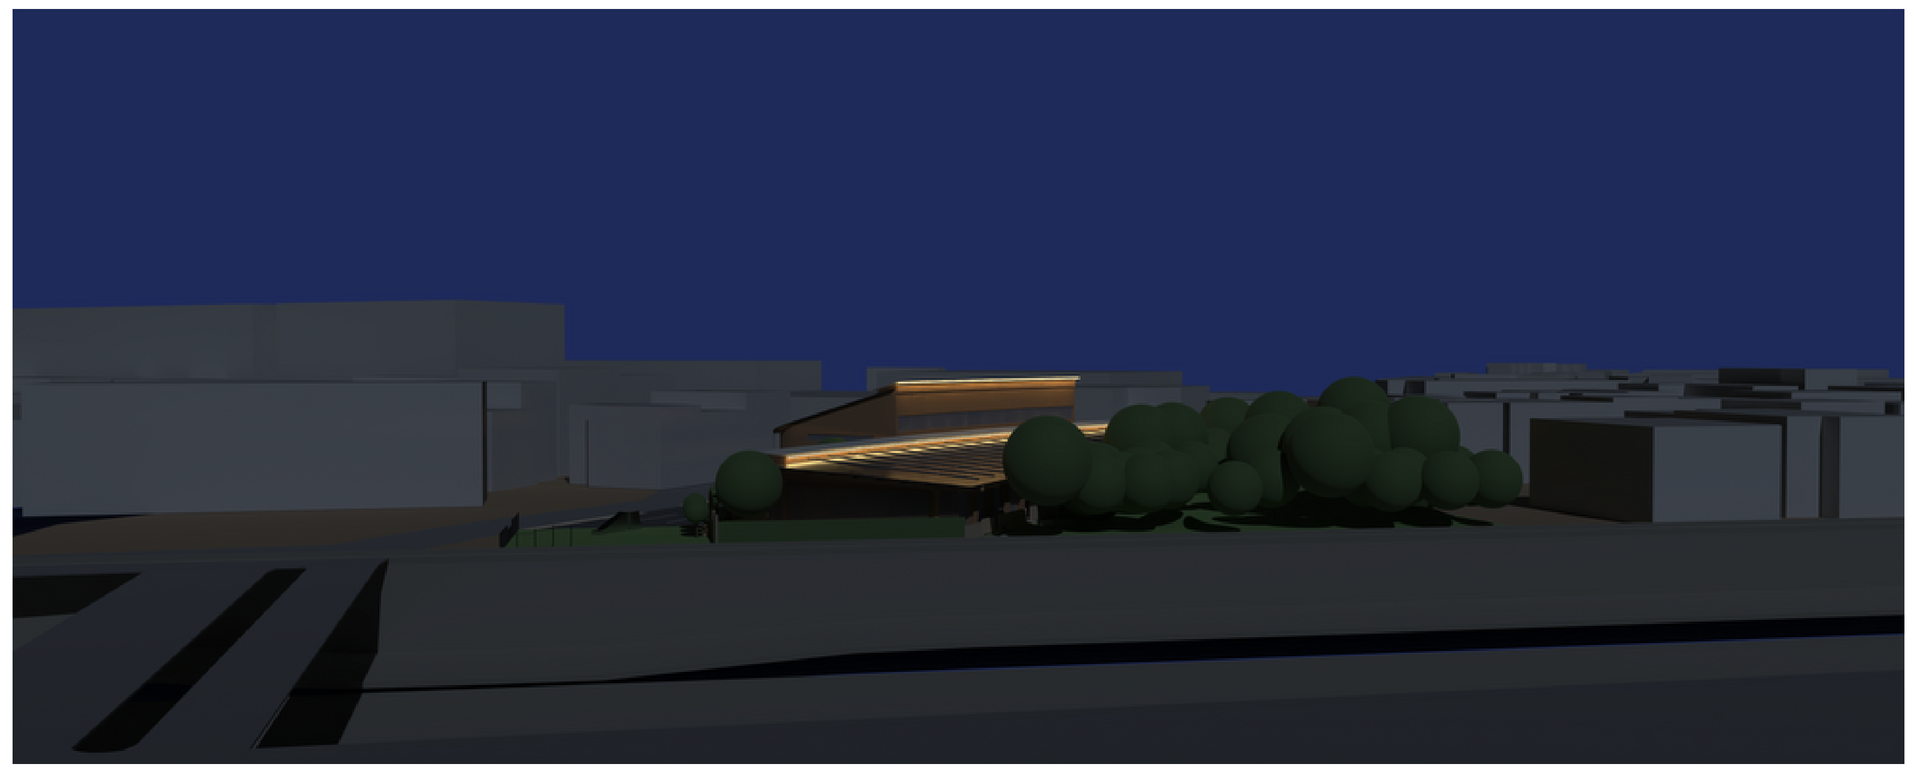

景観の法規

用途地域：第一種低層住居専用地域（都市計画法）。最高の高さは西館の棟で約9.0 m（GLから）。

風致地区（京都市風致地区条例）：高野川特別修景地域（同条例第6条第1項による指定、許可基準は基準告示第7条）。右岸の基準：既存の樹木を保全する／河川に面する部分に植栽帯を設ける／建築物は原則として河川の側に勾配のある下屋を設けた和風の外観とする。対応：川の側に園庭の林と生垣、南に深い軒（下屋）、深い軒と縁側・杉の大和張りの板壁・ゆるい勾配の屋根。

屋根の太陽光：同基準第7条第1項(80)で屋根に太陽光発電装置を原則として設けない。屋根材と一体の太陽電池で、黒い金属の屋根と見分けがつかず周辺の風致に不調和でない（同(80)の例外）。こども園で、同第7条第2項の例外（建築物全体のデザイン・公益上やむを得ない学校等の施設）にもあたるとする。

遠景デザイン保全区域（京都市眺望景観創生条例）：外壁・屋根に禁止色を用いない、山並みと調和する。対応：黒い金属の屋根、木の色のまま。

素材と色

- 🟫 木の柱・梁（木の色のまま）
- 🟫 杉の大和張り（銀鼠に枯れる）
- ■ 黒い金属の屋根（太陽光一体）
- □ 越屋根のガラス・縁側の白
- 🟩 生垣と園庭の緑

敷地が高野川の右岸にあるという読みは要確認（決定事項：たたき台の読み）

建築設計実習Ⅱ—Ⅰ　2026.11.05　木田

［割付の注記］フォーカス：建物に正対する二つの立面（園庭の側・道路の側）で、伸びやかな梁と縁側、西館の立ち上がり。下の段に外から見た姿：目の高さの透視図（公園の角から西の道、お向かいさんとの関係）と、川の向こう岸から見た沿川の景観（昼・夜、透視図）　／　目に入る順：園庭の側・道路の側の立面図→透視図（A4）・沿川の景観（昼・夜）→景観の法規・素材と色

松ヶ崎こども園　6断面・構造

縦断面図A

1/100　保育室の中ほどの弧で切って展開、西を見る（左が南の高野川）

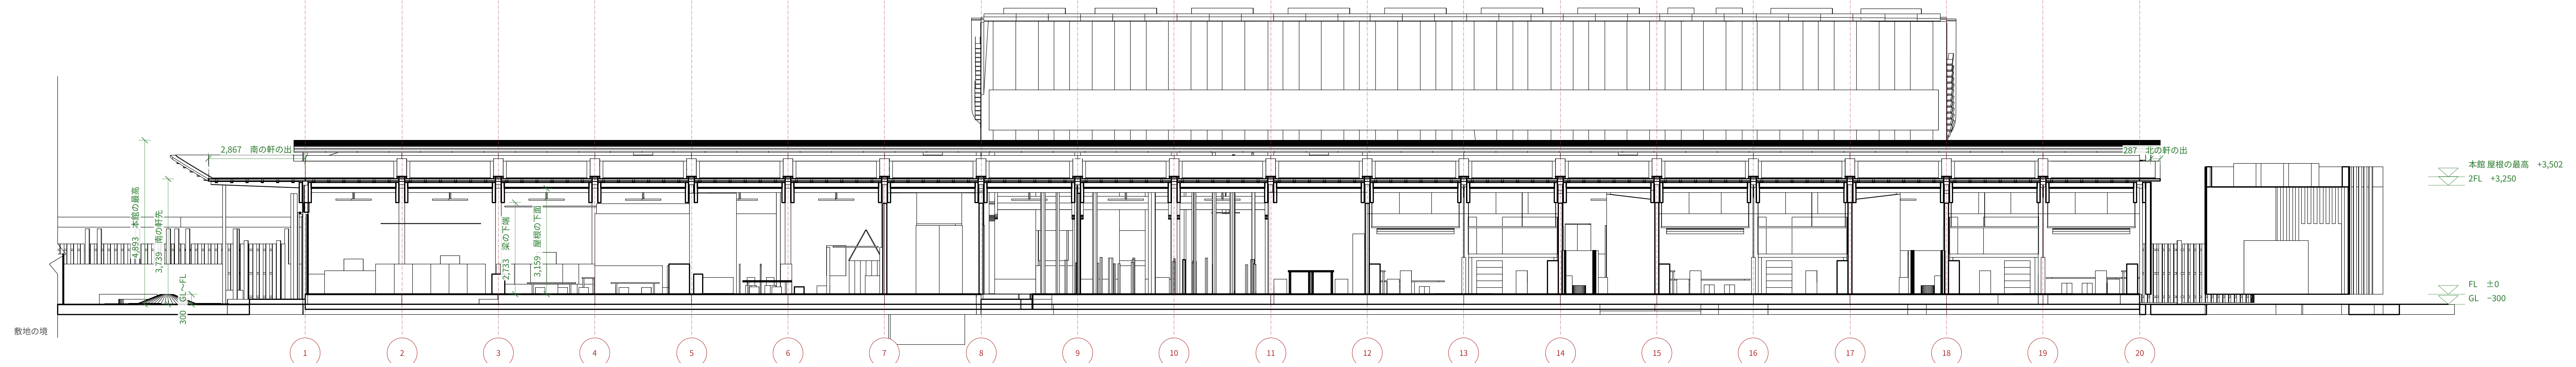
2,867　南の軒の出
287　北の軒の出
4,893　本館の最高
3,739　南の軒先
300　GL～FL
2,733　梁の下端
3,159　屋根の下面
本館 屋根の最高　+3,502
2FL　+3,250
FL　±0
GL　−300
敷地の境
1
2
3
4
5
6
7
8
9
10
11
12
13
14
15
16
17
18
19
20

断面図C　東西に切る（4歳・遊戯室）

1/100　空気の環境：本館と西館の架構、昼と夏の夜の風の道

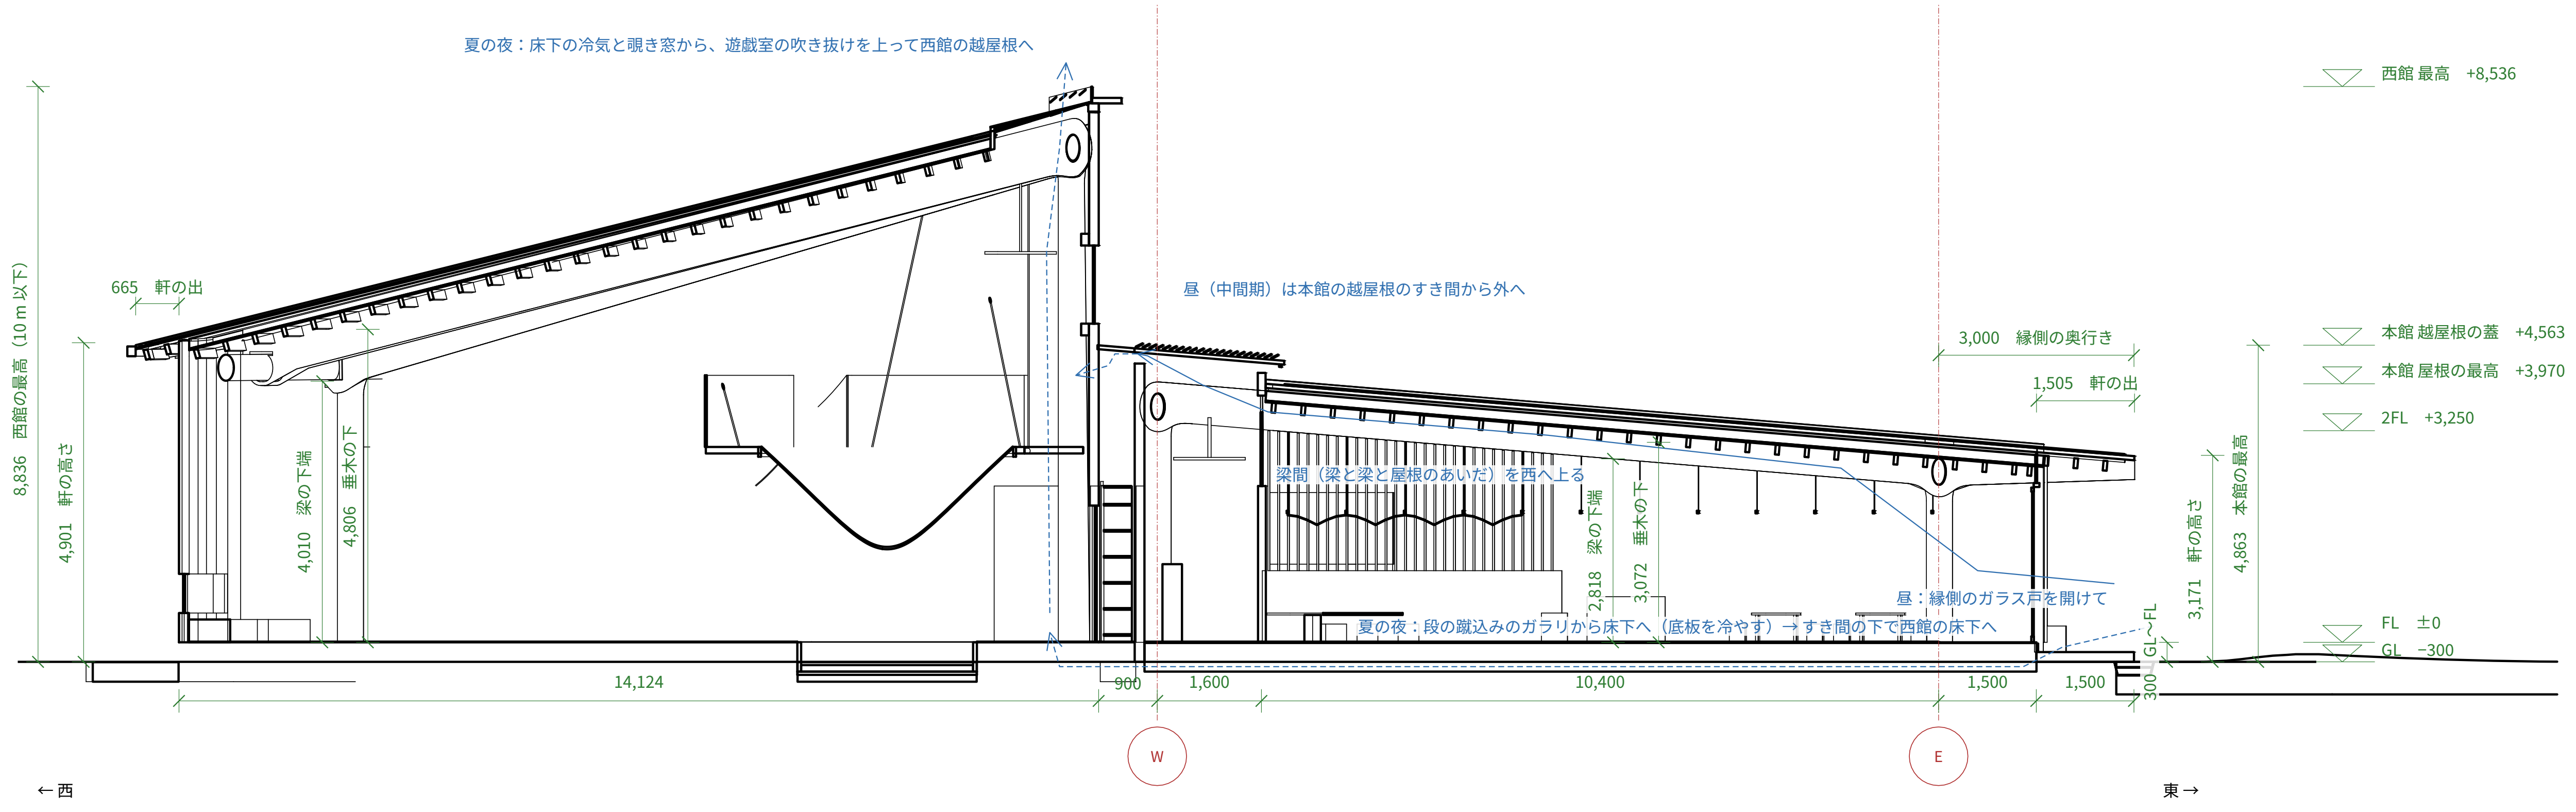
夏の夜：床下の冷気と覗き窓から、遊戯室の吹き抜けを上って西館の越屋根へ
昼（中間期）は本館の越屋根のすき間から外へ
梁間（梁と梁と屋根のあいだ）を西へ上る
昼：縁側のガラス戸を開けて
夏の夜：段の蹴込みのガラリから床下へ（底板を冷やす）→すき間の下で西館の床下へ
665　軒の出
8,836　西館の最高（10 m 以下）
4,901　軒の高さ
4,010　梁の下端
4,806　垂木の下
2,818　梁の下端
3,072　垂木の下
3,000　縁側の奥行き
1,505　軒の出
3,171　軒の高さ
4,863　本館の最高
GL～FL
300
西館 最高　+8,536
本館 越屋根の蓋　+4,563
本館 屋根の最高　+3,970
2FL　+3,250
FL　±0
GL　−300
14,124
900
1,600
10,400
1,500
1,500
W
E
←西
東→

断面図D　本館の横断（光の筋で切る）

1/100　北を見る　光の環境：光の筋の鏡面の溝・東のガラス戸・深い軒・西の吹き抜けの越屋根

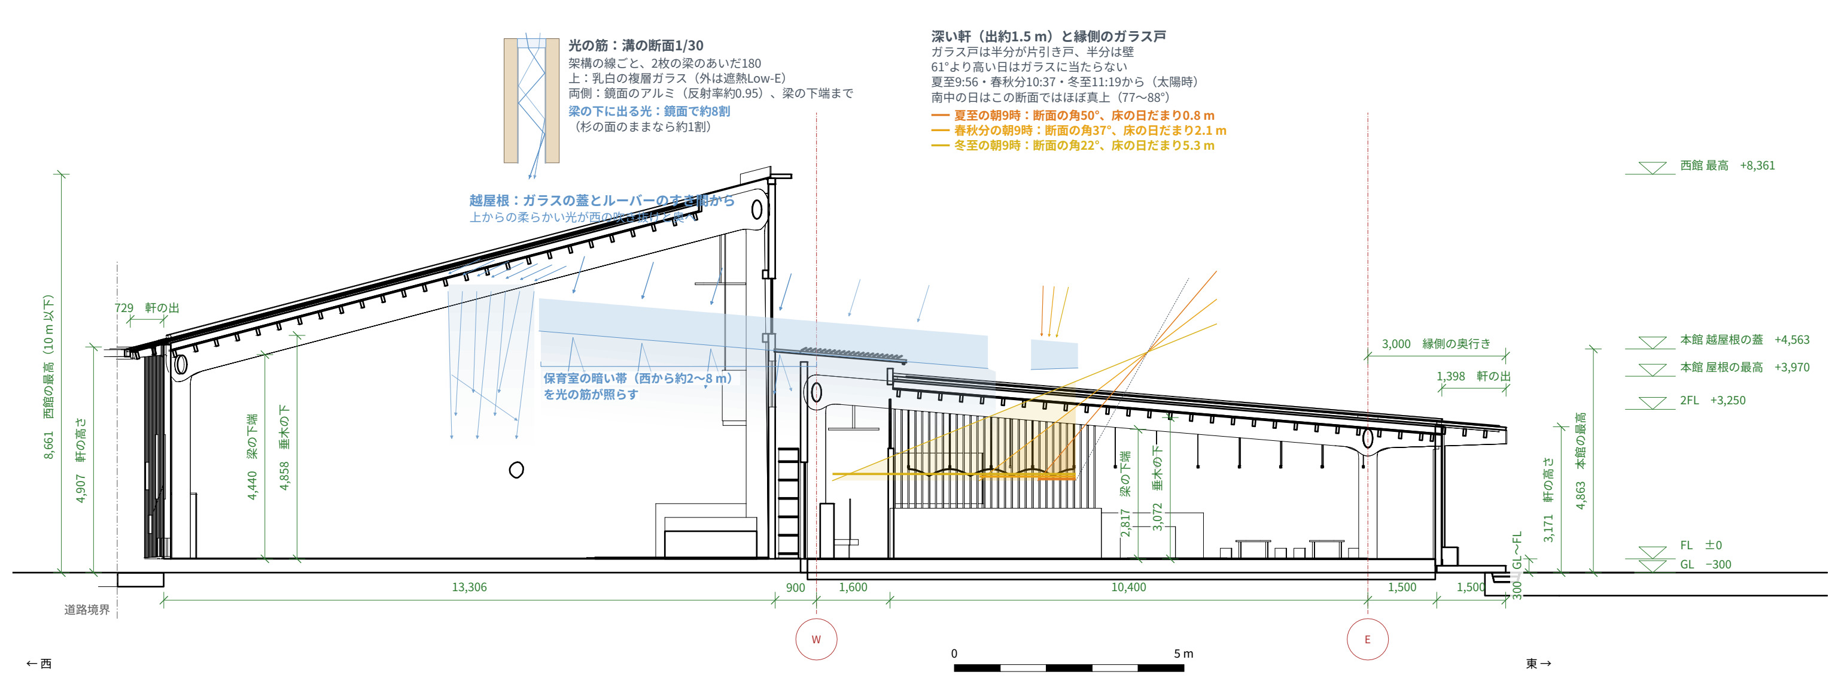
光の筋：溝の断面1/30
架構の線ごと、2枚の梁のあいだ180
上：乳白の複層ガラス（外は遮熱Low-E）
両側：鏡面のアルミ（反射率約0.95）、梁の下端まで
梁の下に出る光：鏡面で約8割
（杉の面のままなら約1割）
深い軒（出約1.5 m）と縁側のガラス戸
ガラス戸は半分が片引き戸、半分は壁
61°より高い日はガラスに当たらない
夏至9:56・春秋分10:37・冬至11:19から（太陽時）
南中の日はこの断面ではほぼ真上（77～88°）
— 夏至の朝9時：断面の角50°、床の日だまり0.8 m
— 春秋分の朝9時：断面の角37°、床の日だまり2.1 m
— 冬至の朝9時：断面の角22°、床の日だまり5.3 m
越屋根：ガラスの蓋とルーバーのすき間から
上からの柔らかい光が西の吹き抜けに落ちる
保育室の暗い帯（西から約2～8 m）
を光の筋が照らす
729　軒の出
8,661　西館の最高（10 m 以下）
4,907　軒の高さ
4,440　梁の下端
4,858　垂木の下
2,817　梁の下端
3,072　垂木の下
3,000　縁側の奥行き
1,398　軒の出
3,171　軒の高さ
4,863　本館の最高
GL～FL
300
西館 最高　+8,361
本館 越屋根の蓋　+4,563
本館 屋根の最高　+3,970
2FL　+3,250
FL　±0
GL　−300
13,306
900
1,600
10,400
1,500
1,500
道路境界
W
E
0
5 m
←西
東→

構造

架構と耐力壁の分布

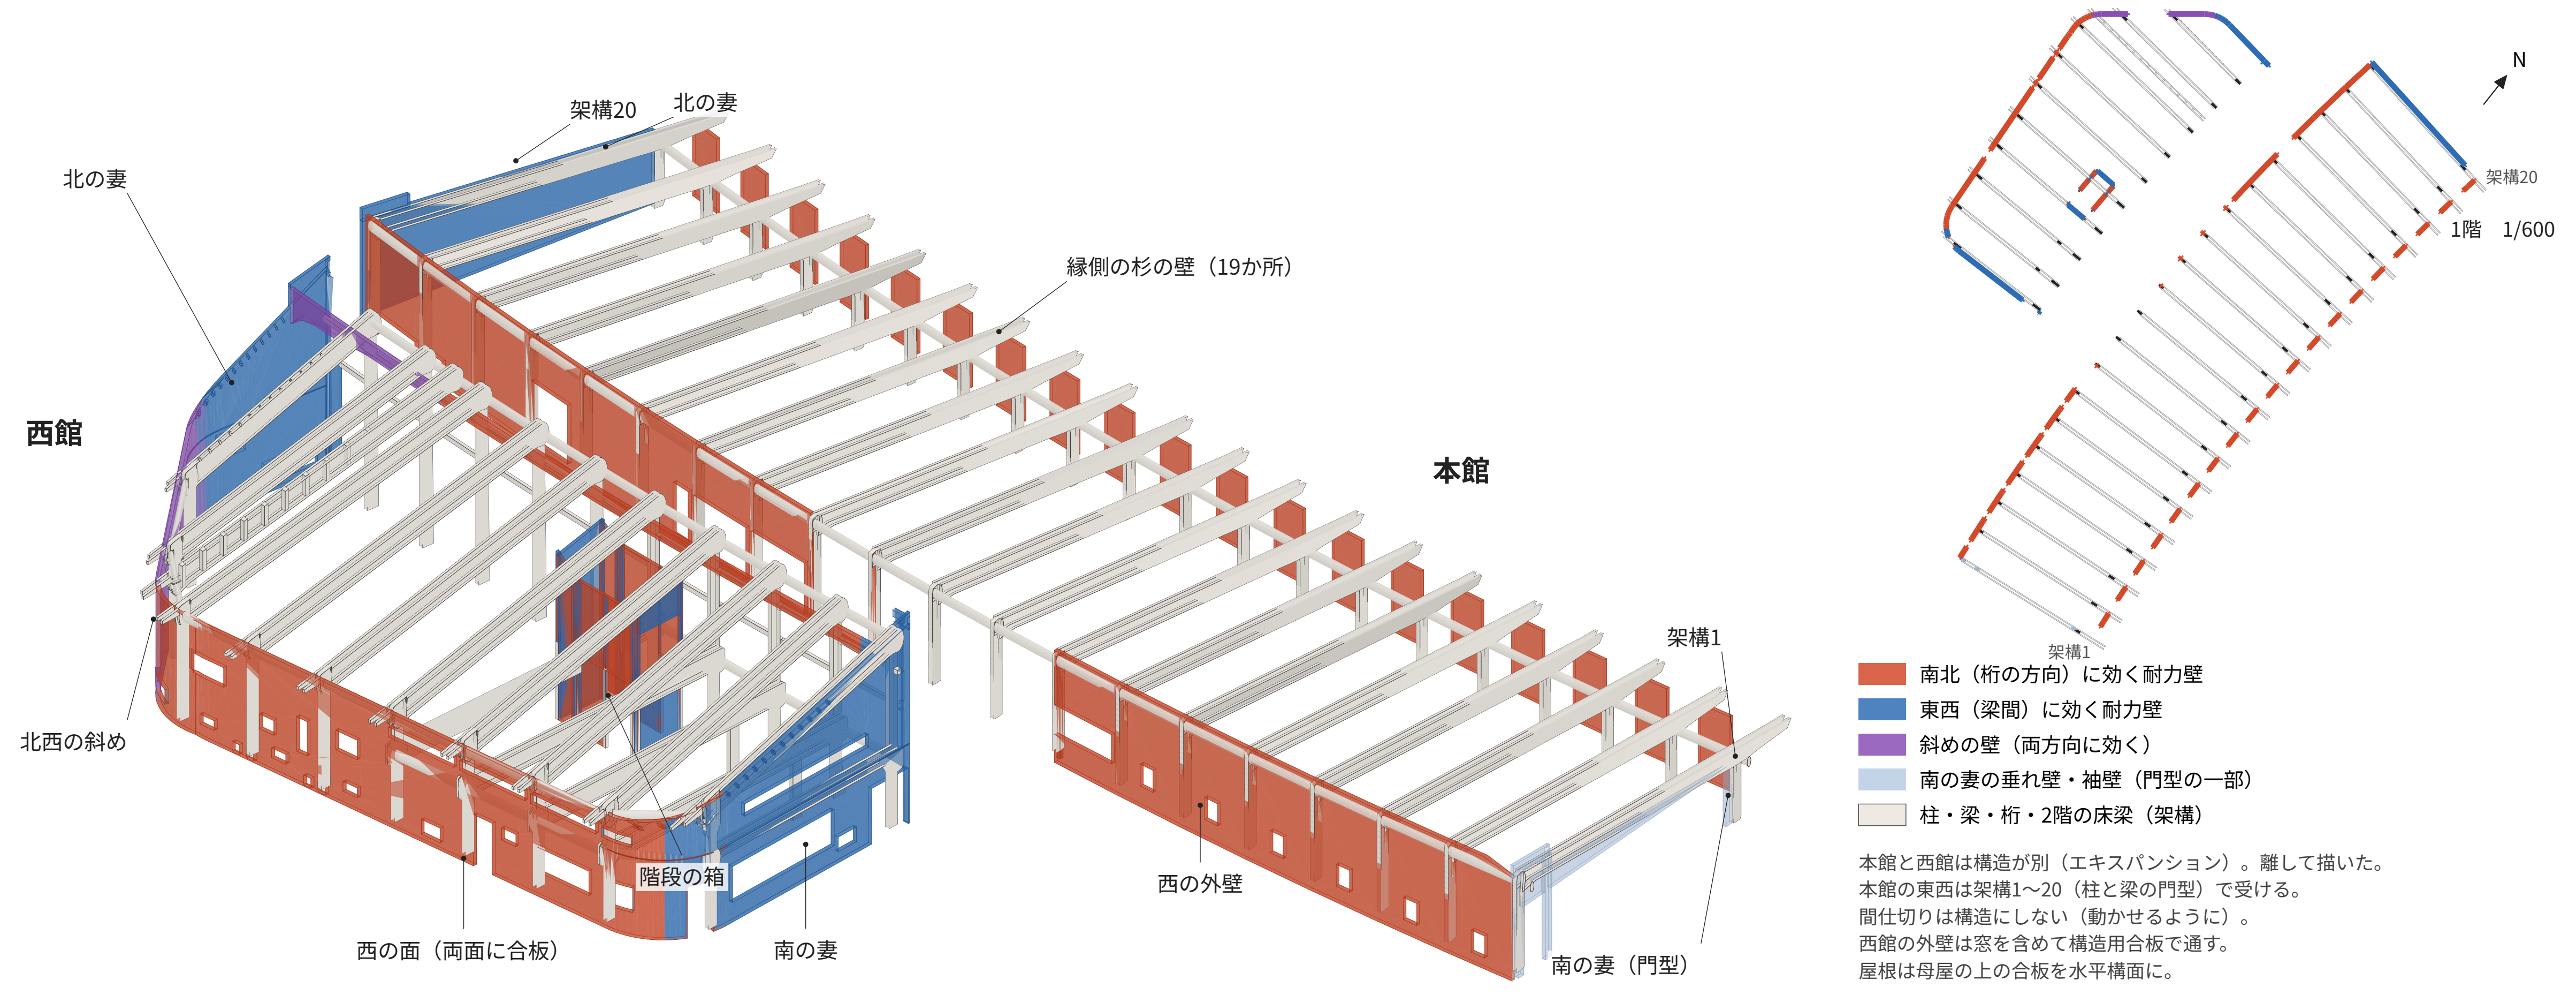
架構20
北の妻
北の妻
縁側の杉の壁（19か所）
西館
本館
北西の斜め
階段の箱
西の面（両面に合板）
南の妻
西の外壁
南の妻（門型）
架構1
N
架構20
1階　1/600
架構1

🟥 南北（桁の方向）に効く耐力壁
🟦 東西（梁間）に効く耐力壁
🟪 斜めの壁（両方向に効く）
▨ 南の妻の垂れ壁・袖壁（門型の一部）
☐ 柱・梁・桁・2階の床梁（架構）

本館と西館は構造が別（エキスパンション）。離して描いた。
本館の東西は架構1～20（柱と梁の門型）で受ける。
間仕切りは構造にしない（動かせるように）。
西館の外壁は窓を含めて構造用合板で通す。
屋根は母屋の上の合板を水平構面に。

季節ごとの空気環境

夏は夜の外気で床下の重さを冷やし、昼はその冷えと、触れて冷たい壁と天井扇で過ごす。冬は閉じて床から暖め、熱と湿気を逃がさない。春と秋は床下から越屋根へ風を通す。

季節	開け閉め	動かすもの	効くもの
夏の昼	窓・越屋根・床下の入口を閉じる	放射冷房のパネル・天井扇（下向き）・床下の送風	深い軒、夜に冷やした底板
夏の夜	縁側のガラリと西館の越屋根を開く（本館の越屋根は閉じる）	開け閉めは自動（外気が涼しいとき・雨で閉じる）	外気が床下の底板を冷やす。遊戯室の吹き抜けの高低差約8 m で引く
春・秋	窓・越屋根を開く	機械は止める	通風（梁間から越屋根へ）
冬	すべて閉じる	床下の暖房・全熱交換の換気・加湿・天井扇（上向きに弱く）	断熱と気密。ガラス戸の際の床からの暖気がガラスの冷えを止める

> **放射冷房のパネル**
> 保育室と遊戯室の壁、こどもの手の届く高さに置く。表面は約15°Cで、触れて「つめた！」とわかる。結露した水を外へ流して除湿も兼ねる。風が無いので静かで、午睡を妨げない。

環境への配慮（LEED v5 Goldを目指す）

LEED v5（USGBC）　https://www.usgbc.org/leed/v5

統合的なプロセス（IP）	一つの形で二つ以上を解く。本館の弧＝朝の日と、夏の夜に谷を下りる冷気（1枚目）。片流れの屋根＝景観と、越屋根へ上る空気の流れ（断面C）。縁側の段のガラリ＝夜の外気を床下へ入れ、ガラス戸をすっきり保つ。井戸＝冷暖房の熱源と、災害時の近隣の水
立地と交通（LT）	車は5台に絞り、送迎は徒歩と自転車（駐輪21台）。西の道に歩道を開く
持続可能な敷地（SS）	小竹藪公園と既存の木を残す。園庭の林。雨庭と浸透側溝で雨を敷地に返す
水の効率（WE）	雨を庭へ。地下水を使う
エネルギーと大気（EA）	断熱・気密、深い軒と遮熱Low-Eで日射を切る、ベタ基礎の底板に夜の冷えをためる、放射冷房と全熱交換、地下水を熱源にしたヒートポンプ、屋根材型の太陽光と蓄電池
材料と資源（MR）	北山杉の間伐材、木造。3 mの架構は残し中は変えられる（スケルトン＆インフィル）。野菜くずのコンポスト
室内環境の質（EQ）	光の筋の鏡面で奥まで昼光。風の音のない放射冷房。自然換気（床下→梁間→越屋根）。静養室と大人の便所は別の換気。2階の窓から川と空
地域の優先（PR）	災害時の持ちつ持たれつ：太陽光と蓄電池の電気と、地下水を近隣に提供できる。浸水のときは京都工芸繊維大学へ避難の協定

inspired by　参照した建築

Asilo Nido Iride　Mario Cucinella Architects・Guastalla・2015
→梁の列が並ぶ長細い本館と、外に付く付属の建物

Tamedia　坂茂・Zürich・2013
→梁の端の楕円の頭と、それを貫く楕円の桁

レイモンド斑鳩こども園　キノアーキテクツ・斑鳩・2026
→室内に木を立てる（ホールの北山杉）・内と外の回廊・回廊と遊戯室に居場所

KAIT工房　石上純也・厚木・2008
→柱の配列：見る向きで景色が変わる並び

認定こども園らみどり　はりゅうウッドスタジオ・須賀川・2026
→内と外の二重の縁側、遊具を置かない地形の園庭

仙田満の園舎　環境デザイン研究所
→摺鉢のネット、キャットウォーク、ニッチ

Waldorf School of the Peninsula　California
→遊戯室の切り株

スターバックス京都二寧坂ヤサカ茶屋店　町家の改修・京都・2017
→放射冷房

面積表

m²（壁芯、3dmから自動）

室	要求	計画
乳児室（0～1歳）	約60×2	120.5
保育室（2歳）	約60	60.0
保育室（3～5歳）	約60×3	181.2
遊戯室	240以上	266.1
便所	適宜	17.2
食堂	必要に応じて	なし
園庭	350以上	982.2
事務室	約60	69.8
休憩室	約60	60.4
医務室	約30	30.1
調理室	約60	65.7
便所（大人用）	適宜	13.9
機械室	約30	30.0
倉庫	約30	36.2
駐車場	5台以上	5台（うち搬入1）
駐輪スペース	適宜	21台（保護者12・職員9）
延床（2,000以内）		**1,310.8**

建築設計実習 II — I　2026.11.05　木田

［割付の注記］フォーカス：上に縦断A（弧の長さ）を一続きに。その下に二つの横断（1/100）：断面Cに空気の環境（本館と西館の架構と風の道）、断面D（本館、光の筋で切る）に光の環境。下に構造（架構と耐力壁の分布）・季節ごとの空気環境と環境への配慮・inspired byと面積表　／　目に入る順：縦断A（上の帯）→断面C（空気）・断面D（光）→季節ごとの空気環境・配慮→構造→inspired by・