壁に貼ったとき　3列：1 ｜ 2・3 ｜ 4・5（1は二段の真ん中）

目の高さ1.5 m

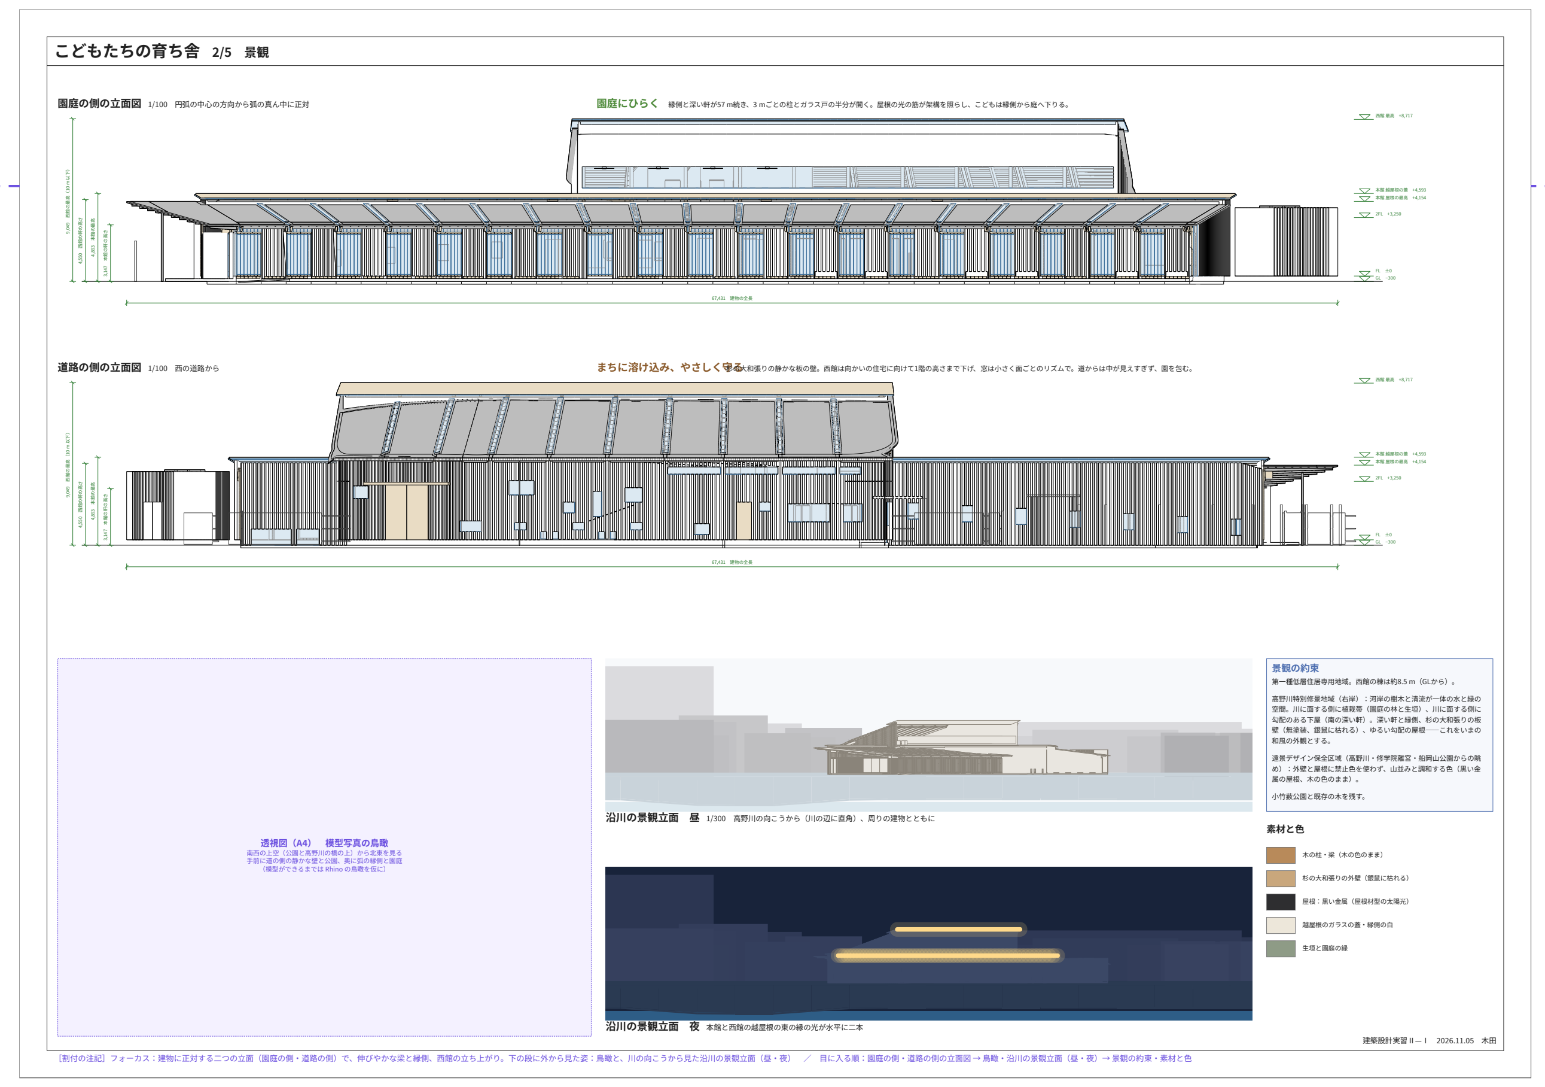

こどもたちの育ち舎 2/5　景観

園庭の側の立面図 1/100　円弧の中心の方向から弧の真ん中に正対

園庭にひらく

道路の側の立面図 1/100　西の道路から

まちに溶け込み、やさしく守る

透視図（A4）　模型写真の鳥瞰

沿川の景観立面　昼　1/300　高野川の向こうから（川の辺に直角）、周りの建物とともに

沿川の景観立面　夜　本館と西館の越屋根の東の縁の光が水平に二本

景観の約束

素材と色

- 木の柱・梁（木の色のまま）
- 杉の大和張りの外壁（銀鼠に枯れる）
- 屋根：黒い金属（屋根材型の太陽光）
- 越屋根のガラスの裏・縁側の白
- 生垣と園庭の緑

建築設計実習Ⅱ－Ⅰ　2026.11.05　木田

こどもたちの育ち舎 4/5　平面図　1階・2階

平面図　1階　FL+1500 で切断／2階（西館）2FL+1000 で切断　1/100

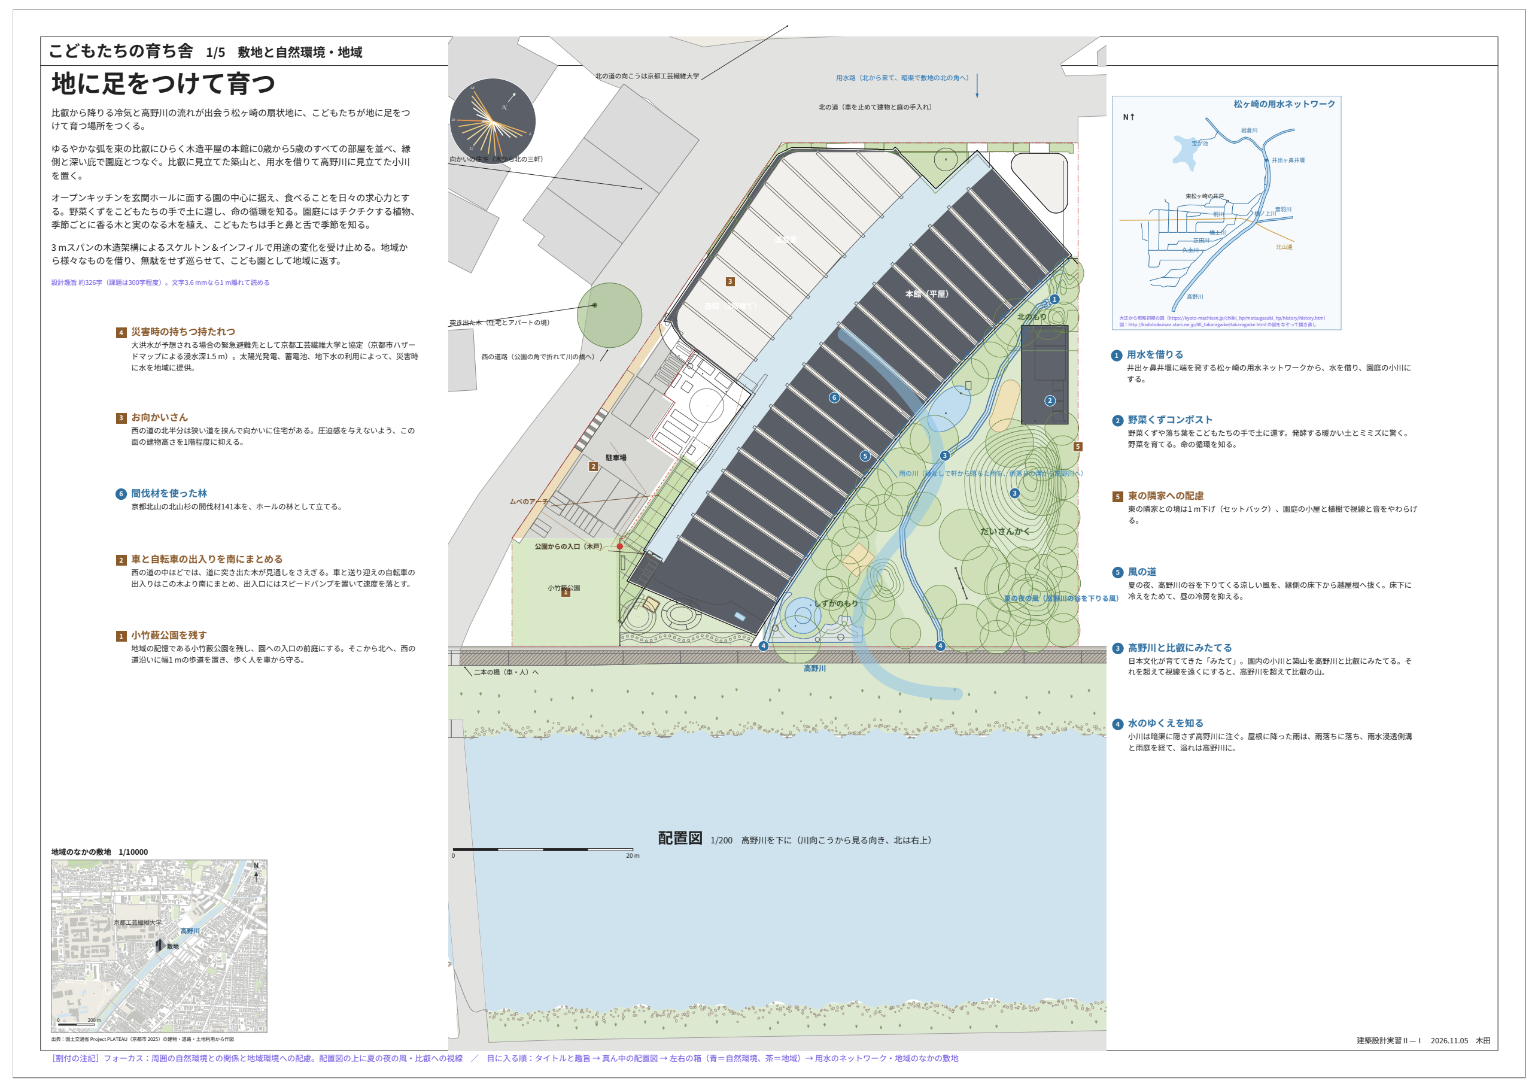

こどもたちの育ち舎 1/5　敷地と自然環境・地域

地に足をつけて育つ

配置図　1/200　高野川を下に（川向こうから見る向き、北は右上）

松ヶ崎の用水ネットワーク

地域のなかの敷地　1/10000

建築設計実習Ⅱ－Ⅰ　2026.11.05　木田

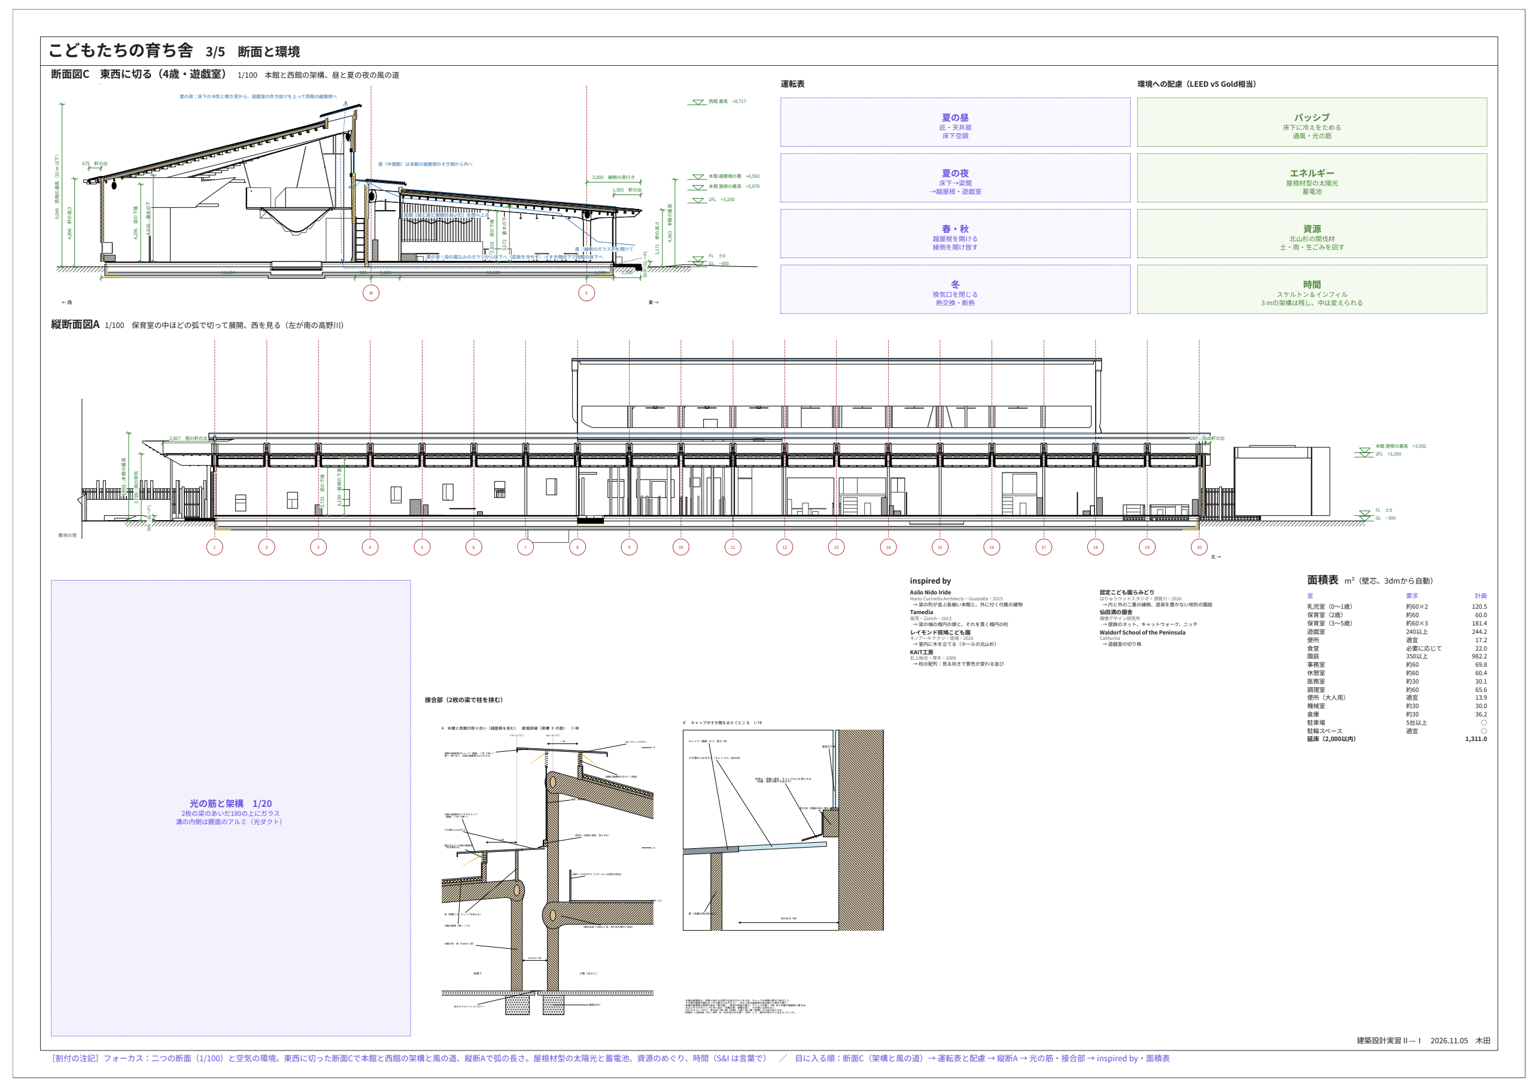

こどもたちの育ち舎 3/5　断面と環境

断面図C　東西に切る（4歳・遊戯室）

縦断面図A

光の筋と架構　1/20

面積表

建築設計実習Ⅱ－Ⅰ　2026.11.05　木田

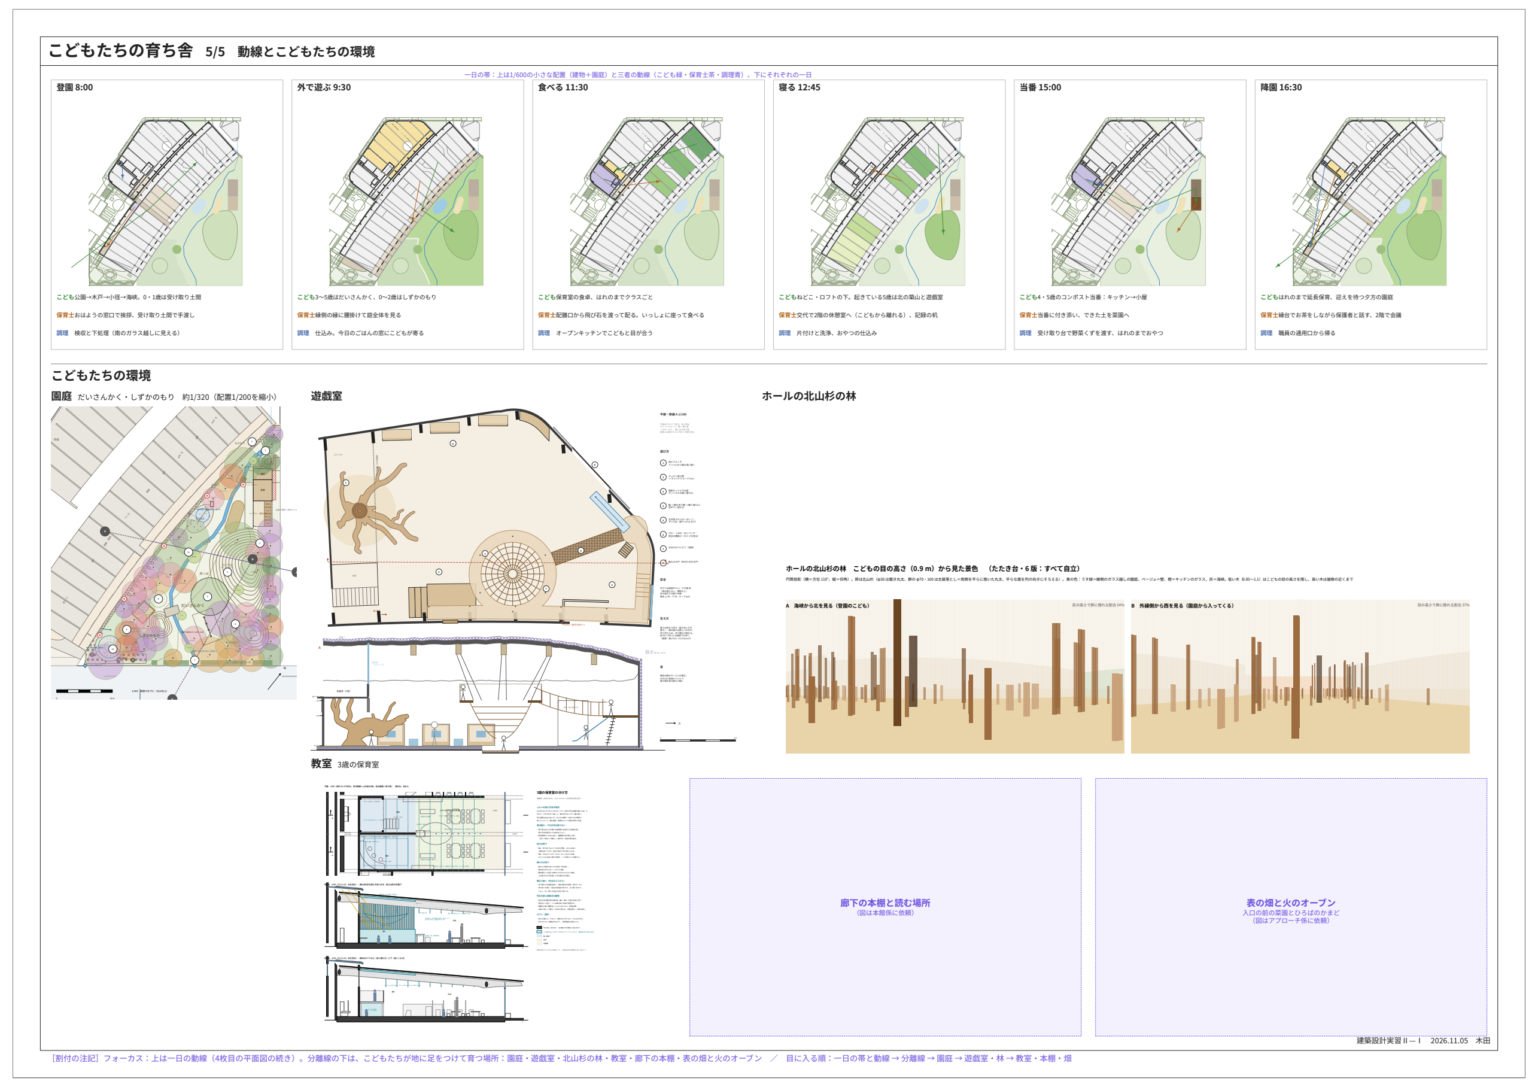

こどもたちの育ち舎 5/5　動線とこどもたちの環境

登園 8:00　外で遊ぶ 9:30　食べる 11:30　寝る 12:45　当番 15:00　降園 16:30

こどもたちの環境

園庭　遊戯室　ホールの北山杉の林　教室

廊下の本棚と読む場所

表の畑と火のオーブン

建築設計実習Ⅱ－Ⅰ　2026.11.05　木田

1　敷地と自然環境・地域（二段の真ん中）。

その右に2　景観（立面図1/100、下の段に沿川の景観立面）、その下に3　断面と環境（断面図1/100）。

その右に4　平面図、その下に5　動線とこどもたちの環境（一日の帯は平面図の続き）。

外から中へ：敷地→外から見た姿と切った姿→中の平面と暮らし。

2・3・4枚目の立面・断面・平面は3dmから自動の図を実寸で貼る。

床