地に足をつけて育つ


比叡から降りる冷気と高野川の流れが出会う松ヶ崎の扇状地に、こどもたちが地に足をつけて育つ場所をつくる。ゆるやかな弧を東の比叡にひらく木造平屋の本館に0歳から5歳のすべての部屋を並べ、縁側と深い庇で園庭とつなぐ。比叡に見立てた築山と、用水を借りて高野川に見立てた小川を置く。

オープンキッチンを玄関ホールに面する園の中心に据え、食べることを日々の求心力とする。野菜くずをこどもの手で土に還し、命の循環を知る。園庭には季節ごとに香る木と実のなる木を植え、こどもたちは手と鼻と舌で季節を知る。

3ｍスパンの木造架構によるスケルトン＆インフィルで用途の変化を受け止める。LEED v5 Gold相当を目指す。地域から様々なものを借り、無駄をせず巡らせて、こども園として地域に返す。

設計趣旨 約332字（課題は300字程度）。文字3.6 mmなら1 m離れて読める

配置図の注
- 駐車5台・搬入は南（川側）。行事の日は駐車場を駐輪に
- セキュリティの線の出入口は公園の木戸だけ
- 園庭への搬入は公園の東の縁から川沿いの帯を通って
- 敷地の境から：北東の隣家1ｍ（厳守）、ほかは1ｍ

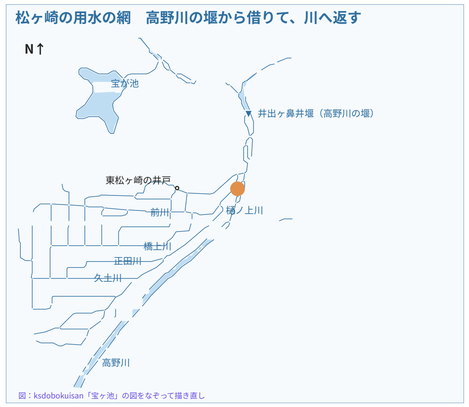

配置図　1/200　高野川を下に（川向こうから見る向き、北は右上）

点線の枠＝園庭のチャットの配置1/200（garden01）を実寸で重ねた。本番は一枚に描き直す



地域2　向かいの住宅へ
狭い道をはさんで向き合う住宅に対し、西館の西の端は1階の高さに抑えた。

地域1　車は西の道の真ん中より南で
西の道は突き出た木で見通しが悪い。外からの車の出入り（駐車・搬入）は、西の道の真ん中より南（川の側）にまとめた。

地域4　小竹薮公園を残す
地域の記憶の公園をそのまま残し、園の入口の前庭にする。

地域5　災害時に水を届ける
地下水をくみ上げて、災害時に近隣に水を届ける。屋根材型の太陽光と蓄電池で停電の時も動く。

自然1　用水を借りる
高野川の上の堰で取った水が、松ヶ崎の田を潤してきた用水の網を巡る。その水を借りる。
北の道の下の暗渠から敷地の北の角へ、北のもりのみなもとに湧き出し、小川になって高野川へ返る。

自然4　地下の水と北山の木も借りる
松ヶ崎は地面を走る用水と地下の水の両方が豊か。涌泉寺の井戸に見るように井戸水が豊富で、その地下水も借りる。
京都北山の北山杉の間伐材141本を、ホールの林に立てる。

地域3　東の隣家へ
視線と音に配慮：境から1ｍ、木の帯、園庭の小屋が声の衝立になる。

自然3　比叡と高野川のうつし
築山は比叡のうつし。ホールから頂の向こうに比叡が見える。
小川は高野川のうつし。足もとを掘った土で築山を盛る。


自然2　山から川へ
みなもとから縁側の前・原っぱを流れ、護岸の溝を滑り落ちて高野川に合流するまでを、こどもが追える。
雨は樋に隠さず、雨の川から同じ溝で川へ。

［割付の注記］フォーカス：周囲の自然環境との関係（用水を借りる・山から川へ・比叡と高野川のうつし・北山杉と地下水）と地域環境への配慮　／　目に入る順：タイトルと趣旨 → 真ん中の配置図 → 左右の箱（青＝自然環境、茶＝地域）→ 用水のネットワーク

こどもたちの育ち舎　2/5　景観


園庭の側の立面図　1/100　円弧の中心の方向から弧の真ん中に正対

伸びやかな梁と縁側（梁の端・庇が3ｍごとに並ぶ）。屋根は屋根材型の太陽光

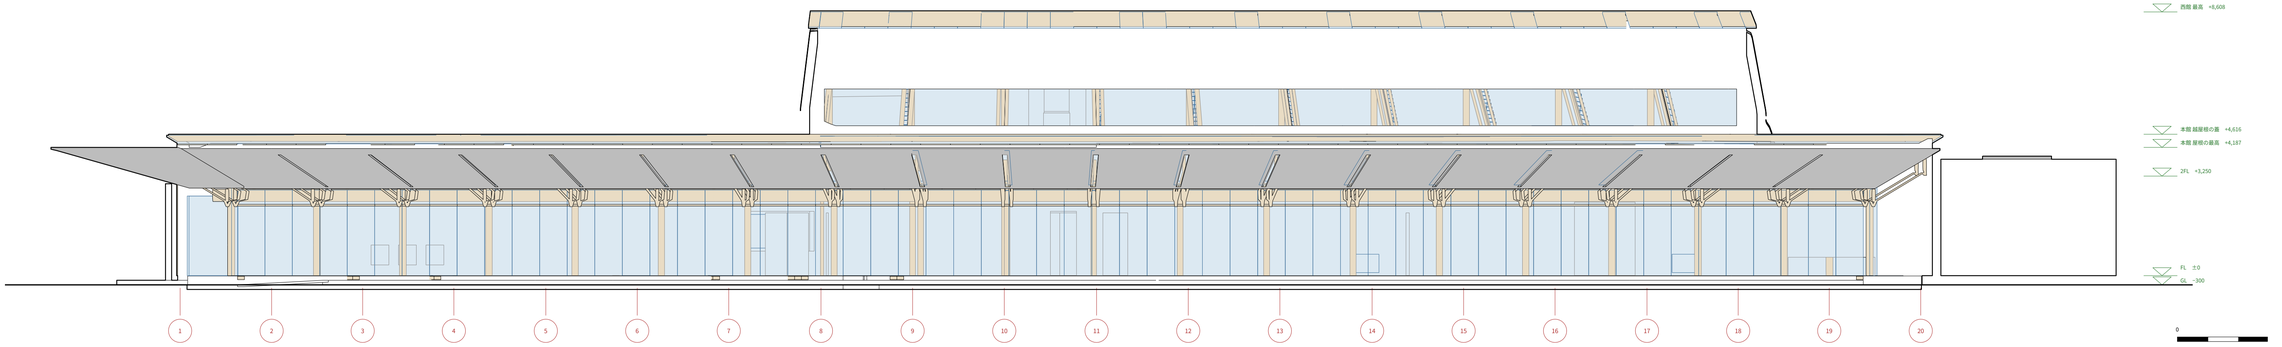


縦断面図A　1/100　保育室の中ほどの弧で切って展開、西を見る（左が南の高野川）

左（南）の高野川の崖から右（北）の大学へ、低い本館 → 高い西館 → おむすび。地域の建物の高低の流れに沿う

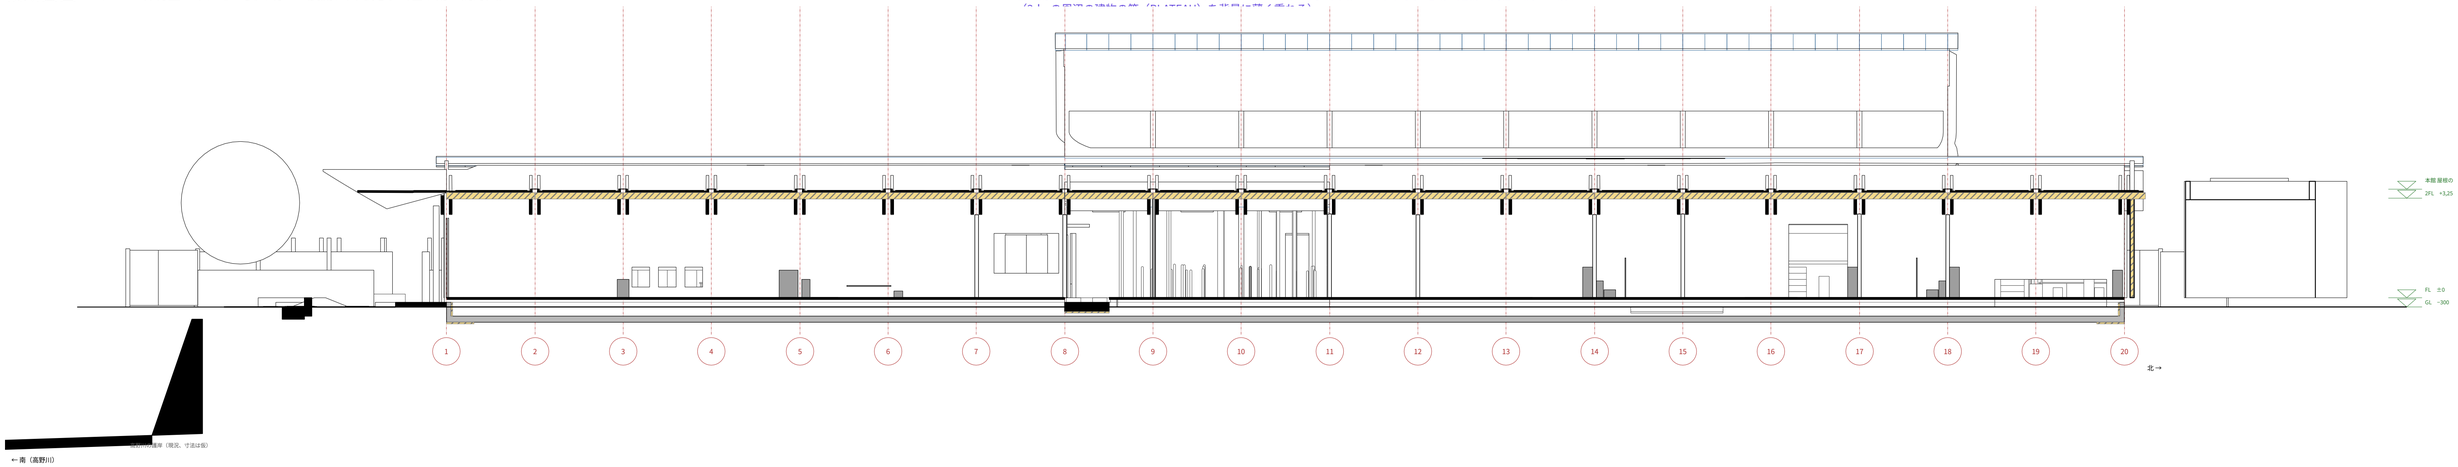


道路の側の立面図　1/100　西の道路から

西館の西端は1階の高さ（向かいの住宅を点線で描き足す）。西館の立ち上がりが北で主張する

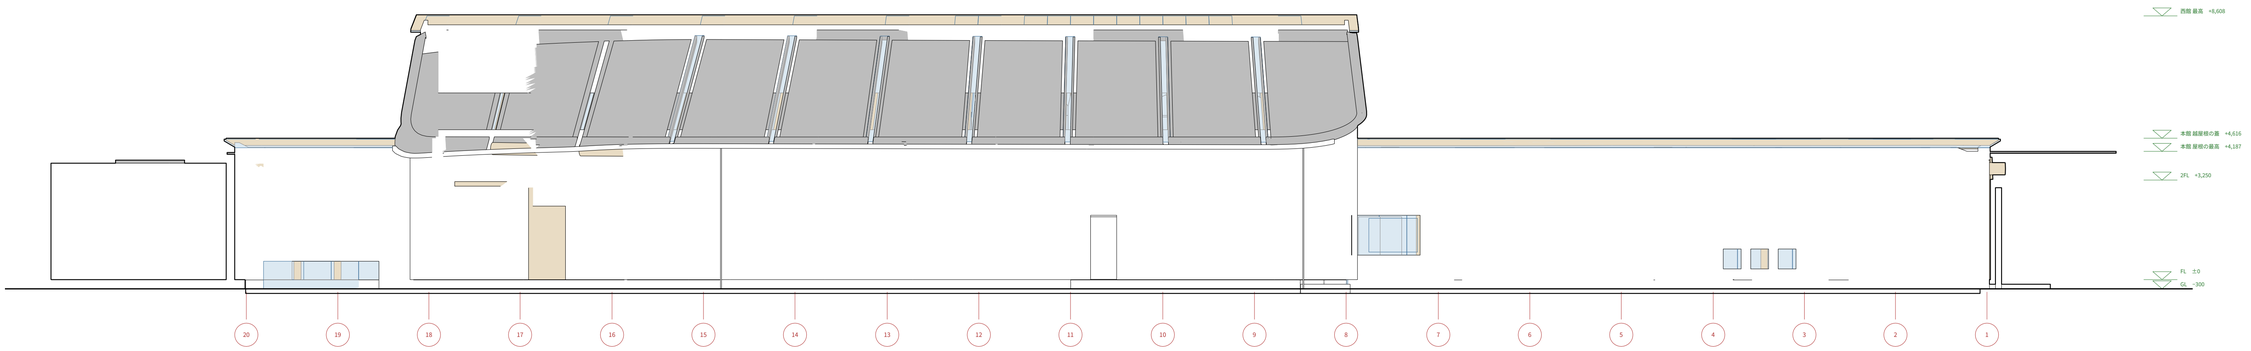

高野川の側の立面図　1/200　川の向こうから

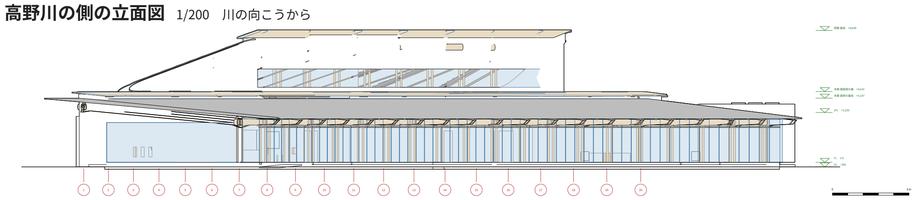

夜の立面（園庭の側）

黒地に越屋根の東の縁の光の線だけ
水平の光が一本、川向こうから見える
（模型の夜景写真でもよい）

模型写真　鳥瞰

敷地と高野川・崖・公園・西の道・園庭
配置図と同じ向き（高野川を手前）
川側が低く北へ高くなる流れが見える角度で

［割付の注記］フォーカス：高野川の側は低く、北の大学に向かって高く（地域の高低差の流れ）。同時に、伸びやかな梁・西館の立ち上がり・夜の水平の光で主張する　／　目に入る順：園庭の側の立面 → 縦断A（川から北へ）→ 道路の側の立面 → 高野川の側・夜

こどもたちの育ち舎　3/5　すべての人の一日　1階平面

建築設計実習Ⅱ－Ⅰ　2026.11.05　木田




面積表　m²（壁芯、3dmから自動）

室	要求	計画
乳児室（0〜1歳）	約60×2	120.5
保育室（2歳）	約60	60.0
保育室（3〜5歳）	約60×3	181.3
遊戯室	240以上	243.5
便所	適宜	57.3
食堂	必要に応じて	21.9
園庭	350以上	982.2
事務室	約60	73.8
休憩室	約60	62.9
医務室	約30	30.1
調理室	約60	65.7
便所（大人用）	適宜	17.1
機械室	約30	30.0
駐車場	5台以上	○
延床（2,000以内）		**1,286.7**

平面は3dmから自動（1/100）

一日の帯：上は1/700の小さな配置（建物＋園庭）と三者の動線（こども緑・保育士茶・調理青）、下にそれぞれの一日

登園 8:00

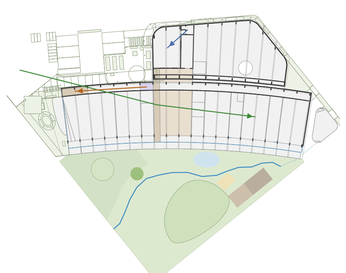


こども公園→木戸→小径→海峡。0・1歳は受け取り土間

保育士おはようの窓口で挨拶、受け取り土間で手渡し

調理　検収と下処理（南のガラス越しに見える）

外で遊ぶ 9:30

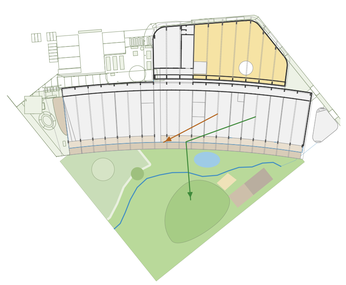


こども3〜5歳はだいさんかく、0〜2歳はしずかのもり

保育士縁側の縁に腰掛けて庭全体を見る

調理　仕込み。今日のごはんの窓にこどもが寄る

食べる 11:30

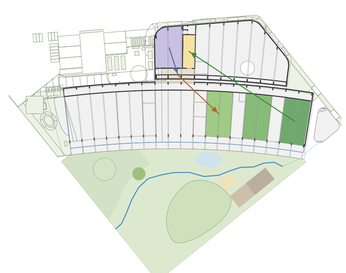


こども保育室の食卓、はれのまでクラスごと

保育士配膳口から飛び石を渡って配る。いっしょに座って食べる

調理　オープンキッチンでこどもと目が合う

寝る 12:45

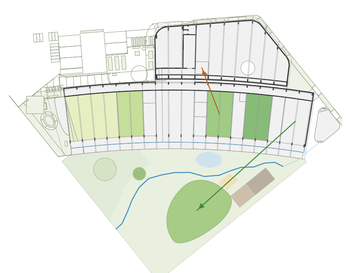


こどもねどこ・ロフトの下。起きている5歳は北の築山と遊戯室

保育士交代で2階の休憩室へ（こどもから離れる）、記録の机

調理　片付けと洗浄、おやつの仕込み

当番 15:00

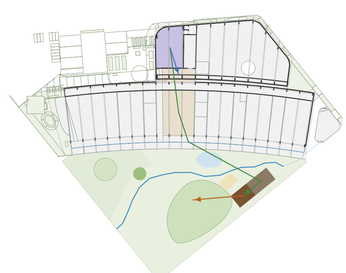


こども4・5歳のコンポスト当番：キッチン→小屋

保育士当番に付き添い、できた土を菜園へ

調理　受け取り台で野菜くずを渡す、はれのまでおやつ

降園 16:30

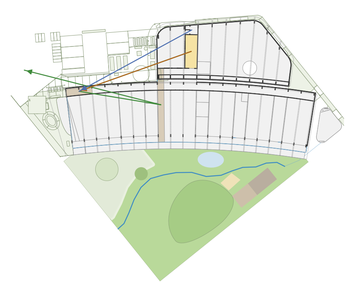

こどもはれのまで延長保育、迎えを待つ夕方の園庭

保育士縁台でお茶をしながら保護者と話す、2階で会議

調理　職員の通用口から帰る

［割付の注記］フォーカス：こども・保育士・調理の職員が一日を過ごす場所としての平面（食べる・寝る・遊ぶ）　／　目に入る順：1階平面（家具・先生の席）と面積表 → 一日の帯と動線（こども／保育士／調理）

こどもたちの育ち舎　4/5　こどもたちへの環境

地に足をつけて育つオープンキッチンを玄関ホールに面する園の中心に据え、食べることを日々の求心力とする。野菜くずをこどもの手で土に還し、命の循環を知る。園庭には季節ごとに香る木と実のなる木を植え、こどもたちは手と鼻と舌で季節を知る。

園庭　だいさんかく・しずかのもり　1/250（園庭のチャットの配置1/200を縮小）



内観（A4）
ホールの北山杉の林・海峡と飛び石・オープンキッチン
梁の見える天井・光の筋
こどもの目の高さで（レンダリングか模型写真）


見立て
築山は比叡、小川は高野川。ホールから頂の向こうに比叡。足もとを掘った土で盛る。

水の行方を隠さない
用水→みなもと→小川→護岸の溝→高野川。雨は樋なしで雨の川へ。


土と命のめぐり
野菜を育て、野菜くずはこどもの手でコンポストへ、土に還す。土の中のミミズに驚く。

季節を手と鼻と舌で
季節ごとに香る木と実のなる木。抱きつける木。とげの木は一本だけ、わざと。

静かな場所と先生の目
しずかのもりは柵で囲まず、道の上の関守石で「ここからはしずかに」。取り除くのは命に関わる危険だけ。

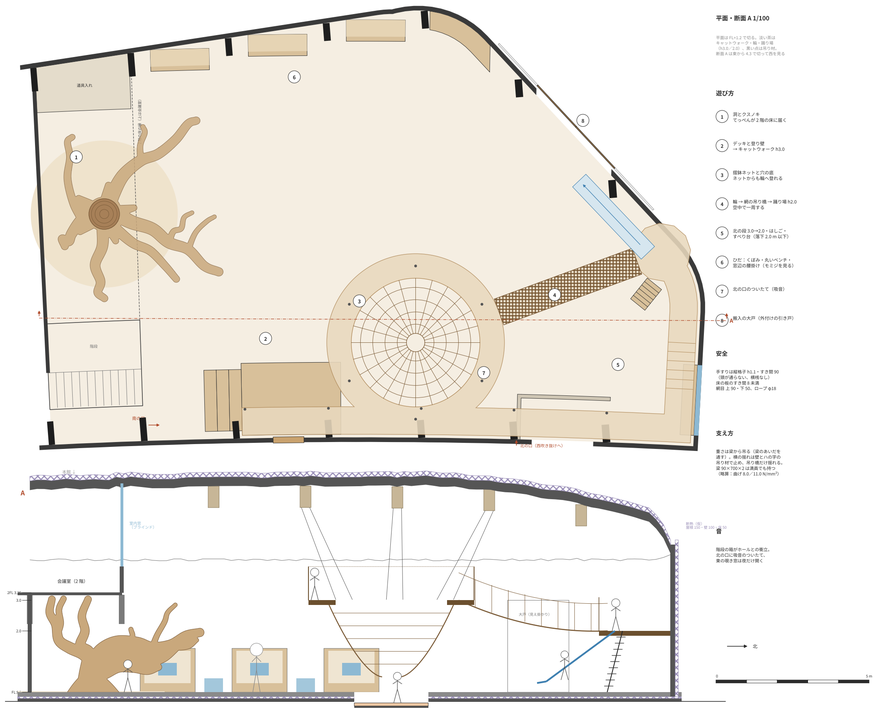

ホールの北山杉の林　こどもの目の高さ（0.9 m）から

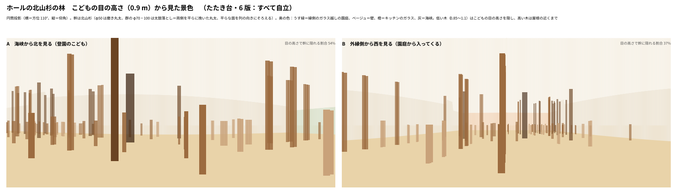


洞のクスノキ　遊戯室の切り株、断面パース



洞のクスノキ
2 階の床の下の低い洞（梁の下 2.23）。クスノキの枝の先が天井に触れ、木が 2 階を支えているように見える。
北の柱は床の縁の下をくぐって遊戯室の高い側へ（この図では切断面で切れている）。

園庭の断面　1/200　A 比叡へ／B 高野川・河川敷へ

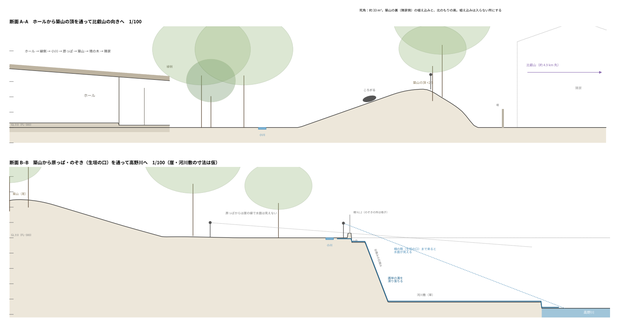


［割付の注記］フォーカス：こどもたちが地に足をつけて育つ場所：食べることを中心に命の循環を知り、季節を手と鼻と舌で知る園庭、遊戯室と北山杉の林　／　目に入る順：趣旨の言葉 → 園庭 → 内観 → 園庭の4つ → 遊戯室 → 林・洞 → 園庭の断面

こどもたちの育ち舎　5/5　環境

建築設計実習Ⅱ－Ⅰ　2026.11.05　木田

断面図C　4歳・遊戯室の摺鉢ネット 1/50（1/100の自動の図を2倍）　西の道路から園庭へ

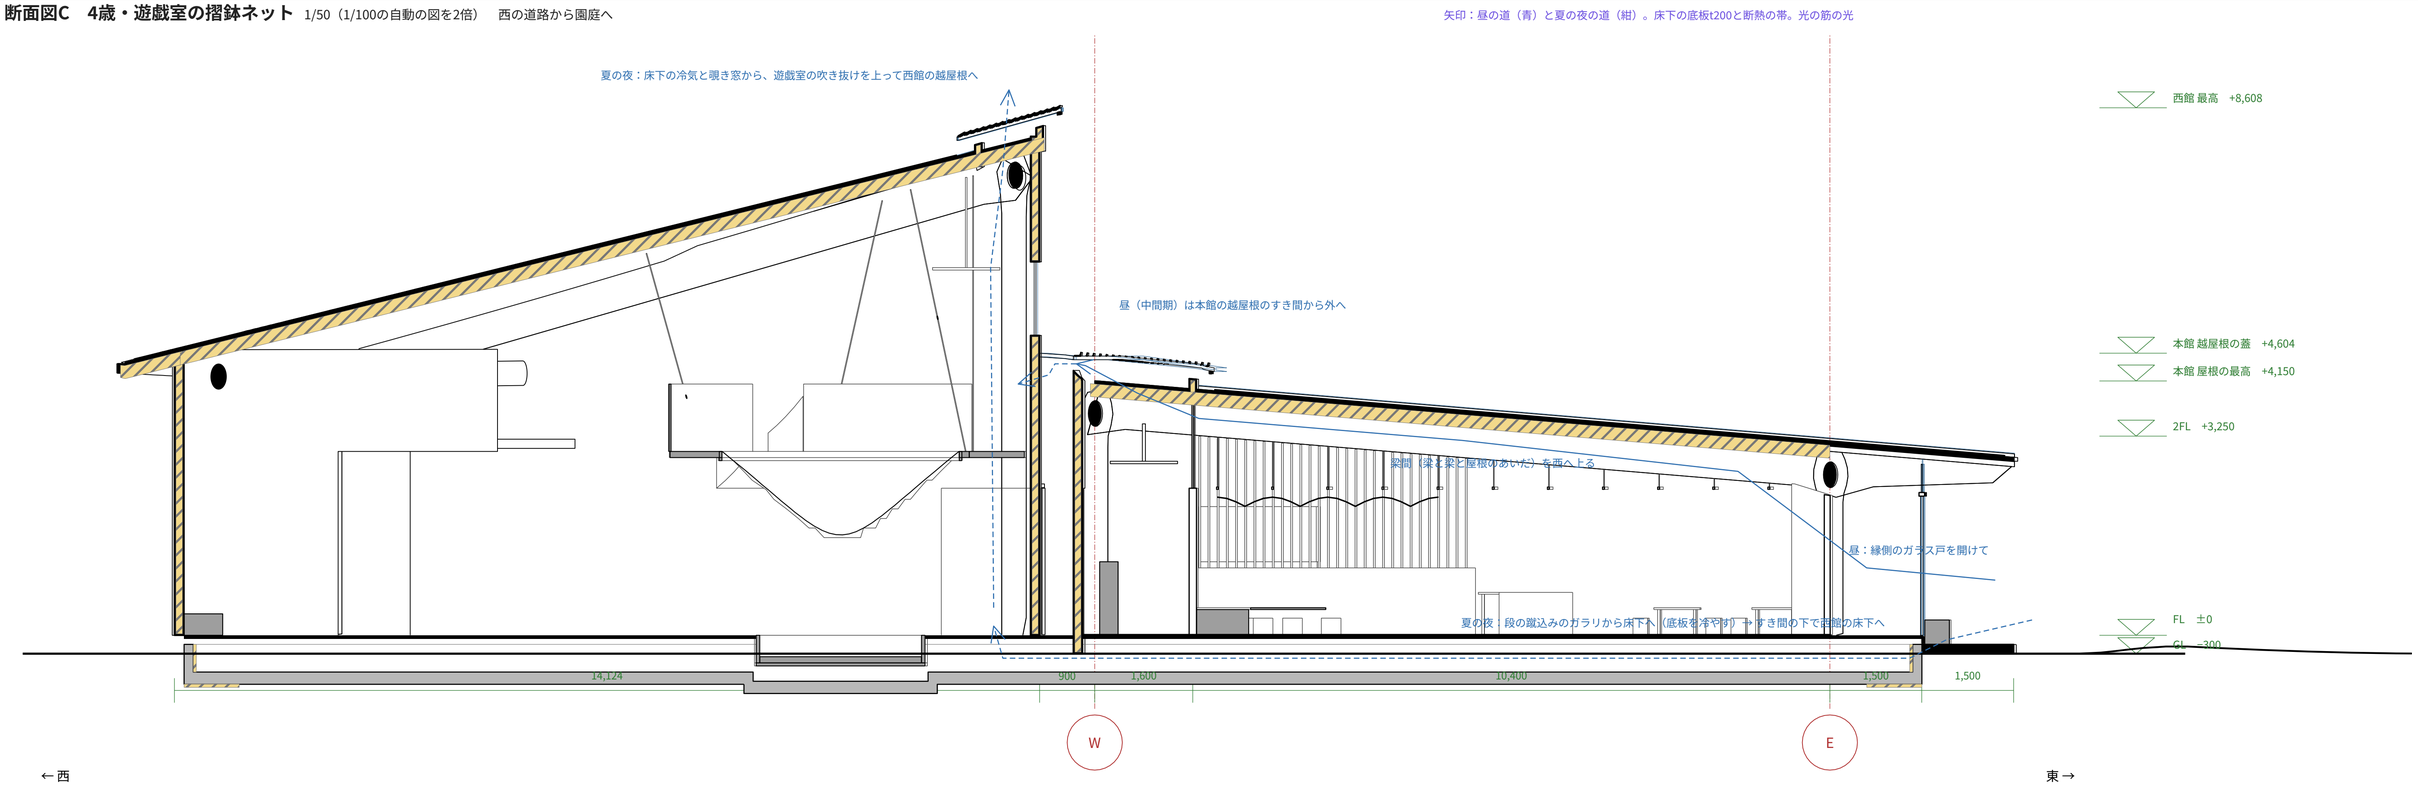

運転表

夏の昼
庇で遮る・天井扇
床下空調（底板の冷え）

夏の夜
縁側の段のガラリ→床下→梁間
→越屋根・遊戯室の吹き抜け

春・秋
越屋根の換気口を開ける
縁側を開け放す

冬
換気口を閉じる・熱交換
基礎断熱・屋根の断熱

環境への配慮（LEED v5 Gold相当を目指す）

パッシブ
床下に冷えをためる
越屋根の通風、光の筋の昼光

エネルギー
屋根材型の太陽光
蓄電池（災害時の拠点）


資源
北山杉の間伐材（山の手入れを支える）
地域のスギ、土・雨・生ごみを敷地で回す

時間
スケルトン＆インフィル
水まわりはどのスパンにも

スケルトン＆インフィル
3ｍスパンの架構（固定）と間仕切り・家具（可変）
今／定員が変わる／学童・地域の場

光の筋と架構　1/20
2枚の梁のあいだ180の上に乳白ガラス

接合部（2枚の梁で柱を挟む）

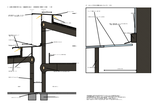

inspired by

Asilo Nido Iride
Mario Cucinella Architects・Guastalla・2015
→ 梁の列が並ぶ長細い本館と、外に付く付属の建物

Tamedia
坂茂・Zürich・2013
→ 梁の端の楕円の開と、それを貫く楕円の桁

レイモンド研究こども園
キノアーキテクツ・琵琶・2026
→ 室内に木を立てる（ホールの北山杉）

KAIT工房
石上純也・厚木・2008
→ 杭の配列と、見る向きで景色が変わる並び


認定こども園ちみどり
ほりゅうウッドスタジオ・須賀川・2026
→ 四どおりの二重の縁側、遊具を置かない地形の園庭

仙台湾の園舎
環境デザイン研究所
→ 擂鉢のネット、キャットウォーク、ニッチ


Waldorf School of the Peninsula
California
→ 遊戯室の切り株

西館2階＝職員の側（休憩室・ぐったり休憩・会議室・更衣）。こどもから離れて休む

西館2階平面図 1/100　職員の側

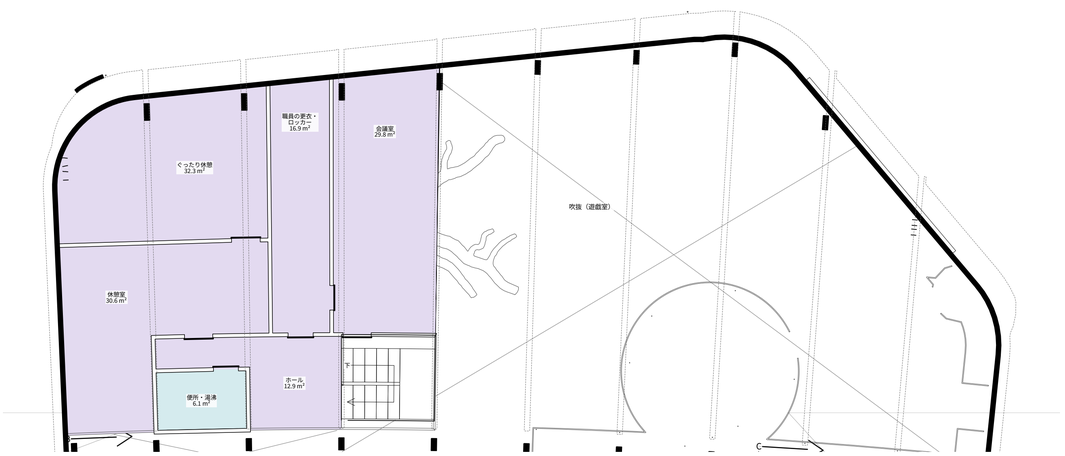

断面図B　海峡 1/100　南の入口・キッチン・2階・すき間・本館・縁側

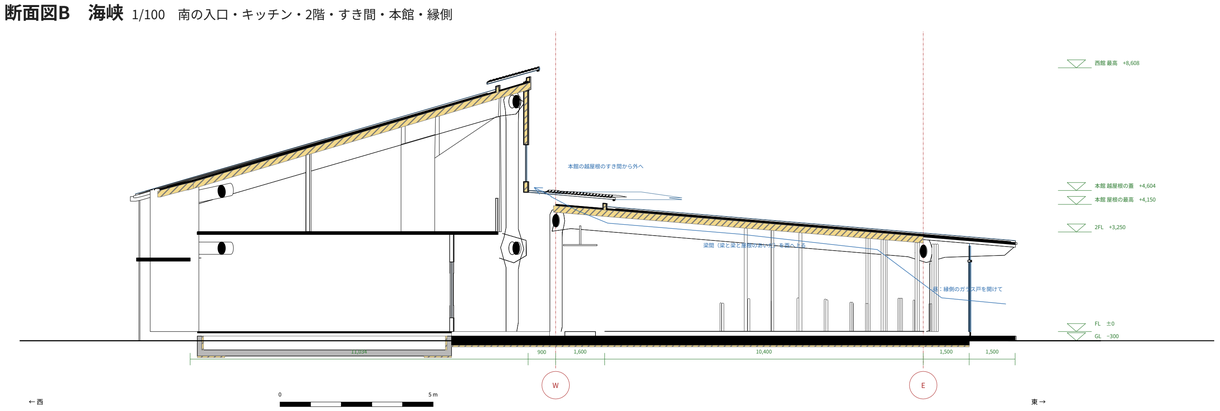

［割付の注記］フォーカス：木造・パッシブ（床下・越屋根・光の筋）で空調を補う。屋根材型の太陽光と蓄電池、資源のめぐり、時間（S&I）　／　目に入る順：断面C 1/50（昼と夏の夜の風、光の筋、床下）→ 運転表と4つの配慮 → 断面B → 2階（職員の側）