
育ち舎　南の入口まわり（キッチン・遊戯室の入り口・窓口の帯・静養室・医務）　ラフ

1/100（A3）　2026-10-29　架構の番号は南から（架構kは南の妻から3(k−1) m、スパンkは架構kとk+1のあいだ）。面積（芯々、概算）：キッチン 60 m²　遊戯室の入り口（遊戯室に含める） 22 m²　窓口の帯 5.4 m²　静養室 8.6 m²　医務 22 m²

キッチン

- 汚染作業区域（検収・下処理・洗浄）
- 非汚染作業区域（加熱・盛り付け・配膳）
- 手洗い（足踏みかセンサーの水栓）
- 食材の流れ（検収→下処理→加熱→盛り付け→配膳口）
- 下膳の流れ（返却口→下膳台→シンク→食洗機→消毒保管庫→盛り付け）
- 腰の高さの仕切り（区域の境）。点線はフードの範囲

キッチンの作り（11-01）：大量調理施設衛生管理マニュアル（厚労省、1回300食以上が対象）の考え方に沿う。約115食で対象外だが、乳幼児・離乳食・アレルギー食があるので従う。部屋で分けず、床の色と腰の高さの仕切りで区域を分け、流れを逆戻りさせない。
床はドライの床（回転釜の前だけ排水の溝）。背の高い物（冷凍冷蔵庫・消毒保管庫・食洗機・スチコン）は西の窓・東と北のガラスの前に置かない。
消毒保管庫は洗浄と非汚染の区域の境で両側から出し入れ。保存食は−20℃で2週間。保温・保冷の配膳車は東の帯の置き場（11）で配膳口から受ける。

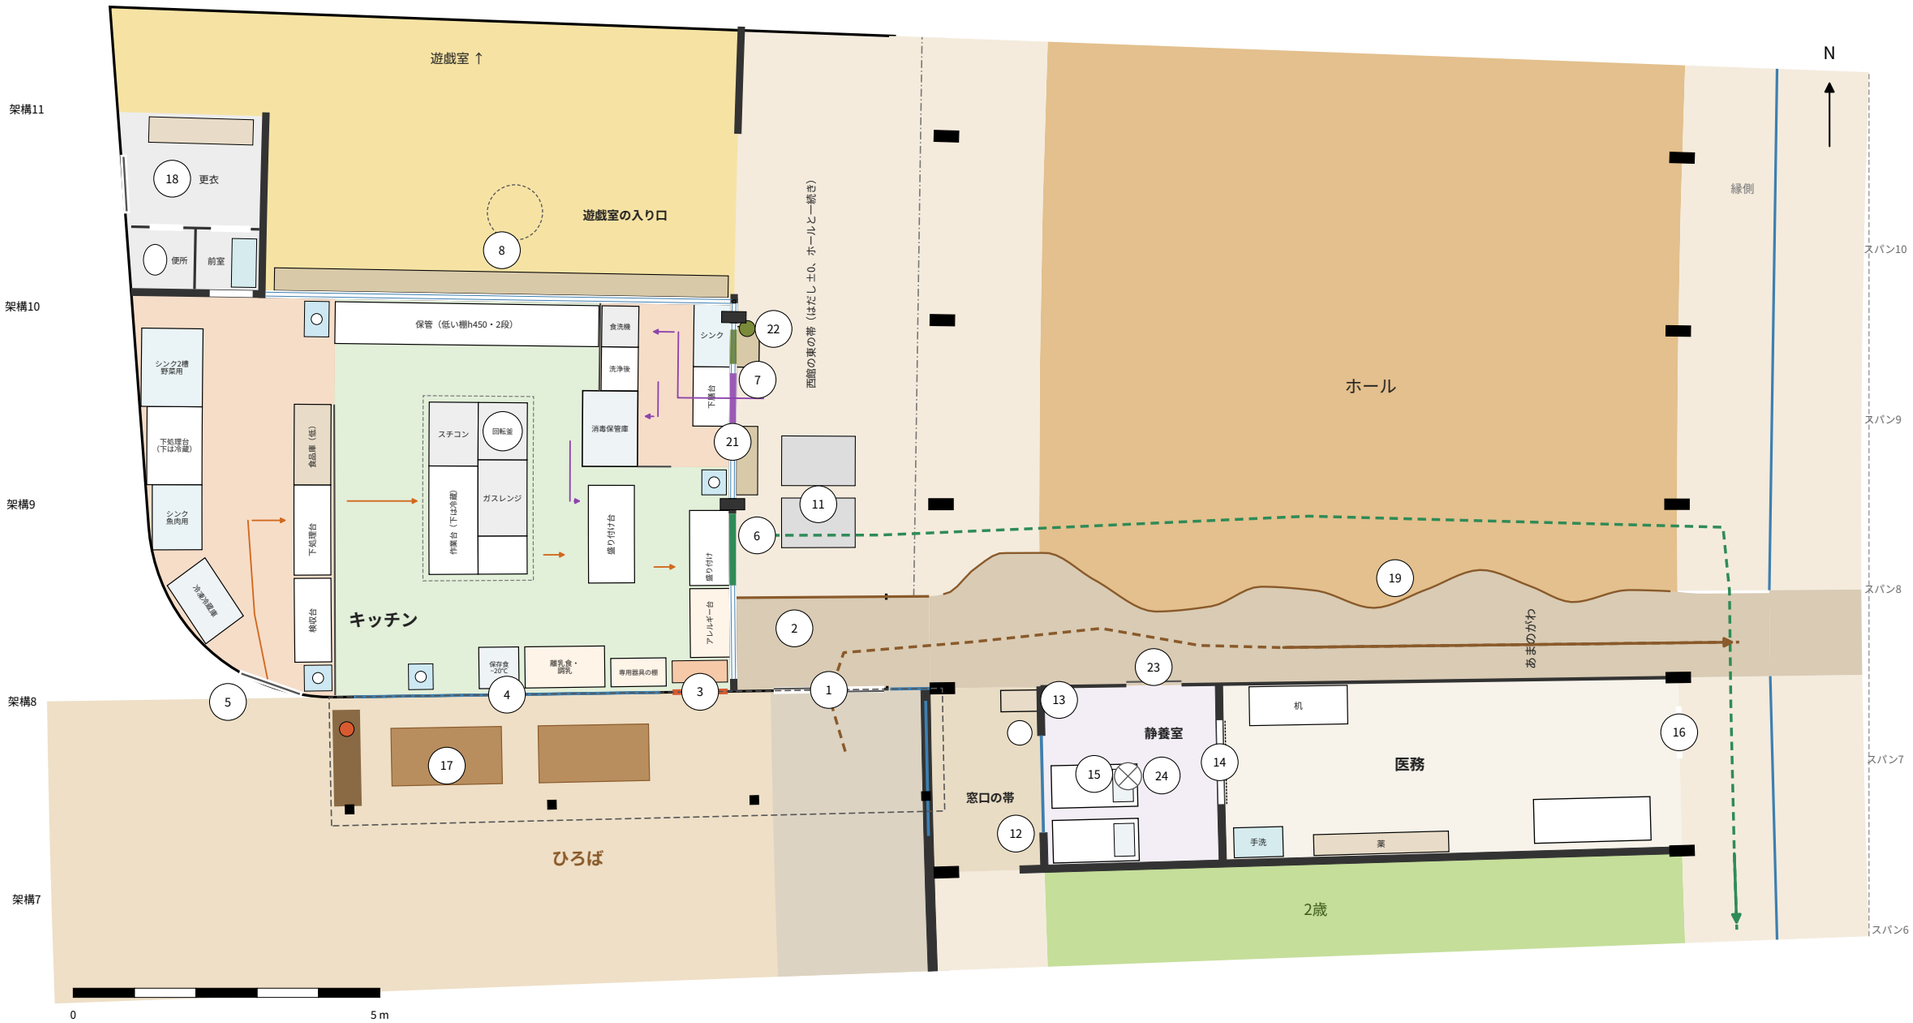

1　入口（西館の南の面、引き戸1.8）。すき間はガラス

2　あまのがわの延長（土足−150、幅1.5）。框から北は東の帯（はだし ±0）

3　「今日のごはん」の窓（子どもの高さ、中は見本の棚）

4　キッチンの南のガラス（離乳食・調乳の台と加熱が見える）

5　検収（勝手口のすぐ内側）

6　配膳口（盛り付け→ワゴン）

7　返却口（配膳口と分ける、一方通行）

8　キッチンの北のガラス（腰壁h450の上、角は方立て□50×50）と踏み台h300（3〜5歳が作業台越しに見る）

11　配膳のワゴン置き場（東の帯）

12　窓口の帯（受付・見守り、西の窓から小径の出口・手水・入口が見える。机仕事はスパン11の記録・連絡の机）

13　おはようの窓口（低いカウンター、あまのがわの広い淵に向く）

14　静養室と医務のあいだの戸（保健師が看る）

15　静養室（こども用ベッド×2、戸で閉じ換気は別、窓口の帯から室内窓h0.9〜2.0）

16　医務の戸（内縁側から、先生が子どもを連れてくる）

17　下屋の下の縁台とお茶の棚（電気ポットはh1100の棚の上：給湯ロック・転倒湯もれ防止・蒸気レス・マグネットプラグ）

18　調理の職員の更衣・便所・前室（外から直接：西の面の戸 → 更衣 → 前室 → キッチン）

19　あまのがわの北の縁（ホールとの段150、框は曲線の杉。本館係の案4、飛び石は無し）

21　キッチンの東の面：腰壁h450の上を2階の床の下までガラス（二本線）。ホールの側に踏み台h300。破線の円は天井扇φ0.9

22　生ごみの受け取り台（返却口の隣、東の帯の側h500。3〜5歳のコンポスト当番がふた付きのバケツを受け取る）

23　静養室の戸（あまのがわへ、お迎えの保護者が迎えに来る）

24　静養室の換気扇（天井から真上へ、屋根の上の換気の頭。給気は戸の下から）

--- 緑：配膳の保育士（配膳口 → 東の帯 → ホール → 内縁側で先生があまのがわを渡る（段150、両側に手すり）→ 南の保育室）。--- 茶：3〜5歳（入口 → あまのがわ → 縁側、おはようの窓口の前を通る）。キッチンは検収→下処理→加熱→盛り付け→配膳口、返却口→洗浄→消毒保管庫→盛り付け・保管の一方通行（区域と流れは左上）。
西館の東の帯とすき間は、エキスパンションをはさんでホールと一続き（はだし ±0）。本館の西の壁はホールの範囲では開く。スパン10 は遊戯室のもう一つの入り口（10-29 夜、ユーザー：はれのまは無くす。中身はこれから）。記念日のお祝いはホール、延長保育は玄関に近い保育室（案）。