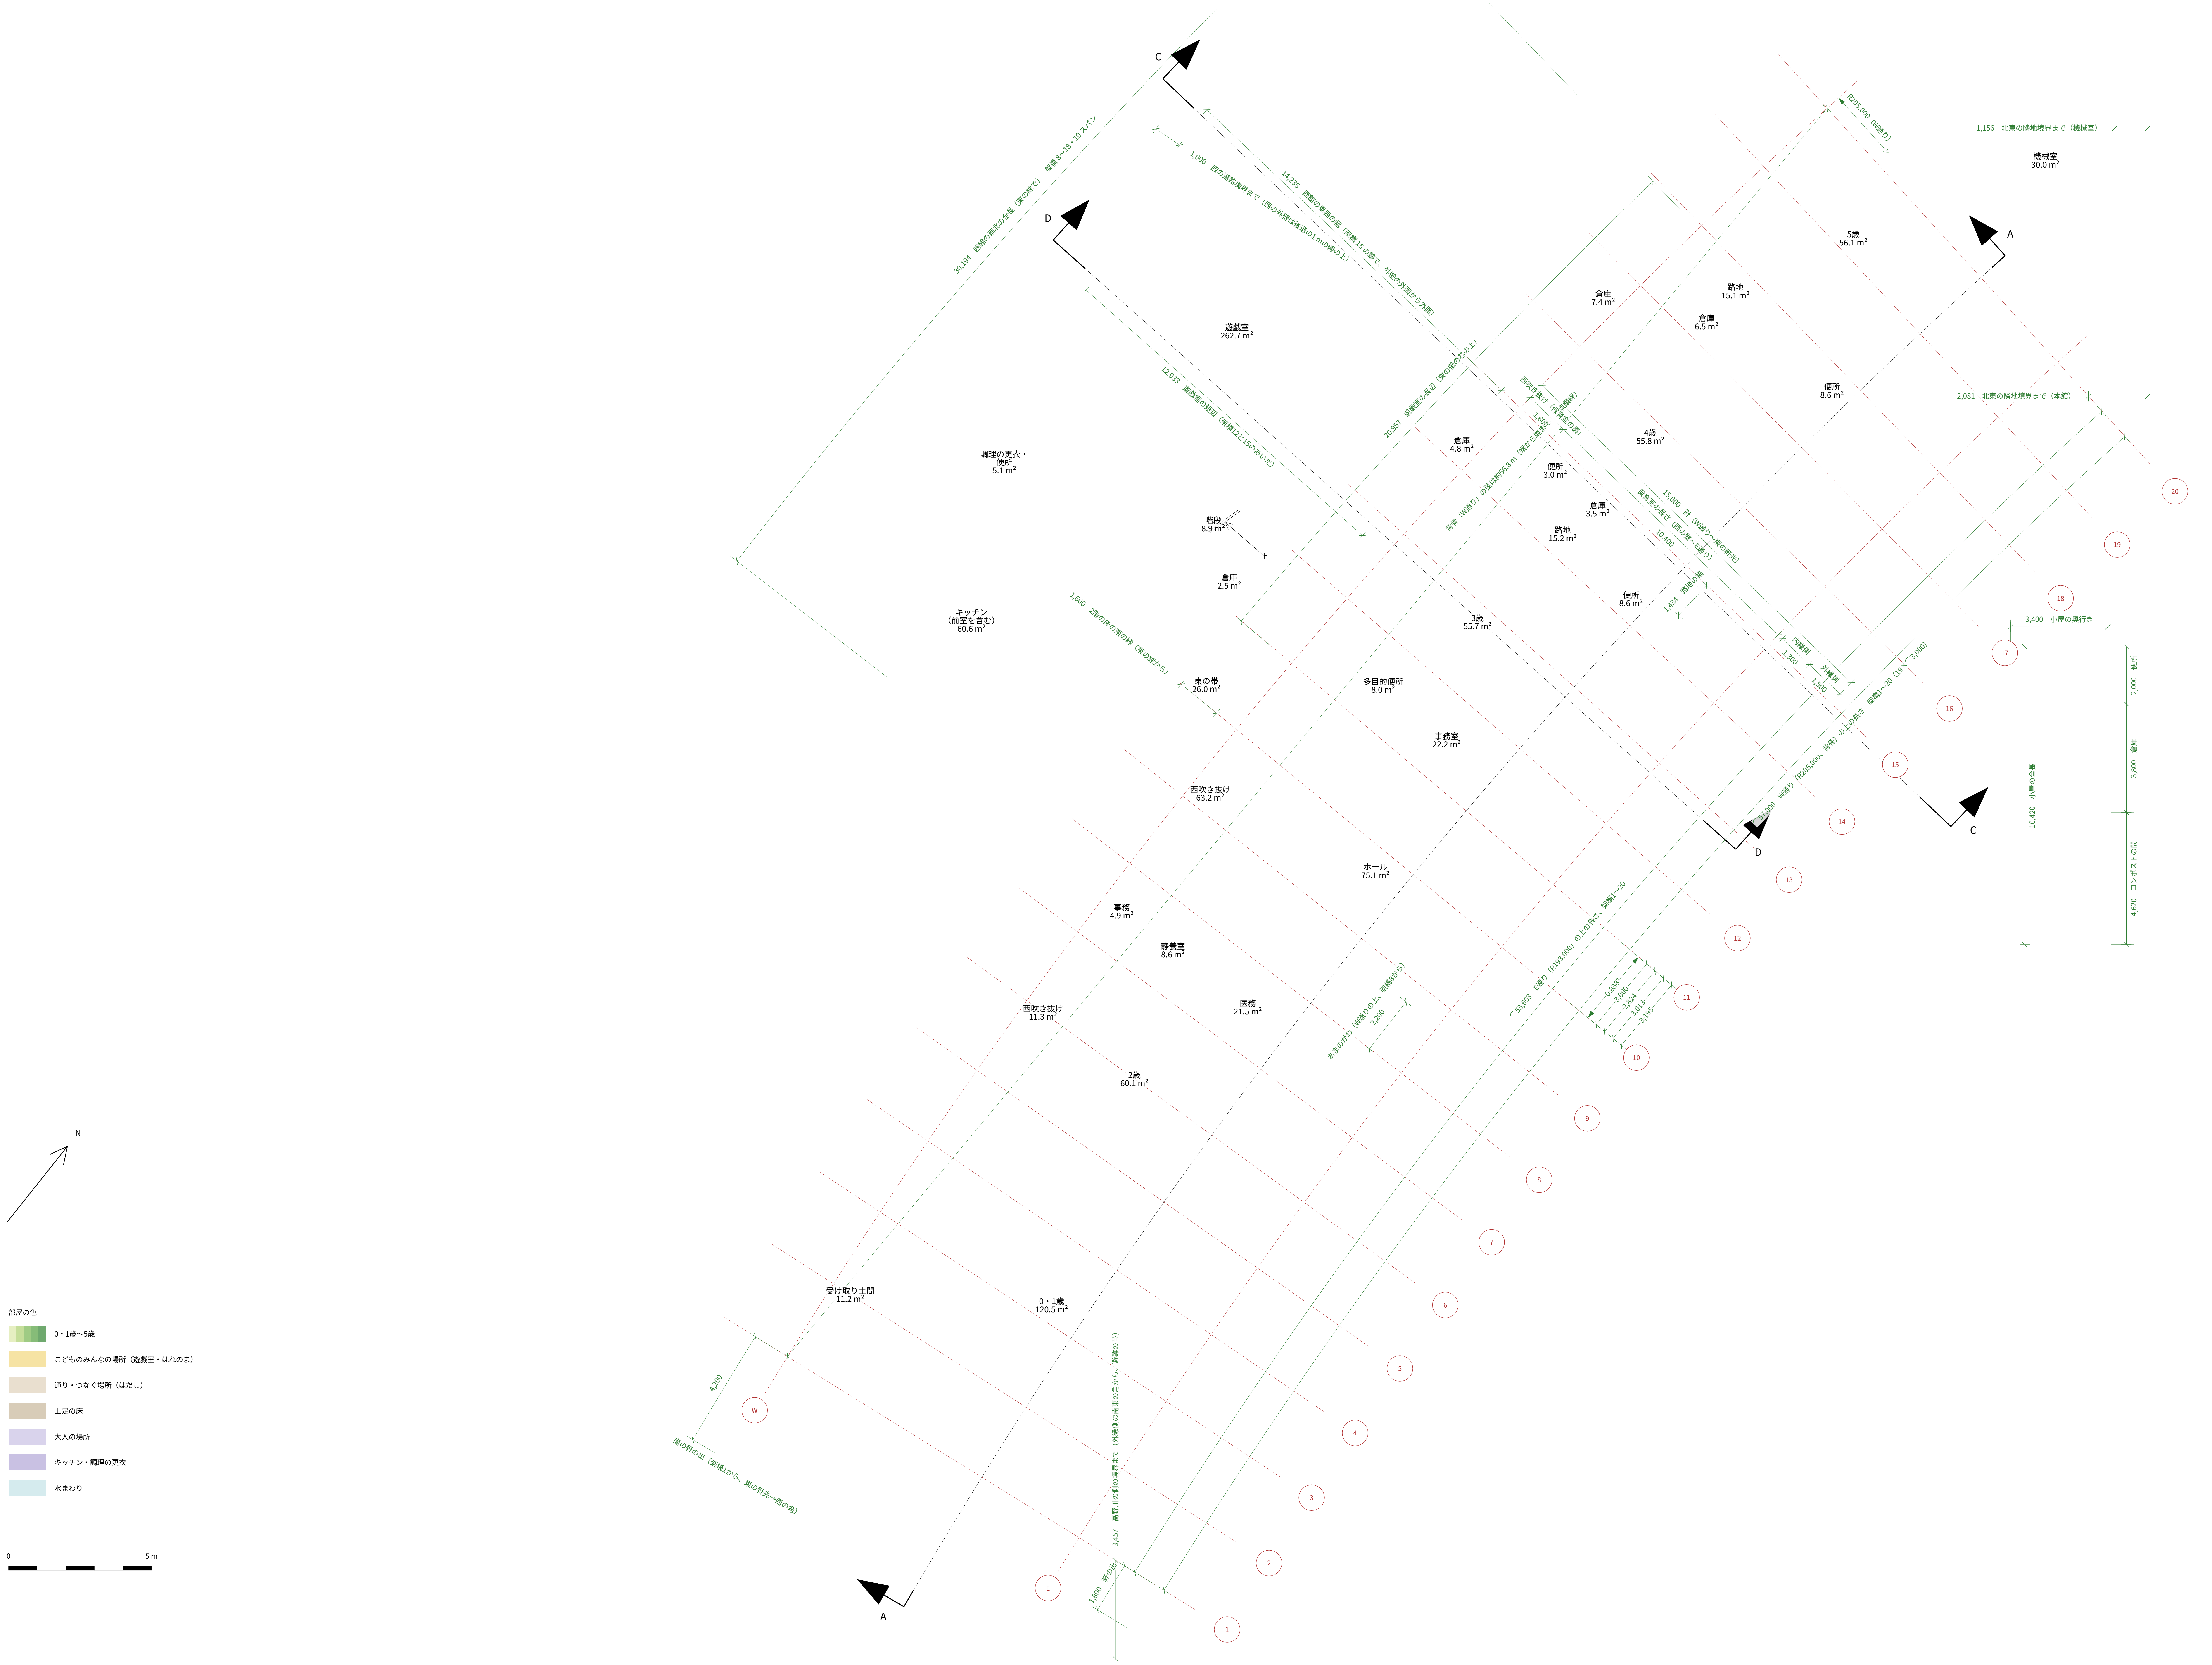
C
C
D
D
A
A
30,194　西館の南北の全長（東の線で）　架構 8〜18・10 スパン
1,000　西の道路境界まで（西の外壁は後退の1mの線の上）
14,235　西館の東西の幅（架構 15 の線で、外壁の外面から外面）
12,933　遊戯室の短辺（架構12と15のあいだ）
20,957　遊戯室の長辺（東の壁の芯の上）
西吹き抜け（保育室の裏）
1,600　（端から端まで）
背骨（W通り）の弦は約56.8 m（端から端まで）
15,000　計（W通り〜東の軒先）
保育室の長さ（西の壁〜E通り）
10,400
1,434　路地の幅
内縁側
1,300
外縁側
1,500
R205,000（W通り）
1,156　北東の隣地境界まで（機械室）
2,081　北東の隣地境界まで（本館）
3,400　小屋の奥行き
10,420　小屋の全長
2,000　便所
3,800　倉庫
4,620　コンポストの間
⌒57,000　W通り（R205,000、背骨）の上の長さ、架構1〜20（19×⌒3,000）
⌒53,663　E通り（R193,000）の上の長さ、架構1〜20
0.838°
3,000
2,824
3,013
3,195
あまのがわ（W通りの上、架構8から）
2,200
1,600　2階の床の東の縁（東の線から）
4,200
南の軒の出（架構1から、東の軒先→西の角）
3,457　高野川の側の境界まで（外縁側の南東の角から、避難の帯）
1,800　軒の出
遊戯室
262.7 m²
調理の更衣・
便所
5.1 m²
階段
8.9 m²
上
倉庫
2.5 m²
キッチン
（前室を含む）
60.6 m²
機械室
30.0 m²
5歳
56.1 m²
倉庫
7.4 m²
路地
15.1 m²
倉庫
6.5 m²
便所
8.6 m²
倉庫
4.8 m²
4歳
55.8 m²
便所
3.0 m²
倉庫
3.5 m²
路地
15.2 m²
便所
8.6 m²
3歳
55.7 m²
東の帯
26.0 m²
多目的便所
8.0 m²
事務室
22.2 m²
西吹き抜け
63.2 m²
ホール
75.1 m²
事務
4.9 m²
静養室
8.6 m²
西吹き抜け
11.3 m²
医務
21.5 m²
2歳
60.1 m²
受け取り土間
11.2 m²
0・1歳
120.5 m²
1
2
3
4
5
6
7
8
9
10
11
12
13
14
15
16
17
18
19
20
W
E
N
部屋の色
0・1歳〜5歳
こどものみんなの場所（遊戯室・はれのま）
通り・つなぐ場所（はだし）
土足の床
大人の場所
キッチン・調理の更衣
水まわり
0
5 m