
平面図　2階（西館）　2FL+1000 で切断　1/100

高野川を下に（配置図と同じ向き）。1階の平面図と同じ位置・同じ縮尺（重ねると上下が合う）。西館の外（本館の屋根・園庭・周り）は上から見た見えがかり。二点鎖線は屋根の外形（軒の線）。部屋の幅は壁の芯から芯

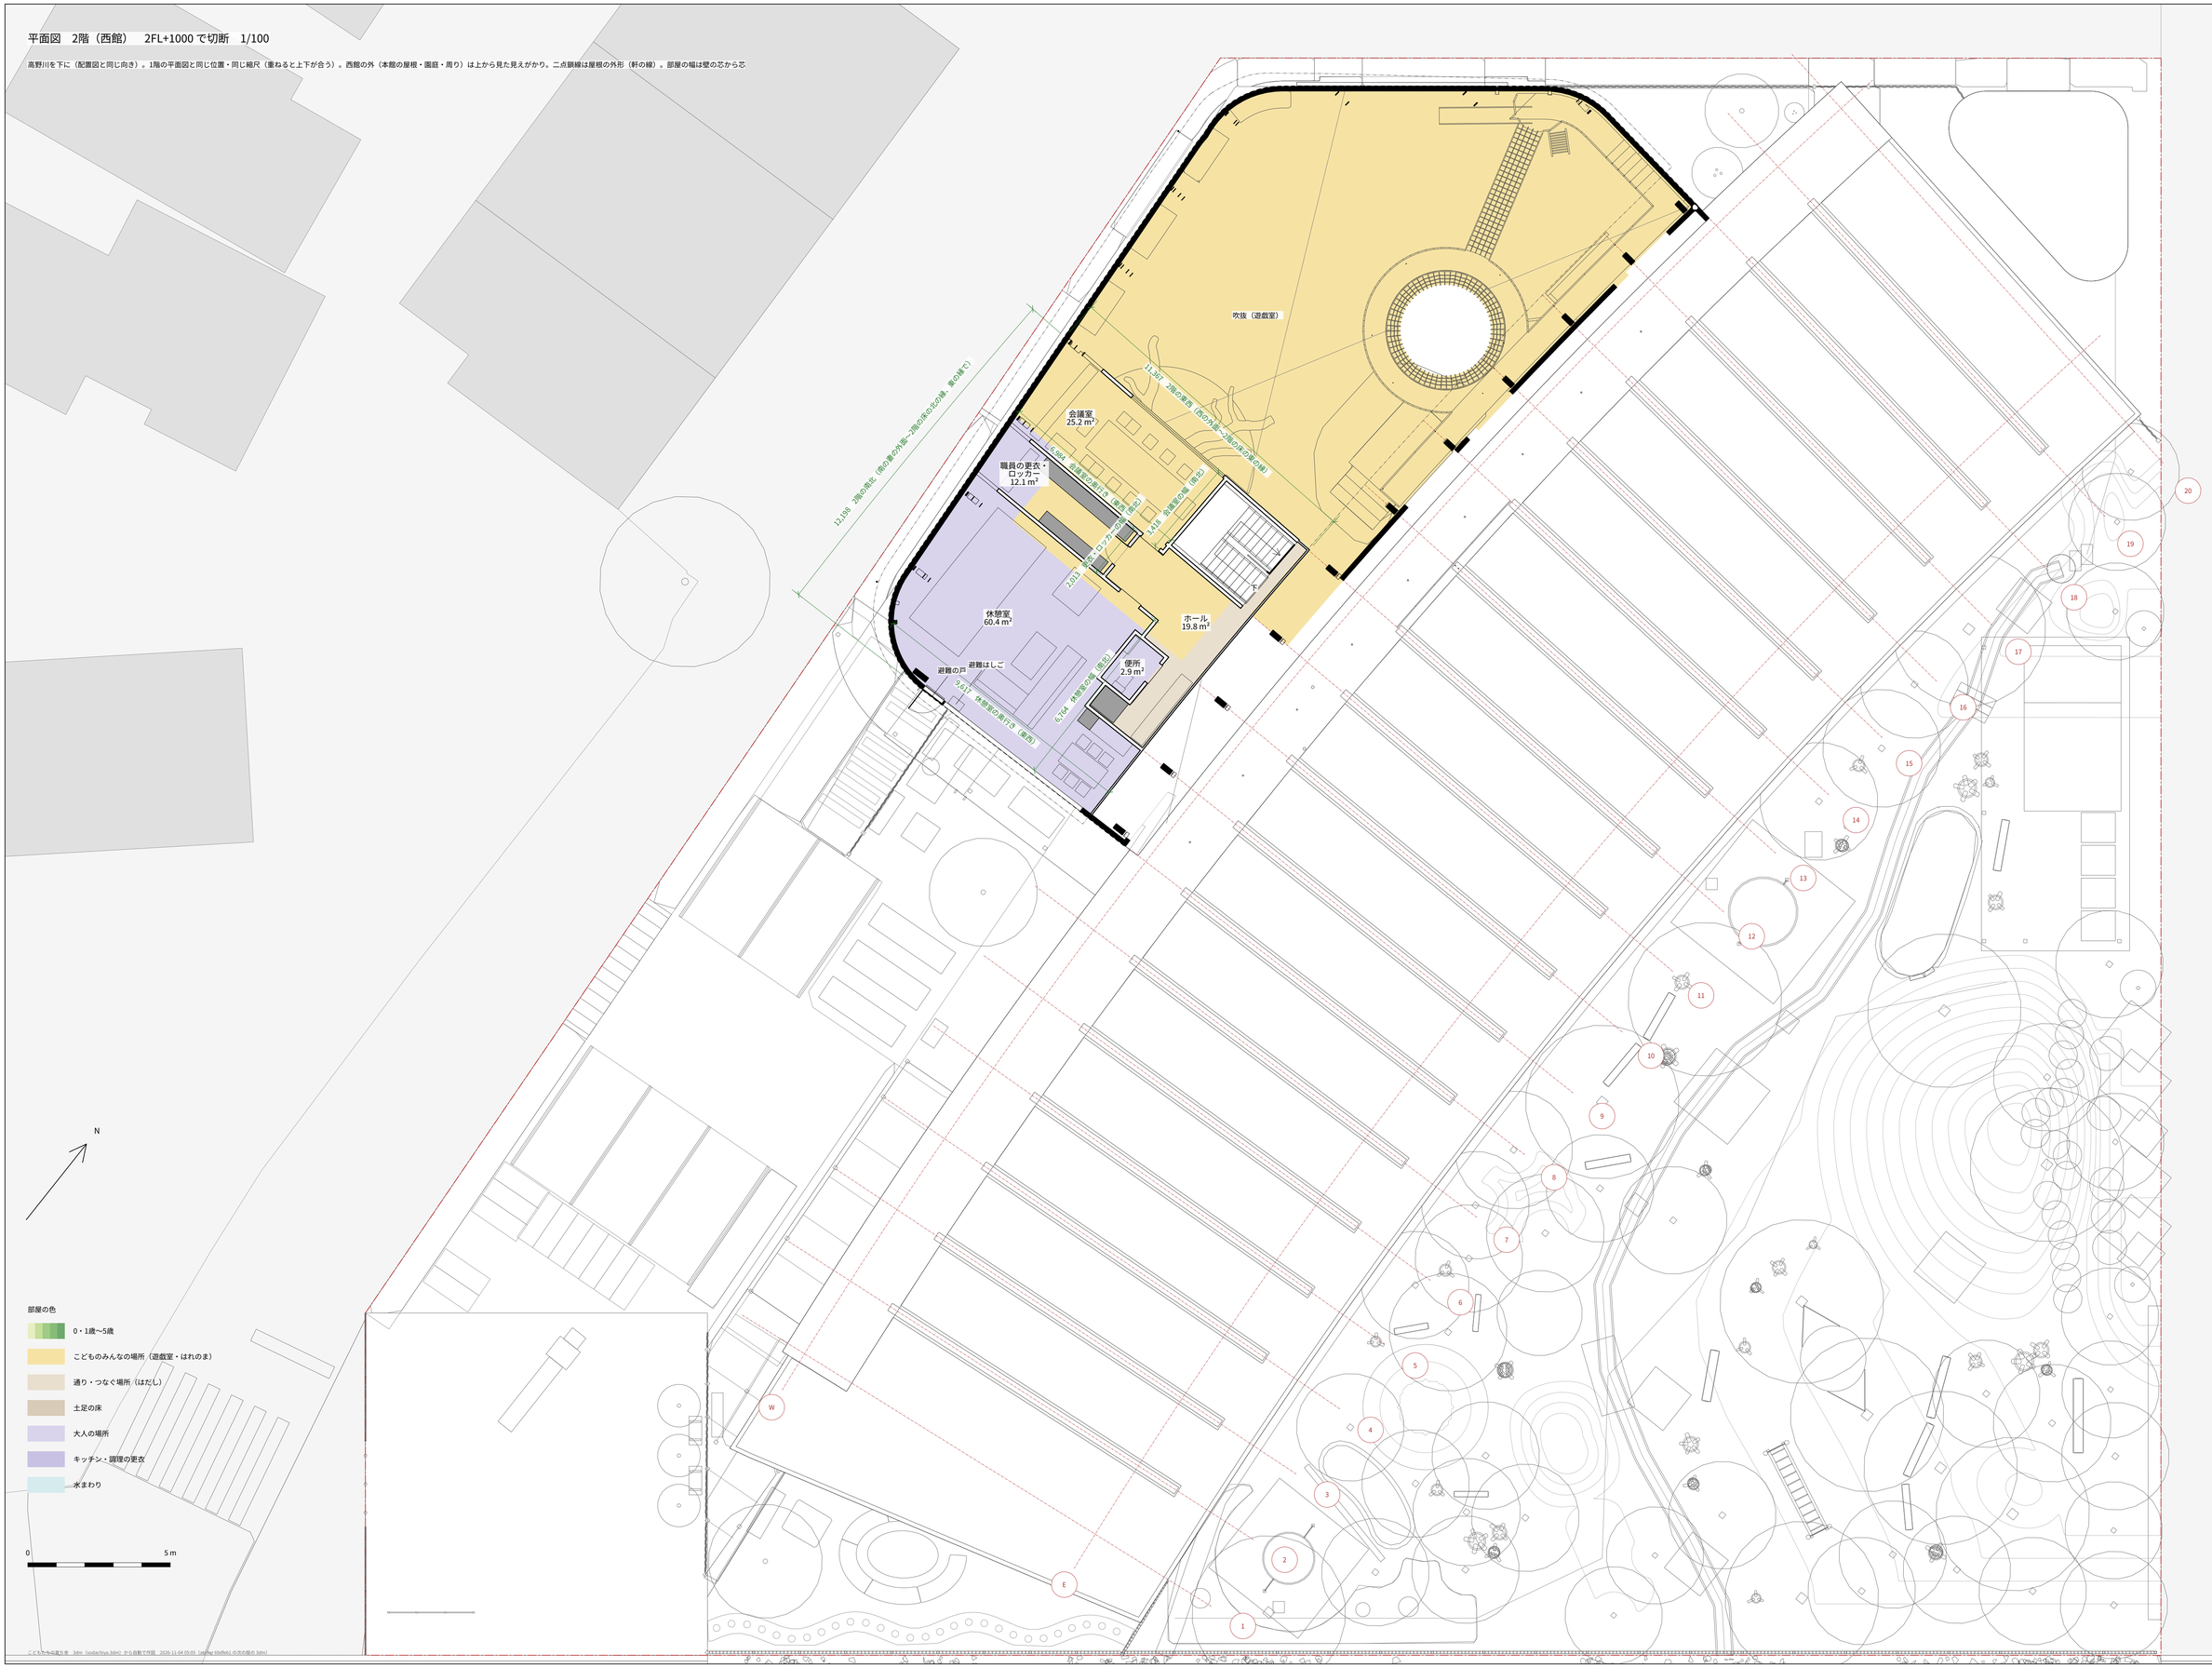

こどもちの森北舎　3dm（ondaichiya.3dm）から自動で作図　2026-11-04 05:05（ondai-03dfm01 の次の版の 3dm）