
育ち舎　南の入口まわり（キッチン・はれのま・事務・医務）　ラフ

1/100（A3）　2026-10-21　架構の番号は南から（架構 k は南の妻から 3(k−1) m、スパン k は架構 k と k+1 のあいだ）。面積（芯々、概算）：キッチン 58 m²　はれのま 31 m²　事務（スパン7 の西）13 m²　医務 22 m²＋内縁側

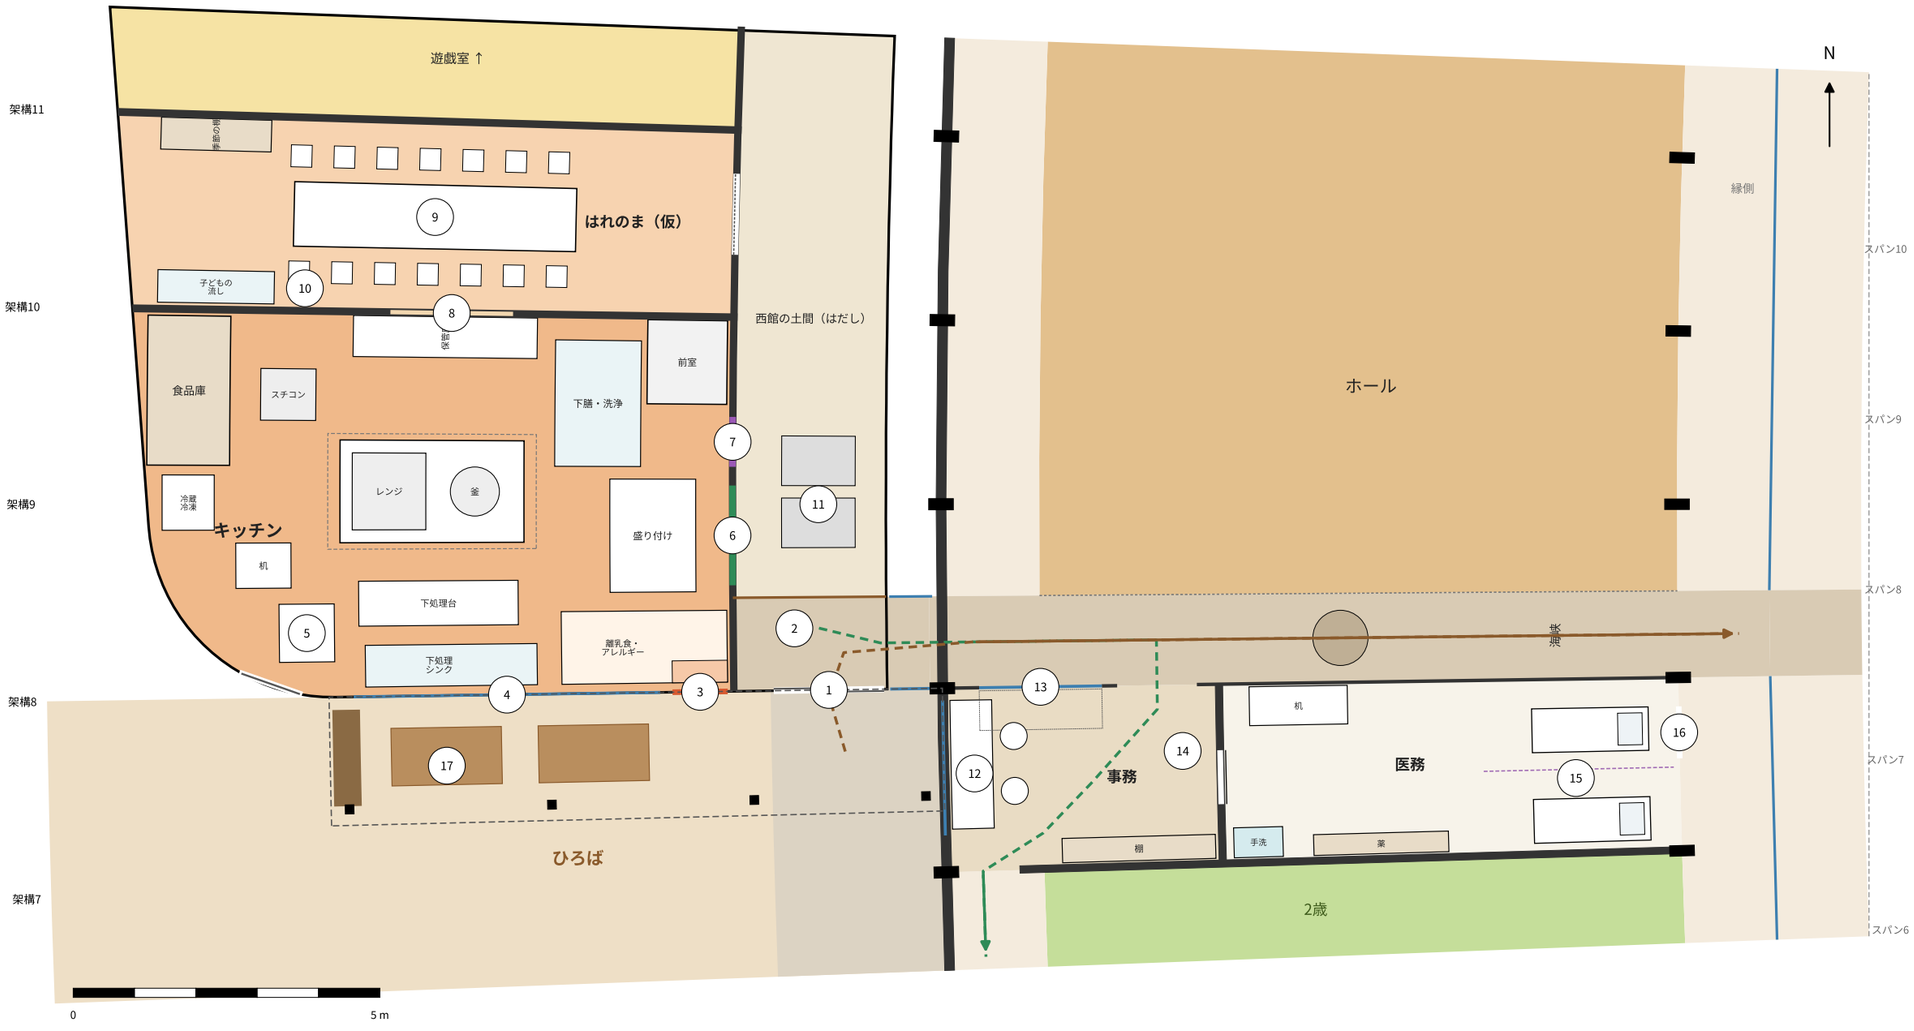

1　入口（西館の南の面、引き戸 1.8）。すき間はガラス

2　海峡の延長（土足 −150）。框から北ははだしの土間

3　「今日のごはん」の窓（子どもの高さ、中は見本の棚）

4　キッチンの南のガラス（下処理が見える）

5　検収（勝手口のすぐ内側）

6　配膳口（盛り付け → ワゴン）

7　返却口（配膳口と分ける、一方通行）

8　見える台所（はれのまへの受け渡しの窓）

9　はれのまの大きな机（10〜12 人）

10　子どもの流しと調理台（食育）

11　配膳のワゴン置き場（土間）

12　事務の机（西の窓：小径の出口・手水・ひろば・入口が見える）

13　受付の窓（海峡に向く）

14　医務への戸（事務から）

15　ベッド×2（カーテンで分ける、静養・隔離）

16　医務の戸（内縁側から、先生が子どもを連れてくる）

17　下屋の下の縁台

--- 緑：配膳の保育士と 2 歳の道（海峡 → 事務を曲がりながら抜ける → 2 歳の道）。--- 茶：3〜5 歳（入口 → 海峡 → 縁側）。キッチンは 検収 → 下処理 → 加熱 → 盛り付け → 配膳口、返却口 → 洗浄 → 保管 の一方通行。破線の箱はフード・下屋（頭上）。