平面図　1階　FL+1500 で切断　1/100

高野川を下に（配置図と同じ向き）。一点鎖線は敷地の境。二点鎖線は切断より上にある物（屋根の外形・越屋根・2階の床の縁など）。周りの道・建物は細い線

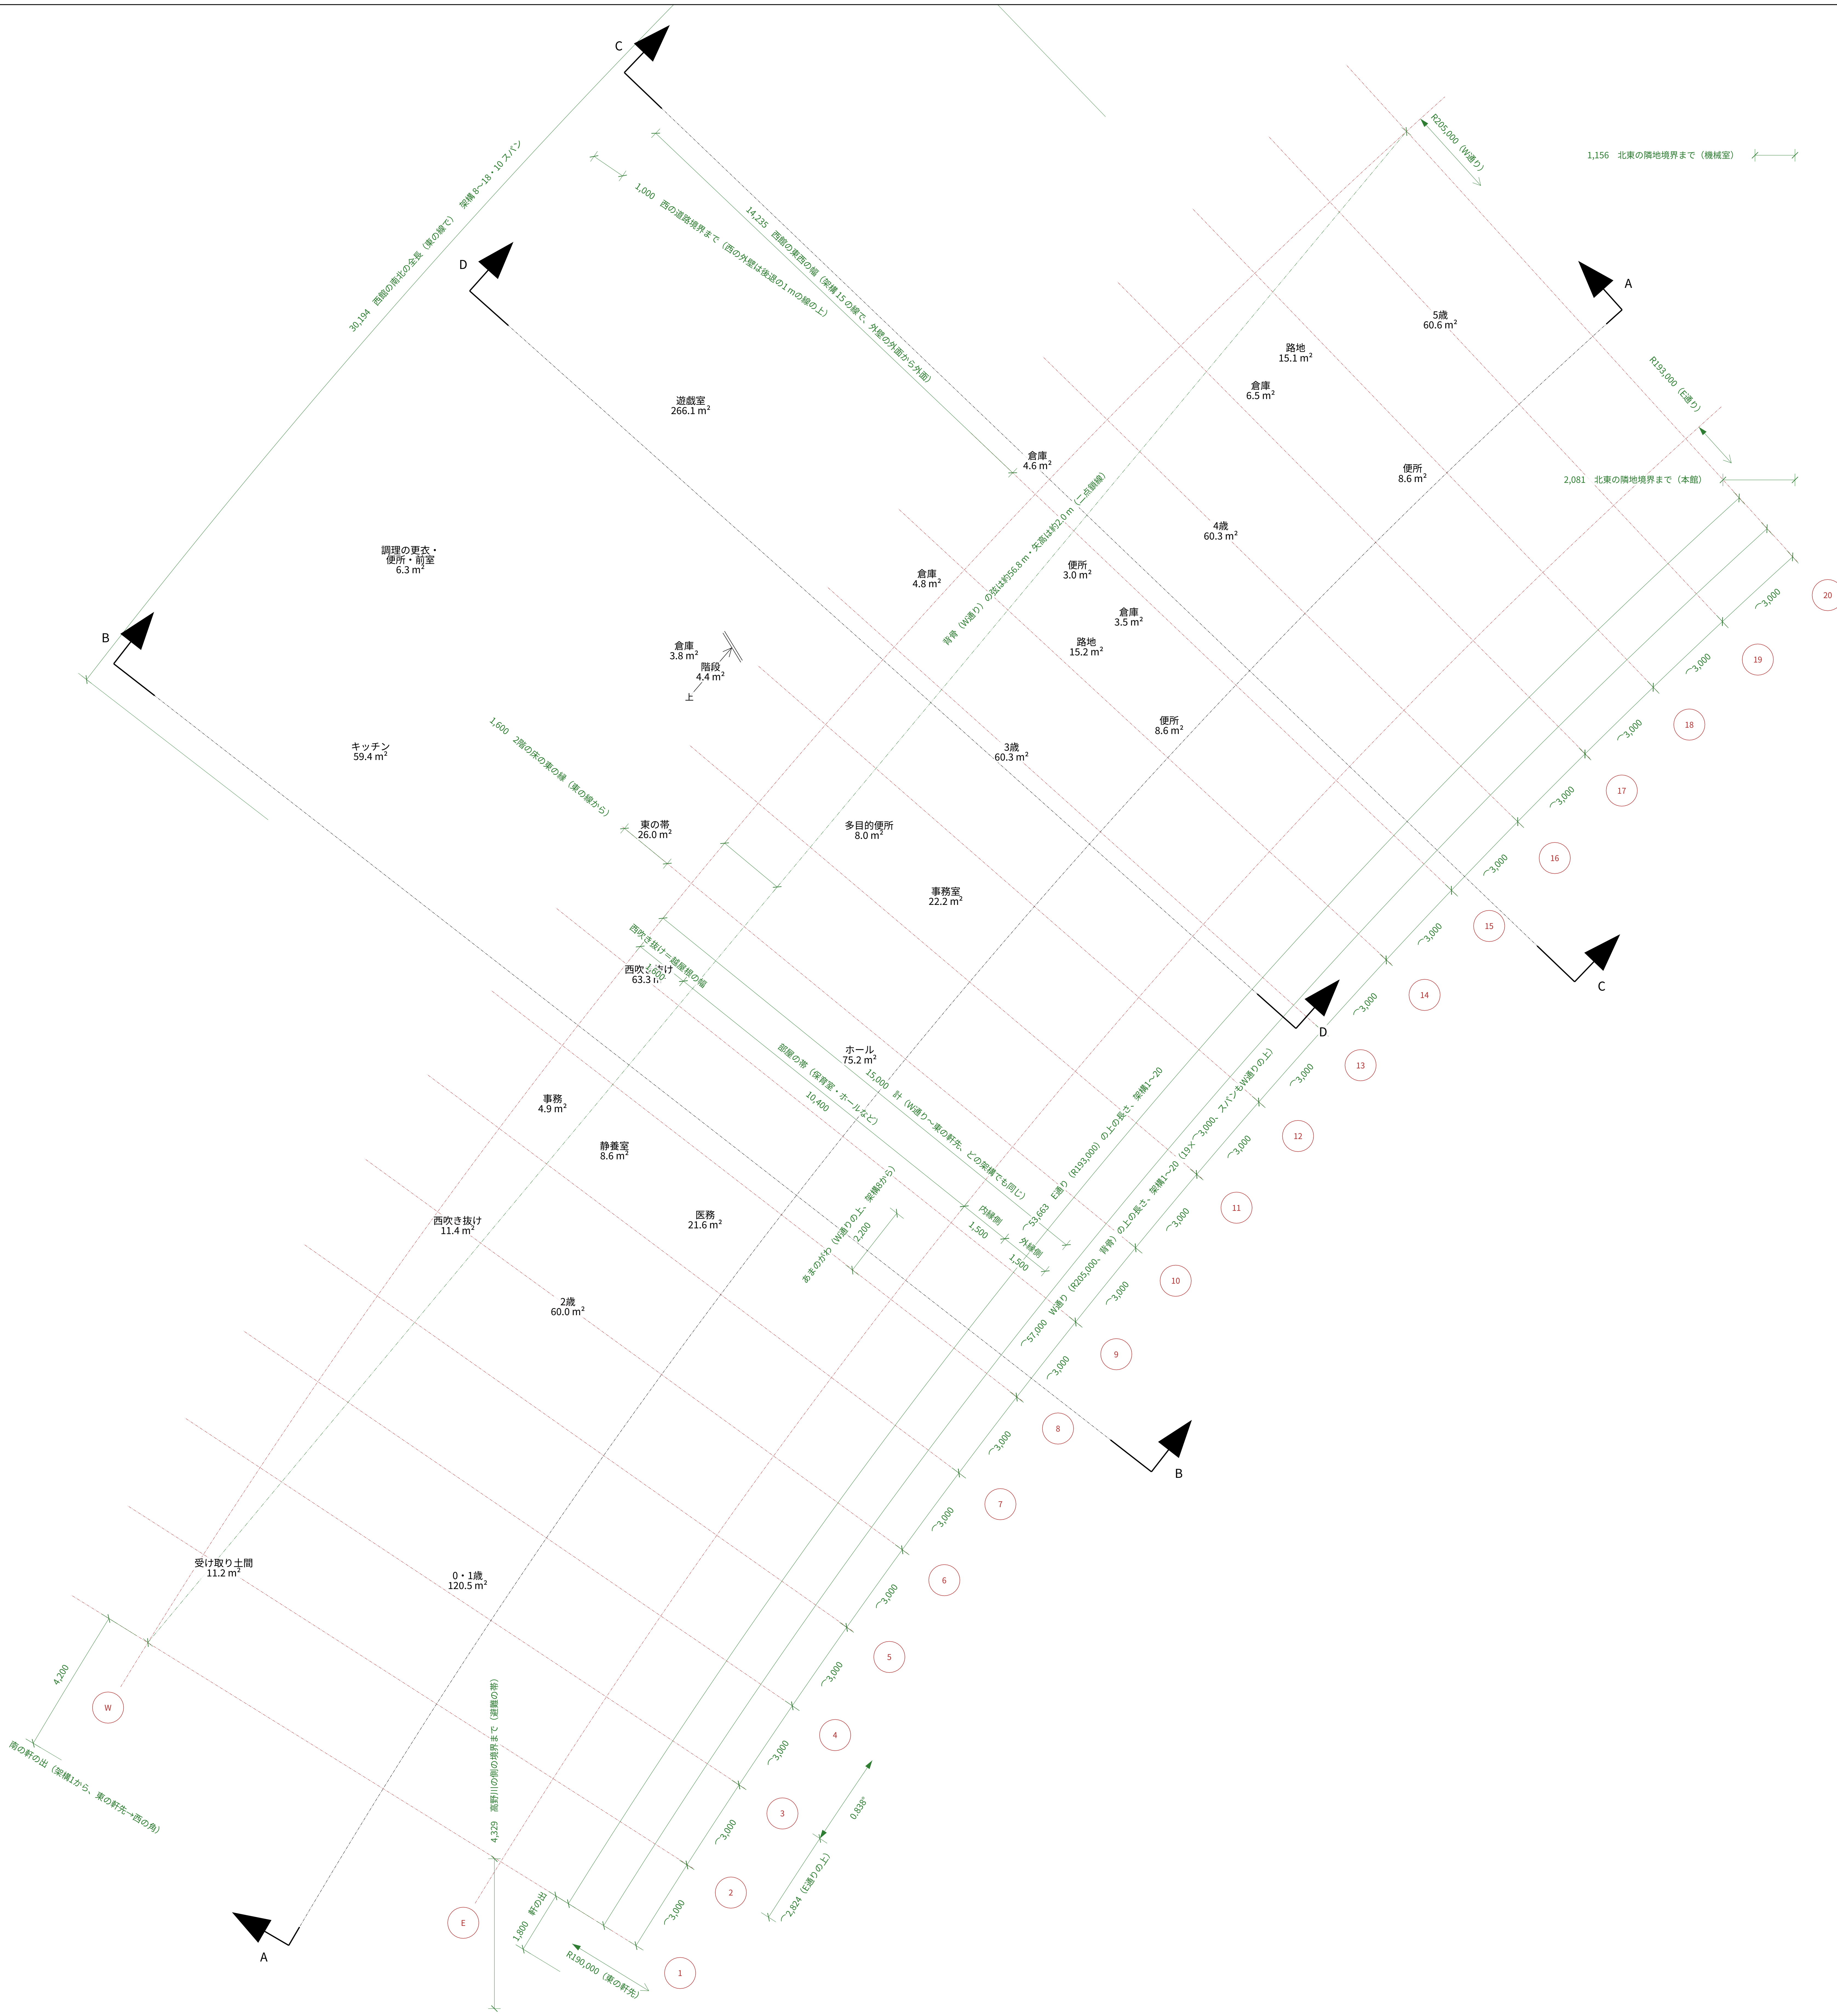
C
30,194　西館の南北の全長（東の線で）　架構 8〜18・10 スパン
1,000　西の道路境界まで（西の外壁は後退の1 mの線の上）
14,235　西館の東西の幅（架構 15 の線で、外壁の外面から外面）
R205,000（W通り）
1,156　北東の隣地境界まで（機械室）
D
A
遊戯室
266.1 m²
路地
15.1 m²
5歳
60.6 m²
倉庫
6.5 m²
R193,000（E通り）
倉庫
4.6 m²
便所
8.6 m²
2,081　北東の隣地境界まで（本館）
背骨（W通り）の弦は約56.8 m・矢高は約2.0 m（二点鎖線）
調理の更衣・
便所・前室
6.3 m²
倉庫
4.8 m²
便所
3.0 m²
4歳
60.3 m²
倉庫
3.5 m²
路地
15.2 m²
B
倉庫
3.8 m²
階段
4.4 m²
上
便所
8.6 m²
キッチン
59.4 m²
1,600　2階の床の東の縁（東の線から）
3歳
60.3 m²
東の帯
26.0 m²
多目的便所
8.0 m²
事務室
22.2 m²
C
西吹き抜け＝越屋根の幅
西吹き抜け
63.3 m²
1,600
D
ホール
75.2 m²
部屋の帯（保育室・ホールなど）
10,400
15,000　計（W通り〜東の軒先、どの架構でも同じ）
事務
4.9 m²
静養室
8.6 m²
医務
21.6 m²
西吹き抜け
11.4 m²
あまのがわ（W通りの上、架構8から）
2,200
内縁側
1,500
外縁側
1,500
⌒53,663　E通り（R193,000）の上の長さ、架構1〜20
⌒57,000　W通り（R205,000、背骨）の上の長さ、架構1〜20（19×⌒3,000、スパンもW通りの上）
2歳
60.0 m²
B
受け取り土間
11.2 m²
0・1歳
120.5 m²
4,200
W
南の軒の出（架構1から、東の軒先→西の角）
4,329　高野川の側の境界まで（避難の帯）
E
1,800　軒の出
R190,000（東の軒先）
A
⌒2,824（E通りの上）
0.838°
⌒3,000
1
2
3
4
5
6
7
8
9
10
11
12
13
14
15
16
17
18
19
20

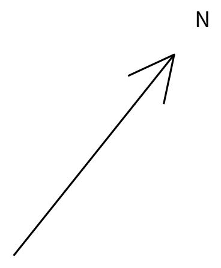

部屋の色

- 🟩 0・1歳〜5歳
- 🟨 こどものみんなの場所（遊戯室・はれのま）
- ⬜ 通り・つなぐ場所（はだし）
- 🟫 土足の床
- 🟪 大人の場所
- 🟪 キッチン・調理の更衣
- 🟦 水まわり

0　5 m

こどもたちの育ち舎　3dm（sodachiya.3dm）から自動で作図　2026-10-31 02:36（atelier 1384853 の次の版の 3dm）