
平面図　1階　FL+1500 で切断　1/100

高野川を下に（配置図と同じ向き）。一点鎖線は敷地の境。二点鎖線は屋根の外形（軒の線）。周りの道・建物は細い線。スパンの寸法はスパン10だけ：庭の側に建物に近い順にE通りの上の弧長／W通りの上の弧長／放射の線のあいだの角度、道の側に西館の西の外面の上の弧長
長手の全体は外がW通り（背骨）、内がE通りの上の弧長。二点鎖線の寸法は背骨（W通り）の弦。寸法はmm

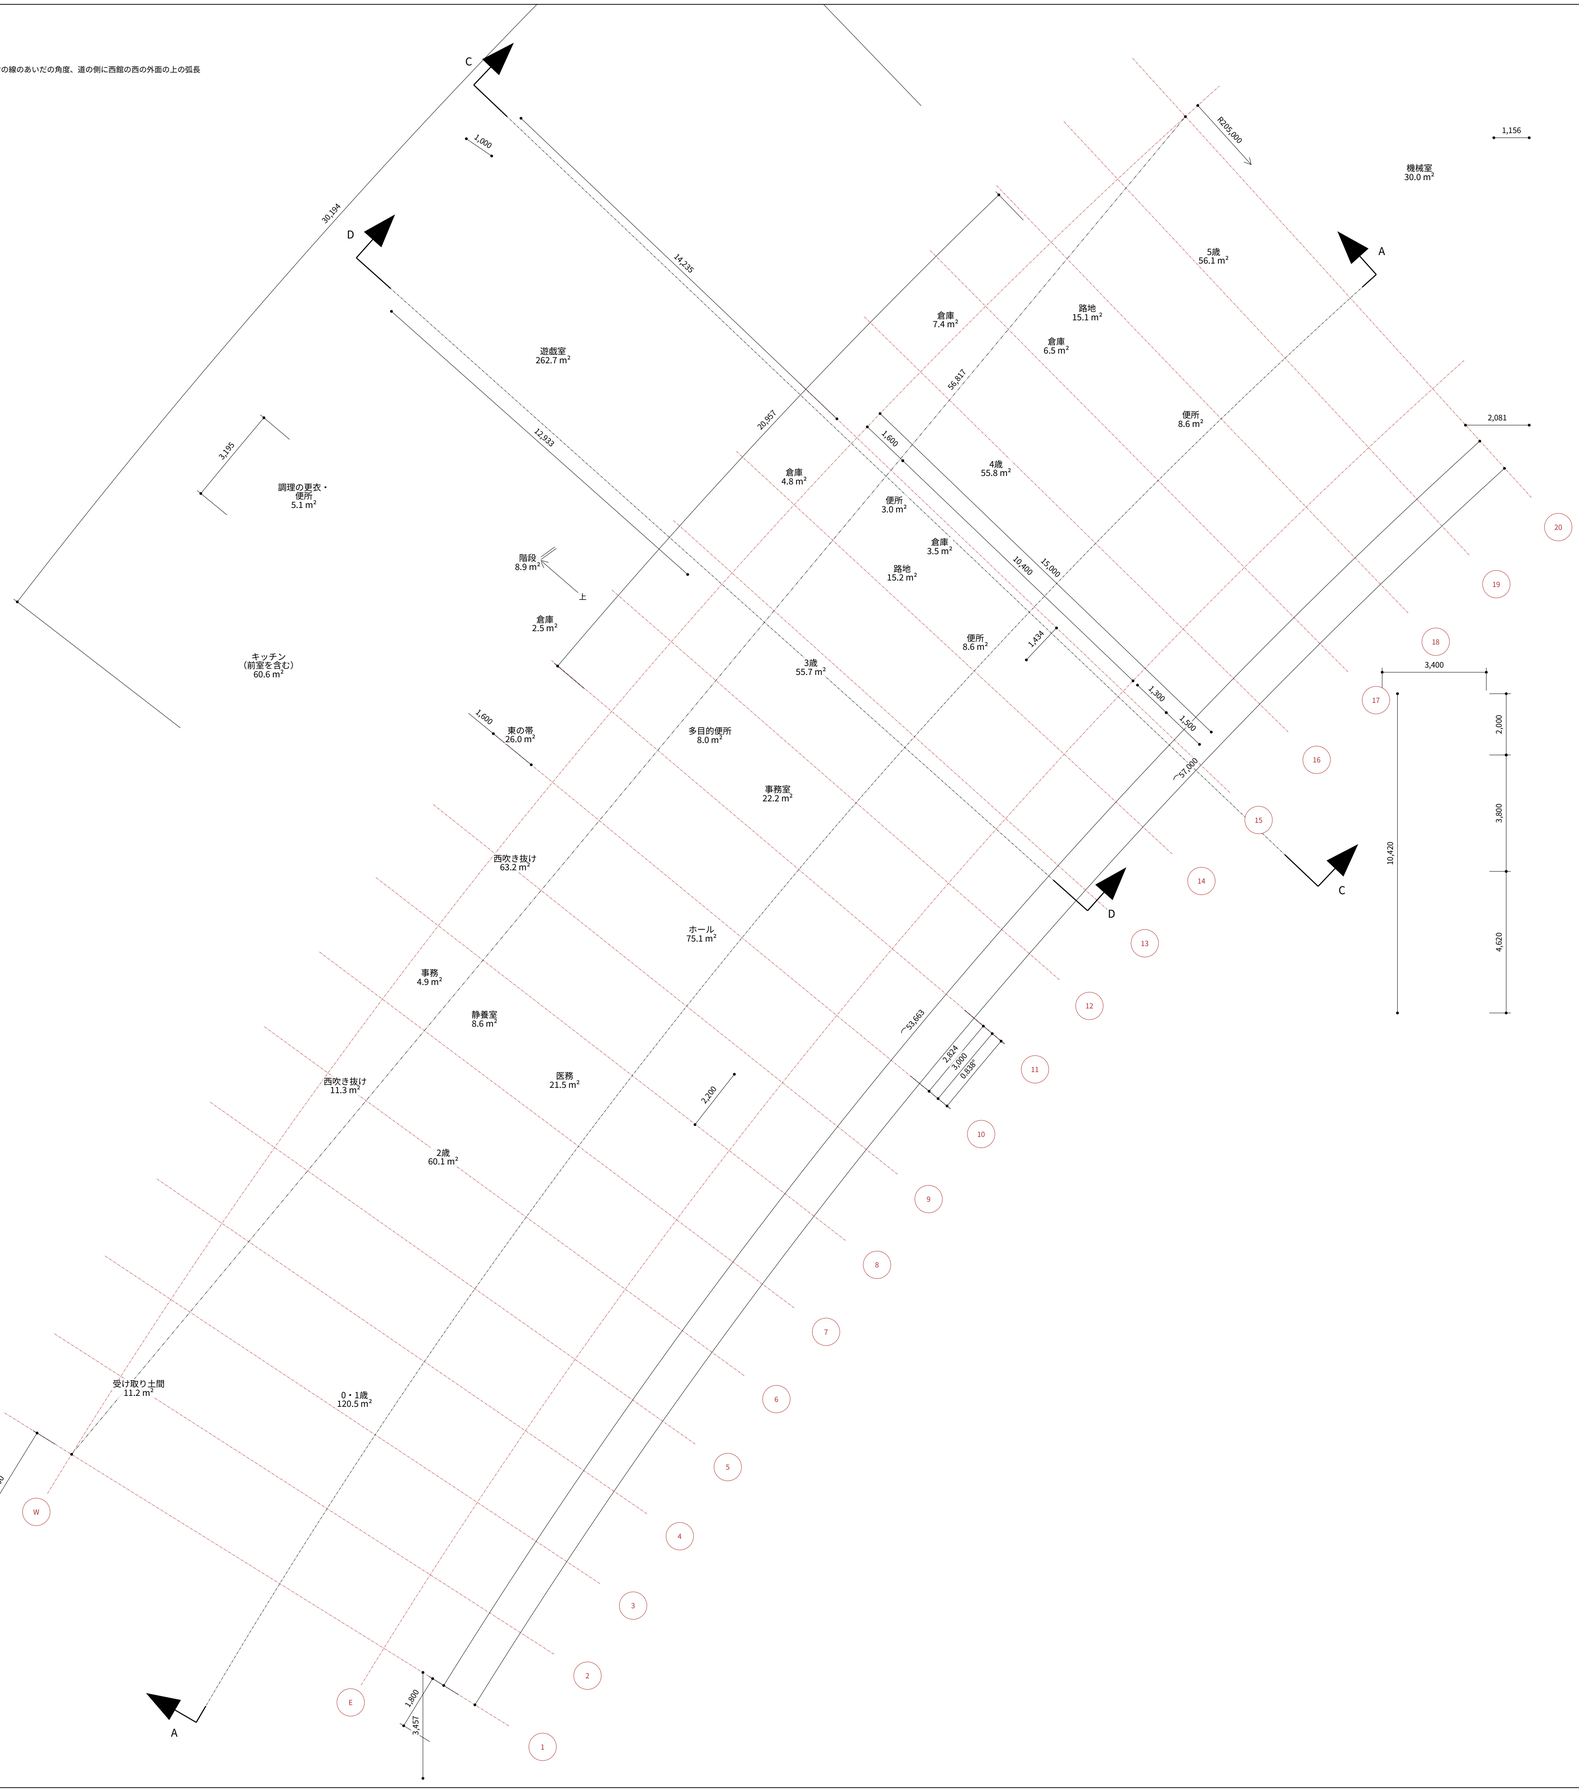

N

部屋の色

- 0・1歳〜5歳
- こどものみんなの場所（くすのきひろば・はれのま）
- 通り・つなぐ場所（はだし）
- 土足の床
- 大人の場所
- キッチン・調理の更衣
- 水まわり

0　5 m