
育ち舎　みなみのさんかく（乳児の園庭、0〜2 歳）　たたき台 1

平面 1/50・断面 1/50（A2）　2026-10-22　寸法 data/minami.json　図 scripts/minami01.py　3dm は外構の取り込み用ファイルのレイヤー 78・79

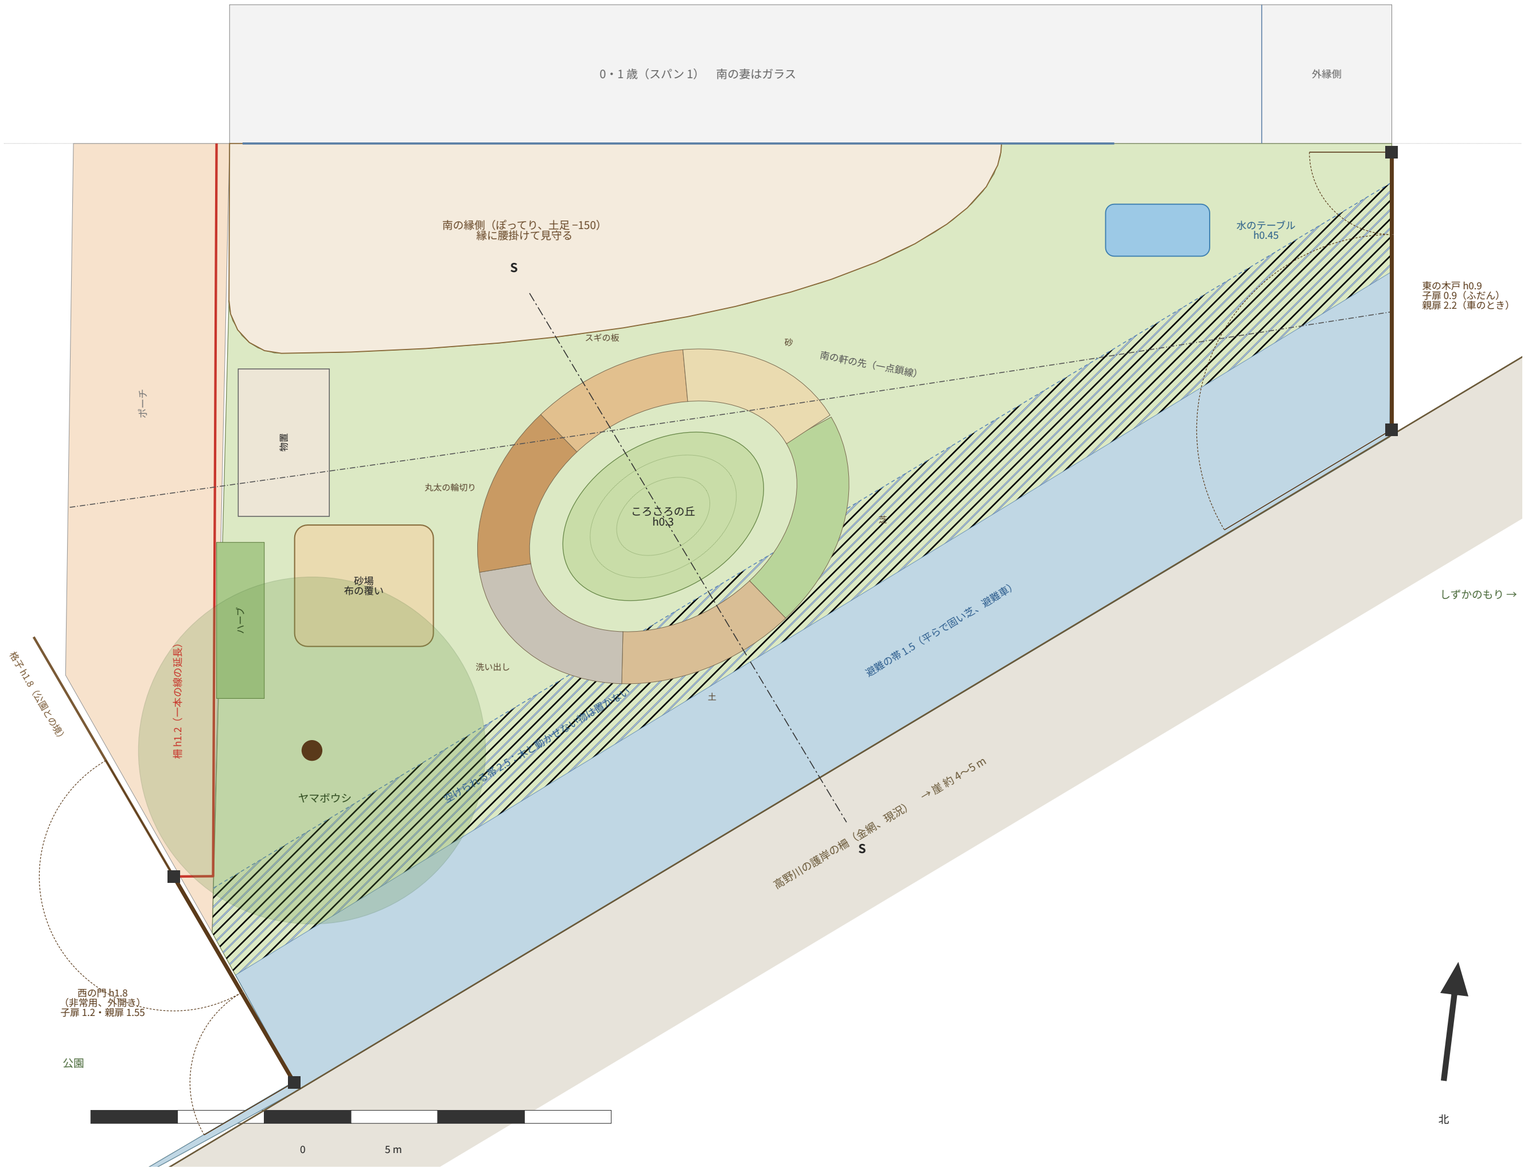

役割

いちばんの役割は 0〜2 歳の園庭（ユーザー）。大きな荷物・工事の車・避難の道は「副」：川沿いの帯 2.5 を「空けられる」ことだけ守る（避難の帯 1.5+1.0）。帯の中に木・動かせない物は置かない。少しの起伏と閉じられる砂場はよい（ユーザー）。避難の帯 1.5 は平らで固い芝（避難車が通る）。道そのものは描かない。

広さ

約 82 m²（南の縁側を除く）。そのうち空けられる帯 約 39 m²、帯の外 約 43 m²。

見守り

先生はぼってりの縁側の縁（+0.15）に腰掛けて全体を見る。木は 1 本だけで、ほかは膝より低い（ハーブ・丘 h0.3）。死角なし。南の妻のガラスごしに、0・1 歳の部屋からも見える。

ころころの丘

h0.3、2.5×1.7 m の楕円、芝。0 歳は這い上がり、1 歳は転がり、2 歳は駆け下りる。だいさんかくの築山（比叡の見立て）の赤ちゃん。帯 1.0 に半分掛かってよい（越えて車が通れる高さ）。

はだしの小径

丘を回る幅 0.6、一周 約 11 m。芝 → 土 → 洗い出し → 丸太の輪切り → スギのすのこ → 砂と、足の裏で順に触れる（本物に触れて育つ）。床と面一で段差なし。ばらの玉砂利は口に入るので使わない（洗い出しで固める）。

砂場

1.6×1.4、深さ 0.3、縁 h0.15（腰掛け）。布の覆い「おやすみの布」で閉じる（猫・落ち葉・雨）。ヤマボウシの北東で、昼すぎに木陰。縁側のすぐ前なので、0 歳も縁側から手を伸ばせる。

木陰の木

ヤマボウシ 1 本（落葉：夏は木陰、冬は日が入る。6 月の白い花、9 月の赤い実は食べられる、紅葉）。南西の隅、柵から 1 m。枝下 2.2、帯の側は枝を上げる。毒・とげ・チャドクガの木は使わない（園庭と同じ）。

水のテーブル

石の水盤 1.2×0.6、h0.45（1・2 歳が立って手が届く）、水深 5 cm、上水（先生が開ける蛇口）。軒の下の東の端、外縁側のスロープの脇。排水はすぐ東の雨の川へ（園庭）。使わないときは乾かす。

ハーブの帯

柵の内側に幅 0.55：レモンバーム・タイム・ラムズイヤー（ふわふわの葉）・ミント（鉢を埋めて広がりを止める）・這うローズマリー。触ってちぎって香る。柵の固さを和らげる。

軒の下

縁側と軒の先のあいだ（約 1〜2 m）は夏の日陰。0 歳はここにござを敷いて寝ころぶ、外気浴。

東の木戸

しずかのもりとの境を木戸で分ける（ユーザー）。v 15 の線、本館の南東の角から川の柵まで 約 3.2 m。親子の両開き：子扉 0.9 をふだん使い（西へ開く）、車のときだけ親扉 2.2（足に戸車、落とし棒）も開けて、車の向きに直角に測って あき 2.66 m（帯 2.5 より広い）。親扉は西へ約 120° 回して川の柵に沿わせて畳む。h0.9、スギの縦格子（すき間 80 以下、横桟なし）、掛け金は上の框の 2 段（h0.95 以上、2 歳の手が届かない）。すぐ東は雨の川（車は石の蓋で渡る）。

西の門

非常用の門（避難の帯の出口）。公園の北東の辺（川に直交）の上で、川の柵から 約 2.85 m。親子の両開き：子扉 1.2（避難車が通る、外へ 90° で川の柵に沿う）＋親扉 1.55（外へ 180° で格子に沿う）、あき 2.65 m。格子と同じ h1.8。内側からは鍵なしで開く（取っ手 h1.3 以上、二段の掛け金）、開くと事務に知らせる、公園の側からは鍵（セキュリティの線）。柵 h1.2 は南の端を 約 0.35 m 縮めて門の柱へ折り返す。

模型

丘は 3 mm（h0.3）の板 1 枚か、紙粘土。砂場・小径は彩色。木は園庭と同じ作り方。3dm のレイヤー 78（地形・遊び場）・79（植物）。

断面 S–S　1/50（丘の真ん中を川に向かって切る）

