平面図　1階　FL+1200 で切断／2階（西館）2FL+1000 で切断　1/100

高野川を下に（配置図と同じ向き）。2階は西の道路の外に同じ向きで置いた（遊戯室は吹き抜けから見下ろす）。一点鎖線は敷地の境

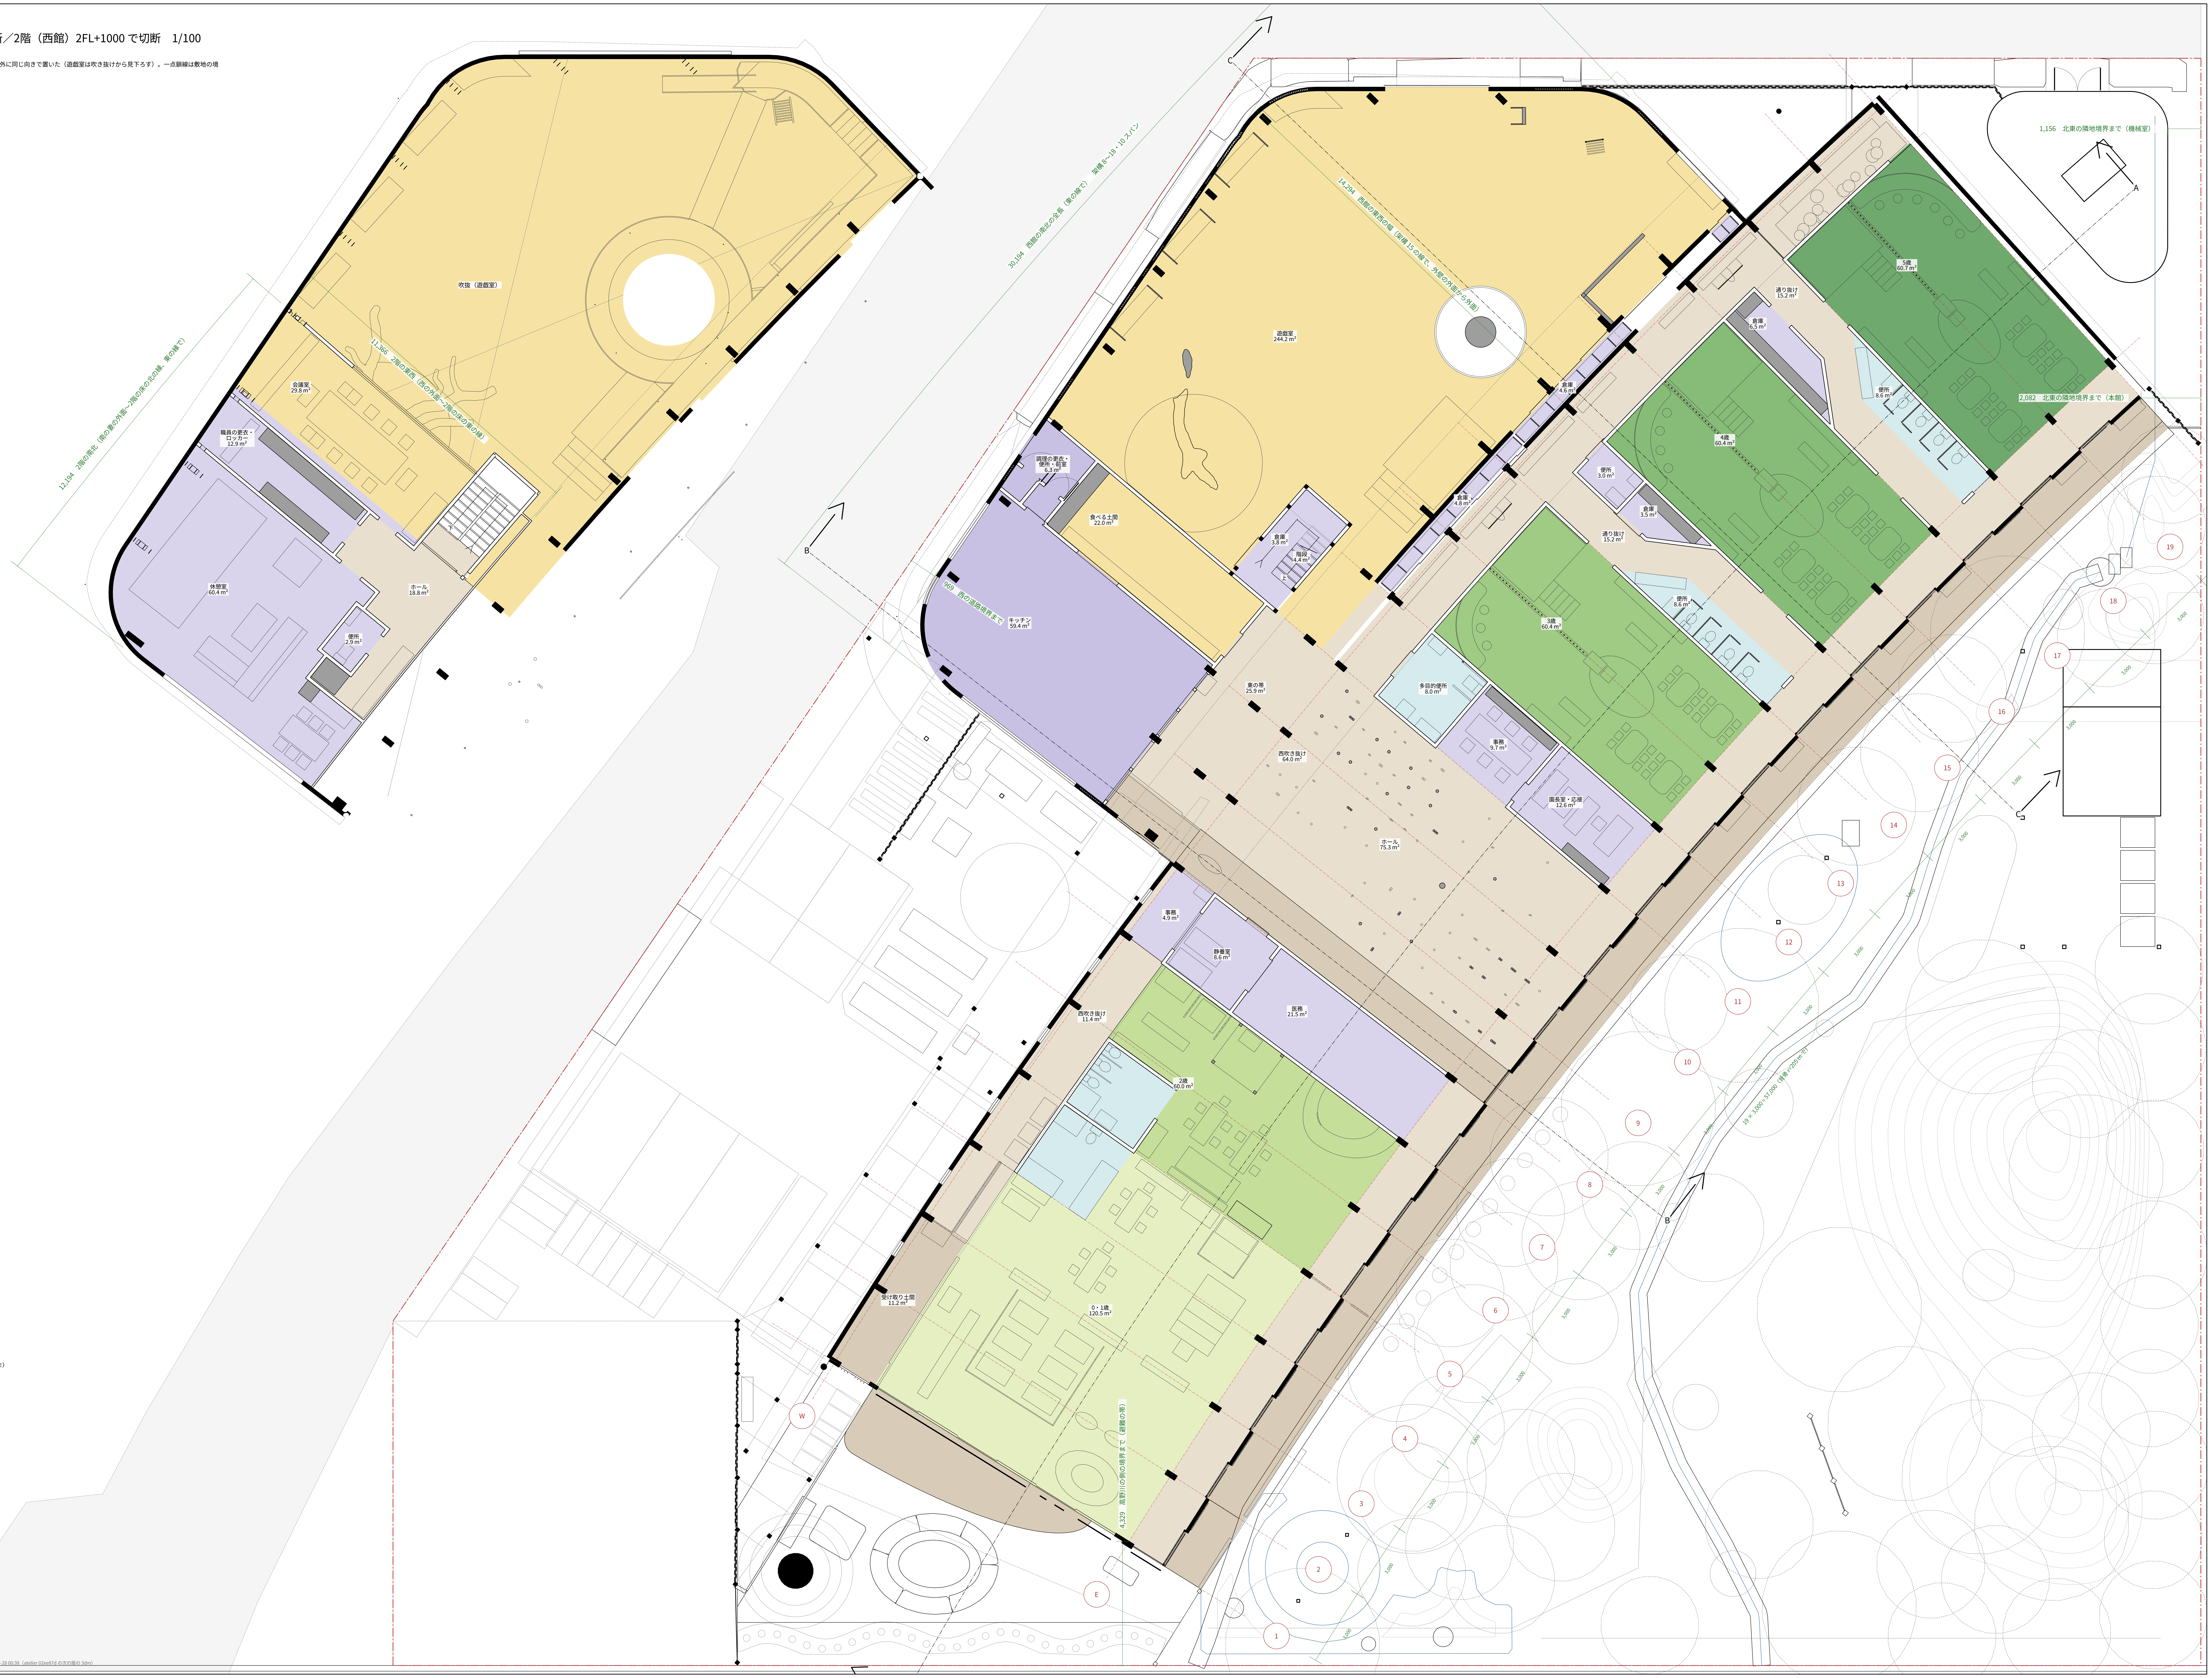
吹抜（遊戯室）
11,366　2階の東西（西の外面〜2階の床の東の縁）
12,194　2階の南北（南の妻の外面〜2階の床の北の縁、東の縁で）
会議室 29.8 m²
職員の更衣・ロッカー 12.9 m²
休憩室 60.4 m²
ホール 18.8 m²
便所 2.9 m²
下
30,194　西館の南北の全長（東の線で）　架構 8〜18・10 スパン
14,294　西館の東西の幅（架構 15 の線で、外壁の外面から外面）
1,156　北東の隣地境界まで（機械室）
2,082　北東の隣地境界まで（本館）
遊戯室 244.2 m²
調理の更衣・便所・前室 6.3 m²
食べる土間 22.0 m²
倉庫 3.8 m²
階段 4.4 m²
上
969　西の道路境界まで
キッチン 59.4 m²
東の帯 25.9 m²
西吹き抜け 64.0 m²
ホール 75.3 m²
多目的便所 8.0 m²
事務 9.7 m²
園長室・応接 12.6 m²
倉庫 4.6 m²
倉庫 4.8 m²
通り抜け 15.2 m²
倉庫 6.5 m²
便所 8.6 m²
5歳 60.7 m²
4歳 60.4 m²
便所 3.0 m²
倉庫 3.5 m²
通り抜け 15.2 m²
便所 8.6 m²
3歳 60.4 m²
事務 4.9 m²
静養室 8.6 m²
医務 21.5 m²
西吹き抜け 11.4 m²
2歳 60.0 m²
受け取り土間 11.2 m²
0・1歳 120.5 m²
4,329　高野川の側の境界まで（避難の帯）
19 × 3,000 = 57,000（背骨 r=205 m で）
3,000
A
B
C
W
E
1
2
3
4
5
6
7
8
9
10
11
12
13
14
15
16
17
18
19
N

部屋の色

- 🟩 0・1歳〜5歳
- 🟨 こどものみんなの場所（遊戯室・はれのま）
- ▨ 通り・つなぐ場所（はだし）
- 🟫 土足の床
- ▨ 大人の場所
- 🟪 キッチン・調理の更衣
- ▨ 水まわり

0　5 m

こどもたちの育ち舎　3dm（sodachiya.3dm）から自動で作図　2026-10-28 00:38（atelier 02ee87d の次の版の 3dm）