松ヶ崎こども園　1 敷地と自然環境・地域

地に足をつけて育つ

比叡から降りる冷気と高野川の流れが出会う松ヶ崎の扇状地に、こどもたちが地に足をつけて育つ場所をつくる。

ゆるやかな弧を東の比叡にひらく木造平屋の本館に 0 歳から 5 歳のすべての部屋を並べ、縁側と深い庇で園庭とつなぐ。比叡に見立てた築山と、用水を借りて高野川に見立てた小川を置く。

オープンキッチンを玄関ホールに面する園の中心に据え、食べることを日々の求心力とする。野菜くずをこどもたちの手で土に還し、命の循環を知る。園庭にはチクチクする植物、季節ごとに香る木と実のなる木を植え、こどもたちは手と鼻と舌で季節を知る。

3 m スパンの木造架構によるスケルトン＆インフィルで用途の変化を受け止める。地域から様々なものを借り、無駄をせず巡らせて、こども園として地域に返す。

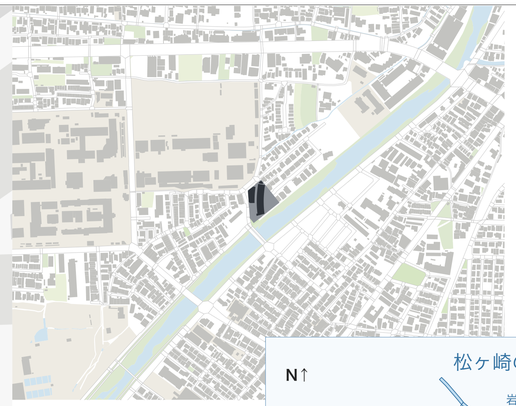

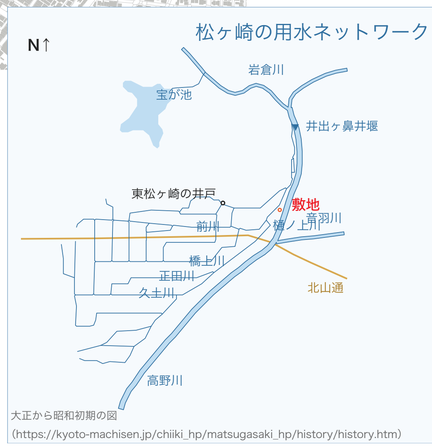

大正から昭和初期の図
(https://kyoto-machisen.jp/chiiki_hp/matsugasaki_hp/history/history.htm)

4 災害時の持ちつ持たれつ

大洪水が予想される場合の緊急避難先として京都工芸繊維大学と協定（京都市ハザードマップによる浸水深 1.5 m）。太陽光発電、蓄電池、地下水の利用によって、災害時に水を地域に提供。

3 お向かいさん

西の道の北半分は狭い道を挟んで向かいに住宅がある。圧迫感を与えないよう、この面の建物高さを 1 階程度に抑える。

6 間伐材を使った林

京都北山の北山杉の間伐材 141 本を、ホールの林として立てる。

2 車と自転車の出入りを南にまとめる

西の道の中ほどでは、道に突き出た木が見通しをさえぎる。車と送り迎えの自転車の出入りはこの木より南にまとめ、出入口にはスピードバンプを置いて速度を落とす。

1 小竹薮公園を残す

地域の記憶である小竹薮公園をそのまま残し、園への入口の前庭にする。そこから北へ、西の道沿いに幅 1 m の歩道を開き、歩く人を車から守る。

1 用水と地下水を借りる

井出ヶ鼻井堰に端を発する松ヶ崎の用水ネットワークから、水を借り、園庭の小川にする。また地下水を借り、京都の名水を園内で用いるとともに、井水ヒートポンプで空調を行う。災害時水道が止まった時には、地域に水を供給。定期的な水質チェックを行う。

2 野菜くずコンポスト

野菜くずや落ち葉をこどもたちの手で土に還す。発酵する暖かい土とミミズに驚く。野菜を育てる。命の循環を知る。

5 東の隣家への配慮

東の隣家との境は 1 m 下げ（セットバック）、園庭の小屋と植樹で視線と音をやわらげる。

3 高野川と比叡にみたてる

日本文化が育ててきた「みたて」。園内の小川と築山を高野川と比叡にみたてる。それを超えて視線を遠くにすると、高野川を超えて比叡の山。

4 水の行方を知る

小川は暗渠に隠さず高野川に注ぐ。屋根に降った雨は、雨落ちに落ち、雨水浸透側溝と雨庭を経て、溢れは高野川に。

5 風の道

夏の夜、高野川の谷を下りてくる涼しい風を、縁側の床下から 8m 高低差の吹き抜けに抜く。床下に冷えをためて、昼の冷房を抑える。

松ヶ崎こども園　2. ゾーニング、動線とリスクのデザイン／子供の環境

ゾーニング

- セキュリティの線
- 建物の外壁
- 避難経路
- コントロールされた死角・リスクエリア

建物の中
- 0〜2 歳の教室
- 3〜5 歳の教室
- 子供の場所
- 大人の場所
- 調理
- 倉庫
- トイレ
- 屋内の土足エリア

園庭
- みなみのさんかく（0〜2 歳専用）
- しずかのもり（0〜5 歳がいっしょに）
- だいさんかく（3〜5 歳）

外の世界
- 公開公園と見送り・お迎えエリア

園庭と植栽

- 山と川
  築山：2.5 m。川縁まで緩やかな傾斜
  小川：水深 3-5 cm。
  カキツバタ、ミツハギ、ギボウシ、カンスゲ、ハングショウ
- 常緑の木（緑取り）
- 香り（ふわふわの円）
- ちくちく（ヒイラギの葉・クリのイガ）
- 食べられる実
- 季節の草：セリ・ショウブ・鵜み草・ススキ・キク
- 柳のアーチ：毎年春に年長さん達が柳の枝で小さなアーチを作る。しずかのもりへの入口になる
- 水遊び場：木陰に床噴水と「あめのわ」(0-2 は霧、3-5 は雨)
- 砂場。帰る前に園児が、砂場さんおやすみ、と言って帆布をかける
- 石

建物沿いの雨落ち
南に流れて雨庭（洲浜）へ、溢れは高野川へ

動線とリスクのデザイン

朝の動き

公園の木戸からムベのアーチへ。0-1 歳は受け渡し土間から。3-5 歳はホールの土間「あまのがわ」を通って各自教室で靴を脱ぐ。帰りはその逆。スタップはスタッフ入口からセキュリティを超え、2 階の更衣室へ。調理さんは専用の入口から。食材は勝手口で検収。

食事

時間をずらしながら調理完了。保育士さんが運ぶ。思い思いに、保育室、遊戯室やホールの林の中、外に出て園庭で食べる。

リスクのデザイン

こどもが育つには、冒険と、たくさんの良い失敗が必要だ。大きな危険は取り除き、小さな失敗は許すようにデザインした。

見守りと死角

死角は建物内外通してごく少なくなるよう保った。

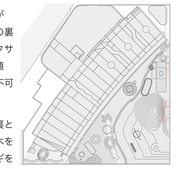

右に赤のドットで示すのが残った死角である。築山の裏の急斜面にはコデマリ、クサボケなどの株立ち低木を植え、転がり落ちることを不可能とする。

また、死角となる築山の裏と小屋の後ろにも株立ち低木を植え、また入口にヒイラギを植える。敢えて立ち入る冒険家は、ヒイラギに刺され、低木で手足をすりむき、怒られるだろう。しかし得るものがあるはず。

園庭の植物

園庭から毒のある植物を除き、食べられる実のなる木を多く植えた。桑の実を食べて口も服も紫にする。ヒイラギの葉や、栗のいがの痛みを経験する。表のかまどで焼いてみんなで食べるクリはご褒美。

水

事故の危険性を排除できないプールを廃止し、その代わりに地面からの地面からの噴水とレインシャワーの水遊び場を作った。小川はくるぶしの深さ、かつ 0-2 歳エリアに入らない。

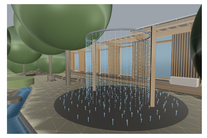

あめのわ。足元からの小さな噴水と頭の上からの雨。足洗い場を兼ねる。

保育室

保育室 0-2 歳

保育室 3-5 歳

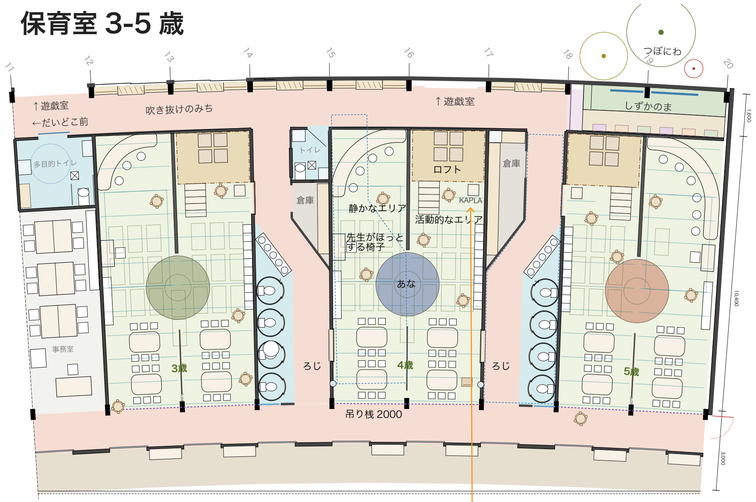

越屋根を見上げる吹き抜け
常に空気の流れがあるのでここに洗濯物を干す

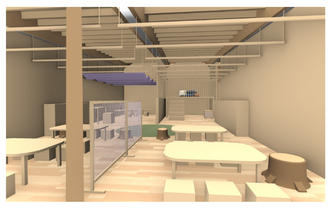

どの部屋も吊り桟で保育士さんが子供達の空間を作りやすくなっている。

自分を積み木の建築で閉じ込める
未来のアーキテクトを育てる

松ヶ崎こども園　３平面図　１階

平面図　1階　FL+1500 で切断　1/100

遊戯室：くすのきひろば

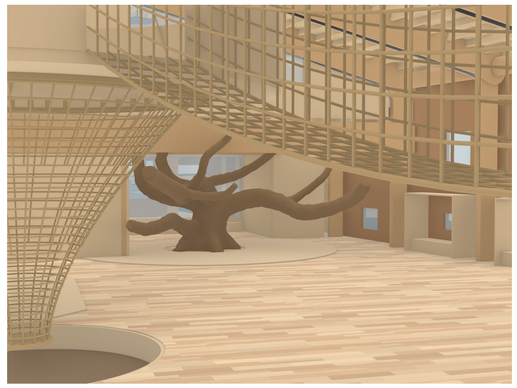

遊戯室には大きな楠正の切り株があり「くすのきひろば」と呼ばれる。木をハグしたり、登って本を読んだりできる。ネットや階段からキャットウォークに登り、すべり台で降りたり、ロープの吊り橋で戻ってきたりする。箱の中にこもる「いおり」が壁沿いに三つある。2F の会議室から見下ろすことができる。

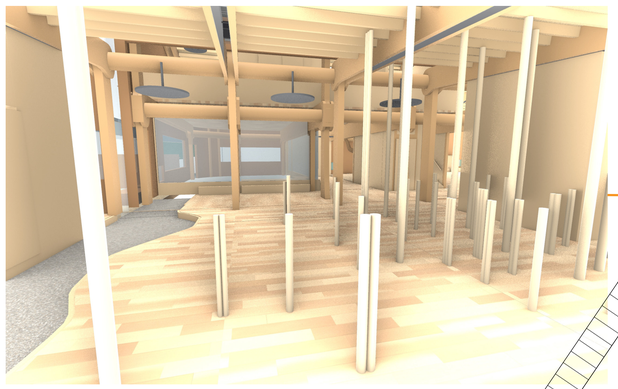

だいどこの見えるホール。靴のまま教室に向かうための「あまのがわ」通路、北山杉間伐材を使った「はやし」がここにある。右には開放型の事務室。

N

部屋の色

- 0-1歳〜5歳
- こどものみんなの場所（くすのきひろば・はれのま）
- 通り・つなぐ場所（はだし）
- 土足の床
- 大人の場所
- キッチン・調理の前衣
- 水まわり

0　5 m

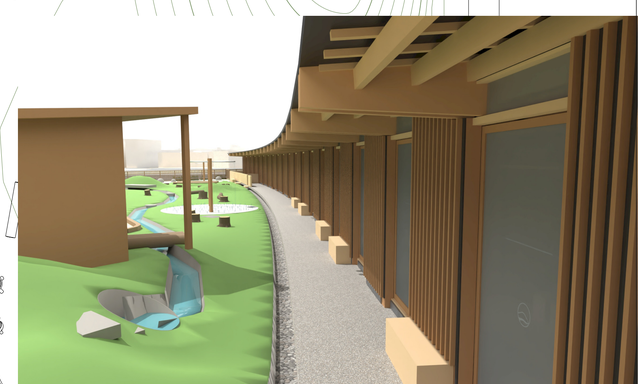

ゆるやかに弧を描くデザイン

松ヶ崎こども園　４平面図　２階

平面図　2階（西館）　2FL+1000 で切断　1/100

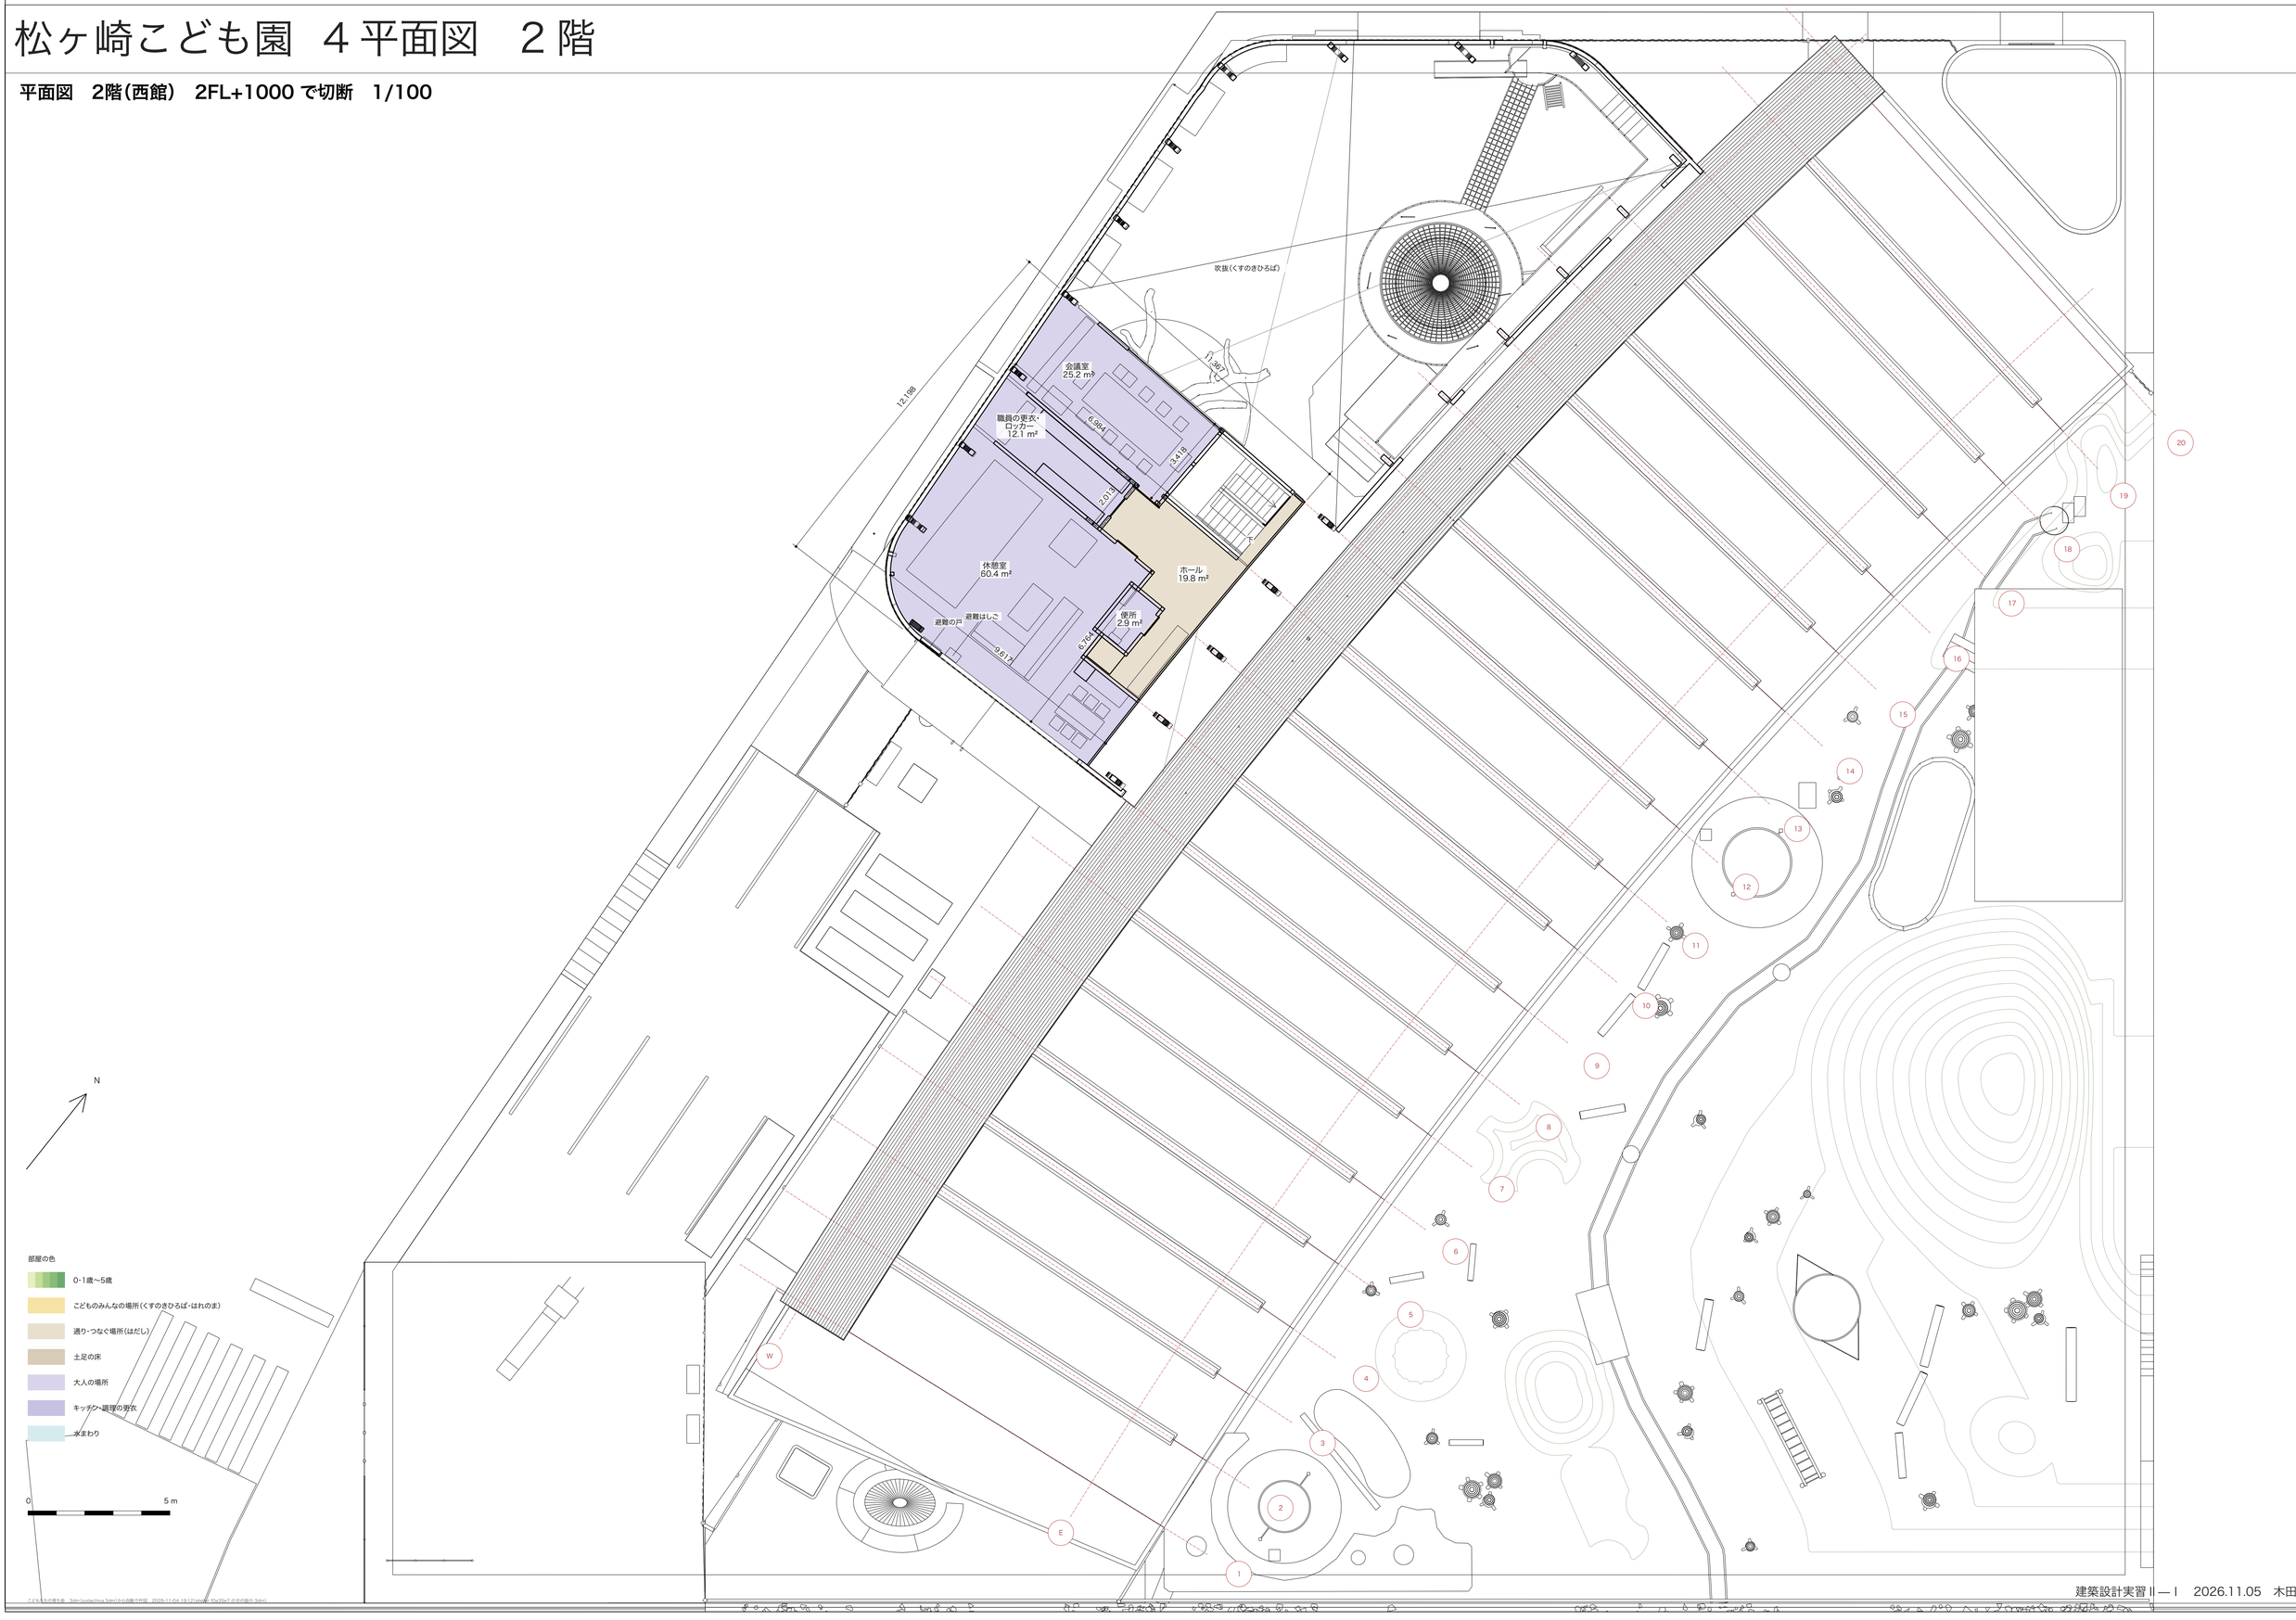

松ヶ崎こども園　５立面・景観

園庭の側の立面図　1/100　（円弧の中心の方向から見る、右が北）

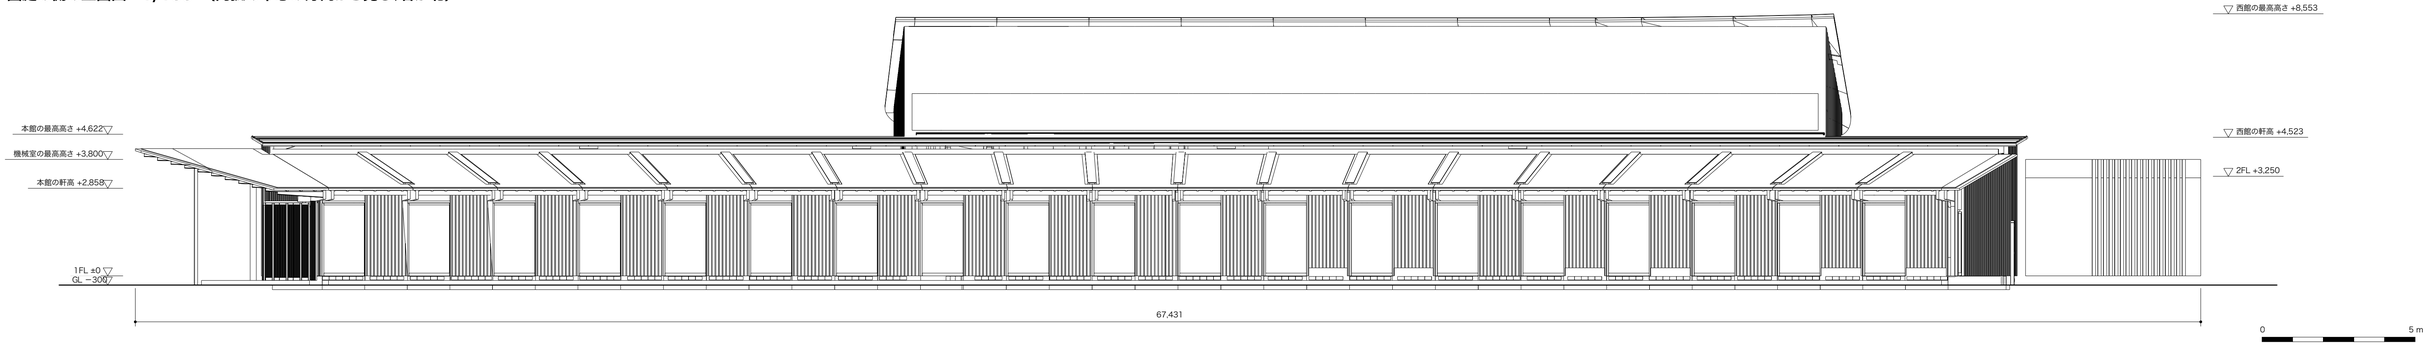

道路の側の立面図　1/100　（西の道路から。右が南）

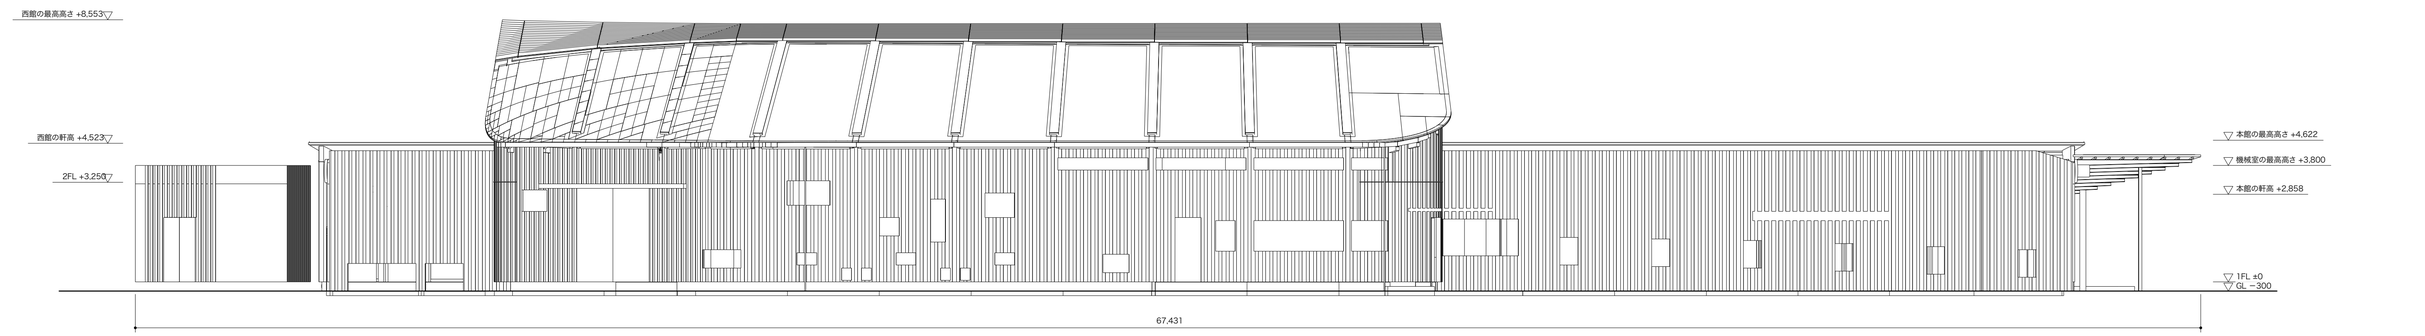

透視図（A4）　公園の角から西の道を見る　目の高さ 1.5 m、左に向かいの住宅、右に西館の低い軒

沿川の景観　昼　高野川の向こう岸の歩道から、目の高さ 1.5 m

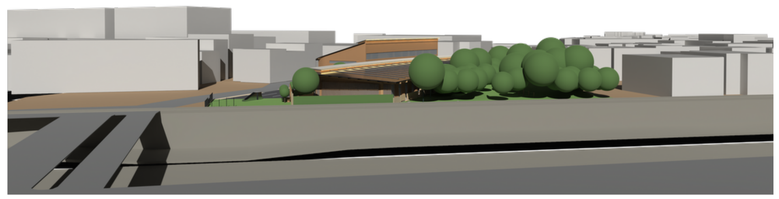

沿川の景観　夜　高野川の向こう岸の歩道から、目の高さ 1.5 m　本館と西館の越屋根の光

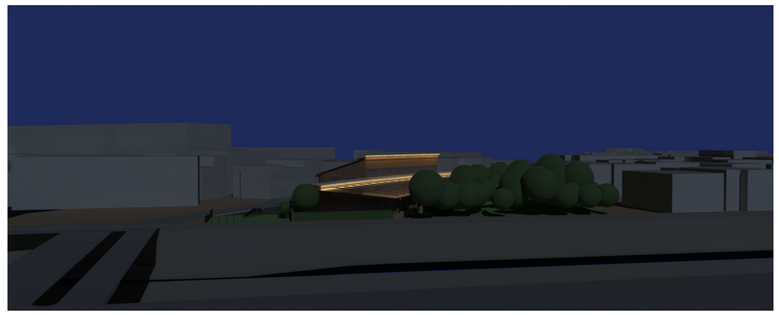

景観の法規

用途地域：第一種低層住居専用地域（都市計画法）。最高の高さは西館の棟で約 9.0 m（GL から）。

風致地区（京都市風致地区条例）：高野川特別修景地域（同条例第 6 条第 1 項による指定、許可基準は基準告示第 7 条）。右岸の基準：既存の樹木を保全する／河川に面する部分に植栽帯を設ける／建築物は原則として河川の側に勾配のある下屋を設けた和風の外観とする。

対応：川の側に園庭の林と生垣、南に深い軒（下屋）、深い軒と縁側・杉の大和張りの板壁・ゆるい勾配の屋根。

同基準第 7 条第 1 項 (80)：屋根に太陽光発電装置を原則として設けない。

対応：屋根材と一体の太陽電池で、黒い金属の屋根と見分けがつかず周辺の風致に不調和でない（同 (80) の例外）。こども園で、同第 7 条第 2 項の例外（建築物全体のデザイン・公益上やむを得ない学校等の施設）にもあたるとする。

遠景デザイン保全区域（京都市眺望景観創生条例）：外壁・屋根に禁止色を用いない、山並みと調和する。

対応：黒い金属の屋根、木の色のまま。

素材と色

- 木の柱・梁（木の色のまま）
- 杉の大和張り（銀鼠に枯れる）
- 黒い金属の屋根（太陽光一体）
- 越屋根のガラス・縁側の白
- 生垣と園庭の緑

建築設計実習 II — I　2026.11.05　木田

建物と、その手前の外構（塀・柵・木戸・樹・柱、細い線）。駐車・駐輪・室内の家具は省いた。反色は屋根の面。薄い青はガラス（塗は細い反色の線で透けて見える）。建物の外形は太い線。

松ヶ崎こども園　６断面・構造

断面図 A　1/100　縦断(展開)

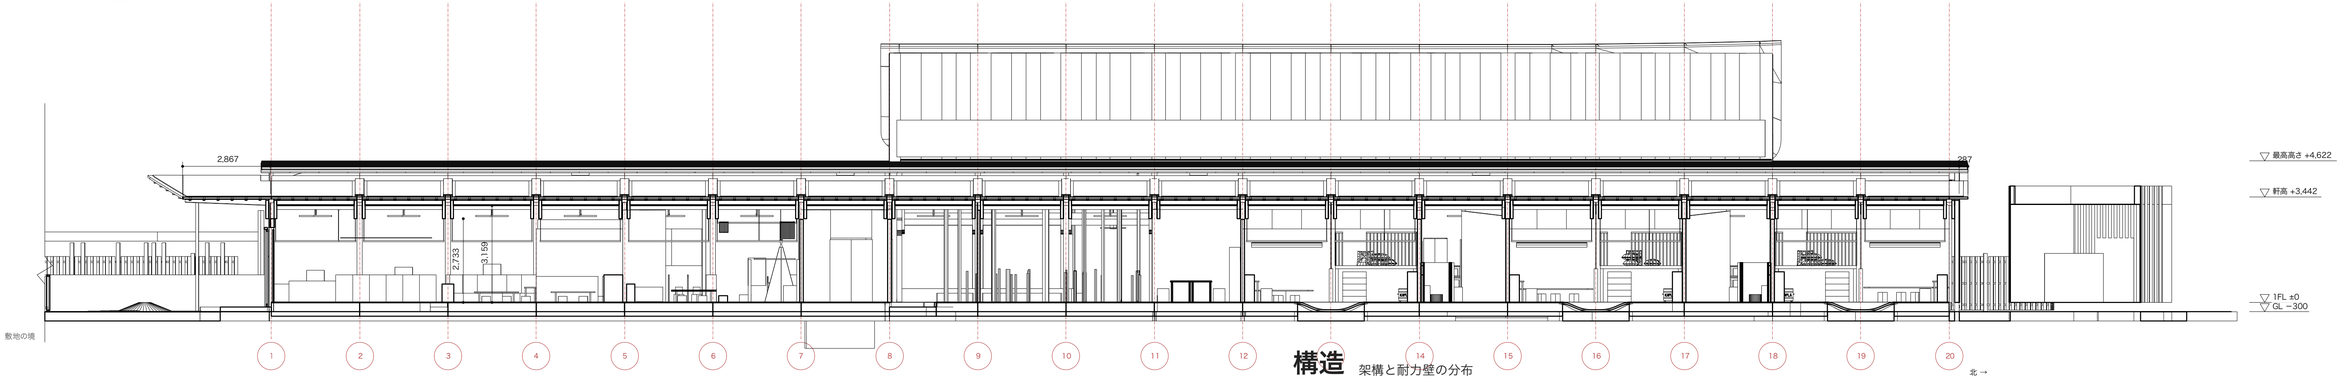

断面図 C　1/100　４歳・くすのきひろばのたつまきネット(スパン 14+2.75)　北を見る

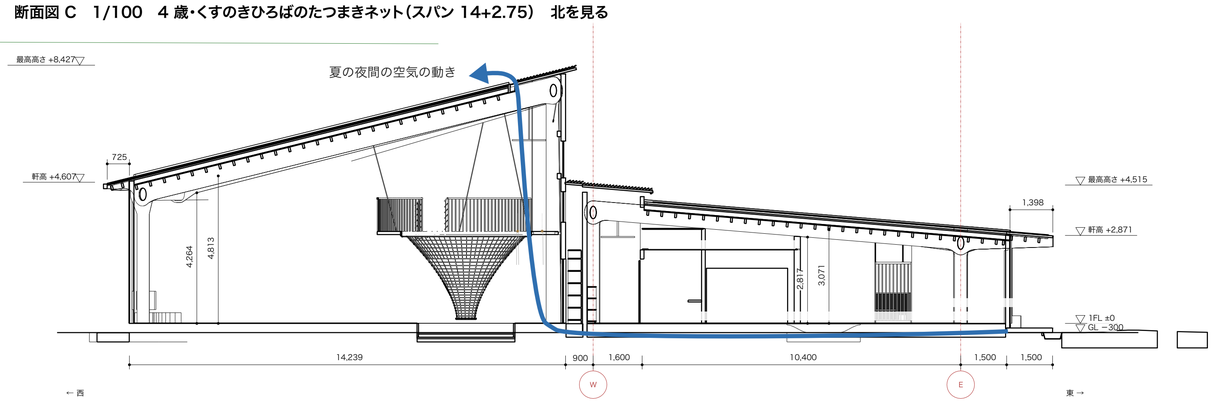

構造　架構と耐力壁の分布

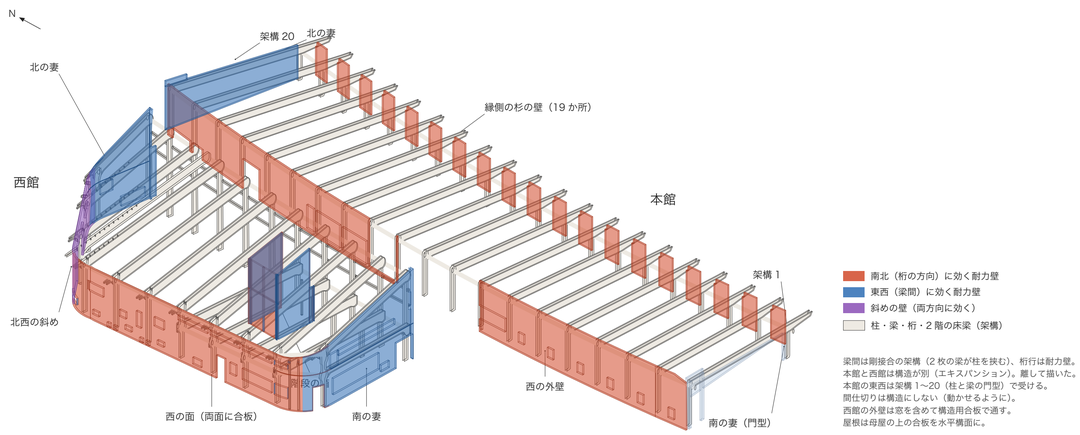

梁間は剛接合の架構（2 枚の梁が柱を挟む）、桁行は耐力壁。
本館と西館は構造が別（エキスパンション）。離して描いた。
本館の東西は架構 1〜20（柱と梁の門型）で受ける。
間仕切りは構造にしない（動かせるように）。
西館の外壁は窓を含めて構造用合板で通す。
屋根は母屋の上の合板を水平構面に。

季節ごとの空気環境

夏は夜の外気で床下の重さを冷やし、昼はその冷えと、触れて冷たい壁と天井扇で過ごす。冬は閉じて床から暖め、熱と湿気を逃がさない。春と秋は床下から越屋根へ風を通す。

季節	開け閉め	動かすもの	効くもの
夏の昼	窓・越屋根・床下の入口を閉じる	放射冷房のパネル・天井扇（下向き）・床下の送風	深い軒、夜に冷やした底板
夏の夜	縁側のガラリと西館の越屋根を開く（本館の越屋根は閉じる）	開け閉めは自動（外気が涼しいとき・雨で閉じる）	外気が床下の底板を冷やす。くすのきひろばの吹き抜けの高低差約 8 m で引く
春・秋	窓・越屋根を開く	機械は止める	通風（梁間から越屋根へ）
冬	すべて閉じる	床下の暖房・全熱交換の換気・加湿・天井扇（上向きに弱く）	断熱と気密。ガラス戸の際の床からの暖気がガラスの冷えを止める

> **放射冷房のパネル**
> 保育室とくすのきひろばの壁、こどもの手の届く高さに置く。表面は約 15℃で、触れて「つめた！」とわかる。結露した水を外へ流して除湿も兼ねる。風が無いので静かで、午睡を妨げない。

環境への配慮（LEED v5 Gold を目指す）

LEED v5（USGBC）　https://www.usgbc.org/leed/v5

統合的なプロセス（IP）	一つの形で二つ以上を解く。本館の弧＝朝の日と、夏の夜に谷を下りる冷気（1 枚目）。片流れの屋根＝景観と、越屋根へ上る空気の流れ（断面 C）。縁側の段のガラリ＝夜の外気を床下へ入れ、ガラス戸をすっきり保つ。井戸＝冷暖房の熱源と、災害時の近隣の水
立地と交通（LT）	車は 5 台に絞り、送迎は徒歩と自転車（駐輪 21 台）。西の道に歩道を開く
持続可能な敷地（SS）	小竹薮公園と既存の木を残す。園庭の林。雨庭と浸透側溝で雨を敷地に返す
水の効率（WE）	雨を庭へ。地下水を使う
エネルギーと大気（EA）	断熱・気密、深い軒と遮熱 Low-E で日射を切る、ベタ基礎の底板に夜の冷えをためる、放射冷房と全熱交換、地下水を熱源にしたヒートポンプ、屋根材型の太陽光と蓄電池
材料と資源（MR）	北山杉の間伐材、木造。3 m の架構は残し中は変えられる（スケルトン&インフィル）。野菜くずのコンポスト
室内環境の質（EQ）	光の筋の鏡面で奥まで昼光。風の音のない放射冷房。自然換気（床下→梁間→越屋根）。静養室と大人の便所は別の換気。2 階の窓から川と空
地域の優先（PR）	災害時の持ちつ持たれつ：太陽光と蓄電池の電気と、地下水を近隣に提供できる。浸水のときは京都工芸繊維大学へ避難の協定

面積表　m²（壁芯、3dm から自動）

室	要求	計画
乳児室（0〜1 歳）	約 60×2	120.5
保育室（2 歳）	約 60	60.1
保育室（3〜5 歳）	約 60×3	181.0
遊戯室	240 以上	262.7
便所	適宜	17.2
食堂	必要に応じて	なし
園庭	350 以上	987.2
事務室	約 60	64.4
休憩室	約 60	60.4
医務室	約 30	30.1
調理室	約 60	65.7
便所（大人用）	適宜	13.9
機械室	約 30	30.0
倉庫	約 30	37.6
駐車場	5 台以上	5 台（うち搬入 1）
駐輪スペース	適宜	21 台（保護者 12・職員 9）
延床（2,000 以内）		1,313.5

inspired by　参照した建築

Asilo Nido Iride　Mario Cucinella Architects・Guastalla・2015
→梁の列が並ぶ長細い本館と、外に付く付属の建物

Tamedia　坂茂・Zürich・2013
→梁の端の楕円の頭と、それを貫く楕円の桁

レイモンド斑鳩こども園　キノアーキテクツ・斑鳩・2026
→室内に木を立てる（ホールの北山杉）・内と外の回廊・回廊と遊戯室に居場所

KAIT 工房　石上純也・厚木・2008
→柱の配列：見る向きで景色が変わる並び

認定こども園らみどり　はりゅうウッドスタジオ・須賀川・2026
→内と外の二重の縁側、遊具を置かない地形の園庭

仙田満の園舎　環境デザイン研究所
→擂鉢のネット、キャットウォーク、ニッチ

Waldorf School of the Peninsula　California
→遊戯室の切り株

スターバックス京都二寧坂ヤサカ茶屋店　町家の改修・京都・2017
→放射冷房