
育ち舎　南の入口まわり（キッチン・はれのま・窓口の帯・静養室・医務）　ラフ

1/100（A3）　2026-10-29　架構の番号は南から（架構kは南の妻から3(k−1) m、スパンkは架構kとk+1のあいだ）。面積（芯々、概算）：キッチン 60 m²　はれのま 20 m²　窓口の帯 5.4 m²　静養室 8.6 m²　医務 22 m²

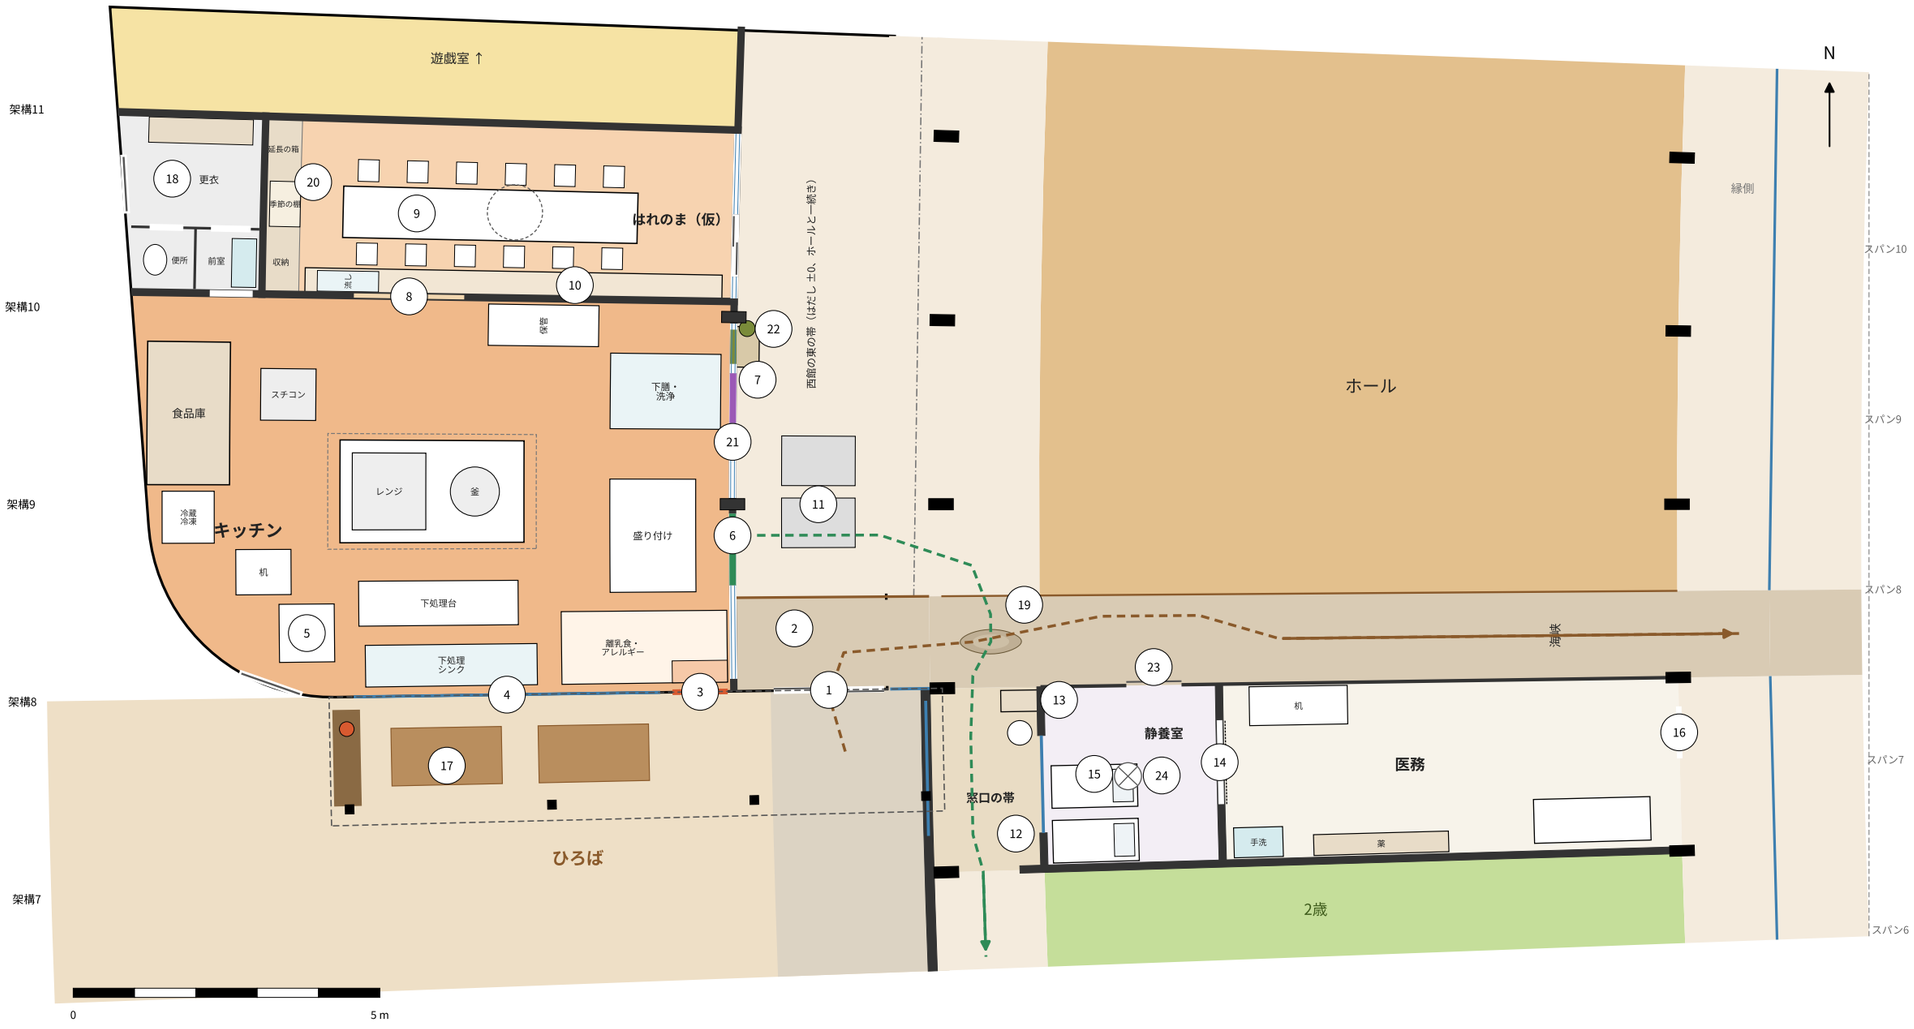

1　入口（西館の南の面、引き戸1.8）。すき間はガラス

2　海峡の延長（土足 −150）。框から北は東の帯（はだし ±0）

3　「今日のごはん」の窓（子どもの高さ、中は見本の棚）

4　キッチンの南のガラス（下処理が見える）

5　検収（勝手口のすぐ内側）

6　配膳口（盛り付け → ワゴン）

7　返却口（配膳口と分ける、一方通行）

8　見える台所（はれのまへの受け渡しの窓）

9　はれのまの机（幅0.8、12人）

10　キッチン沿いのカウンターh600（子どもの流し・おやつの台・食育）

11　配膳のワゴン置き場（東の帯）

12　窓口の帯（受付・見守り、西の窓から小径の出口・手水・入口が見える。机仕事はスパン11の記録・連絡の机）

13　おはようの窓口（低いカウンター、海峡に向く）。前に飛び石

14　静養室と医務のあいだの戸（保健師が看る）

15　静養室（こども用ベッド×2、戸で閉じ換気は別、窓口の帯から室内窓h0.9〜2.0）

16　医務の戸（内縁側から、先生が子どもを連れてくる）

17　下屋の下の縁台とお茶の棚（電気ポットはh1100の棚の上：給湯ロック・転倒湯もれ防止・蒸気レス・マグネットプラグ）

18　調理の職員の更衣・便所・前室（外から直接：西の面の戸 → 更衣 → 前室 → キッチン）

19　飛び石（窓口の帯の正面、流れに沿うレンズ形0.4×1.0、上面は床の高さ）

20　はれのまの収納（西の端の壁、延長の箱・季節の棚）

21　東の面：腰壁h450の上を2階の床の下までガラス（二本線、戸の上は欄間）。破線の円は天井扇φ0.9

22　生ごみの受け取り台（返却口の隣、東の帯の側h500。3〜5歳のコンポスト当番がふた付きのバケツを受け取る）

23　静養室の戸（海峡へ、お迎えの保護者が迎えに来る）

24　静養室の換気扇（天井から真上へ、屋根の上の換気の頭。給気は戸の下から）

--- 緑：配膳の保育士と2歳の道（配膳口 → 東の帯 → ホールの西 → 飛び石で海峡を渡る → 窓口の帯を抜ける → 2歳の道）。--- 茶：3〜5歳（入口 → 海峡 → 縁側、おはようの窓口の前を通る）。キッチンは 検収 → 下処理 → 加熱 → 盛り付け → 配膳口、返却口 → 洗浄 → 保管 の一方通行。

西館の東の帯とすき間は、エキスパンションをはさんでホールと一続き（はだし ±0）。本館の西の壁はホールの範囲では開く。はれのまの日常：朝夕の延長保育（キッチンが近く、補食・おやつ）、5歳のお手伝い当番・おやつづくり、3〜5歳がクラスごとに順番に食べる日。ときどき：誕生会・行事食・保護者の試食会・離乳食の相談。